ÍNDICE DE PEÇAS DESENHADAS

DESENHO Nº	DESCRIÇÃO	ESCALA
00	Índice de Peças Desenhadas	S/E
01	Planta de Implantação	1:100
02	Planta do Piso -1	1:100
03	Planta do Piso 0	1:100
04	Planta do Piso 1	1:100
05	Planta da Cobertura	1:100
06	Corte A (Esquemático)	1:100
07	Pormenores	S/ESC

GAPLR
ENGENHARIA LDA

Telem.: 967 068 588 | fax: 219 863 894 | GAPLRgeral@gmail.com

PROJETO

CONSTRUÇÃO DE MORADIA UNIFAMILIAR

ESPECIALIDADE

REDE DE AGUAS

DESIGNAÇÃO

INDÍCE DE PEÇAS DESENHADAS

REQUERENTE

Natasha Lara Santric

LOCAL

Praceta da Abadia, Lote 13
Ericeira
Mafra

DATA	PROCESSO	ESCALA
Julho 2026	3775	1/125

TÉCNICO

Eng.º Luis Reis
21981 O.E.

DESENHO N.º

00

Topo do muro:
41.23

39.74

Topo do muro:
40.40

Topo do muro:
39.83

38.32

38.35

38.16

38.17

38.19

38.13

38.20

38.02

38.10

38.03

38

38.11

37.97

37.87

37.91

37.87

37.95

37.88

Praceta Da Abadia

1 Lugar de Estacionamento

+37.50

Alçado Norte

Alçado Poente

Alçado Nascente

Alçado Sul

+38.28

+38.27

+38.26

+35.28

+40.29

+43.55

+39.35

Limite do lote de acordo com o Levantamento Topográfico

Topo do muro:
41.72

Topo do muro:
40.03

Beirado:
41.36

Topo do muro:
39.45

Topo do muro:
38.84

Beirado:
45.87

GAPLR
ENGENHARIA LDA

Telem.: 967 068 588 | fax: 219 863 894 | GAPLRgeral@gmail.com

PROJETO

CONSTRUÇÃO DE MORADIA UNIFAMILIAR

ESPECIALIDADE

REDE DE AGUAS

DESIGNAÇÃO

PLANTA DE IMPLANTAÇAO

REQUERENTE


Natasha Lara Santric

LOCAL

Praceta da Abadia, Lote 13
Ericeira
Mafra

DATA	PROCESSO	ESCALA
Julho 2026	3775	1/100

TÉCNICO	DESENHO N.º
Eng.º Luis Reis 21981 O.E.	**01**

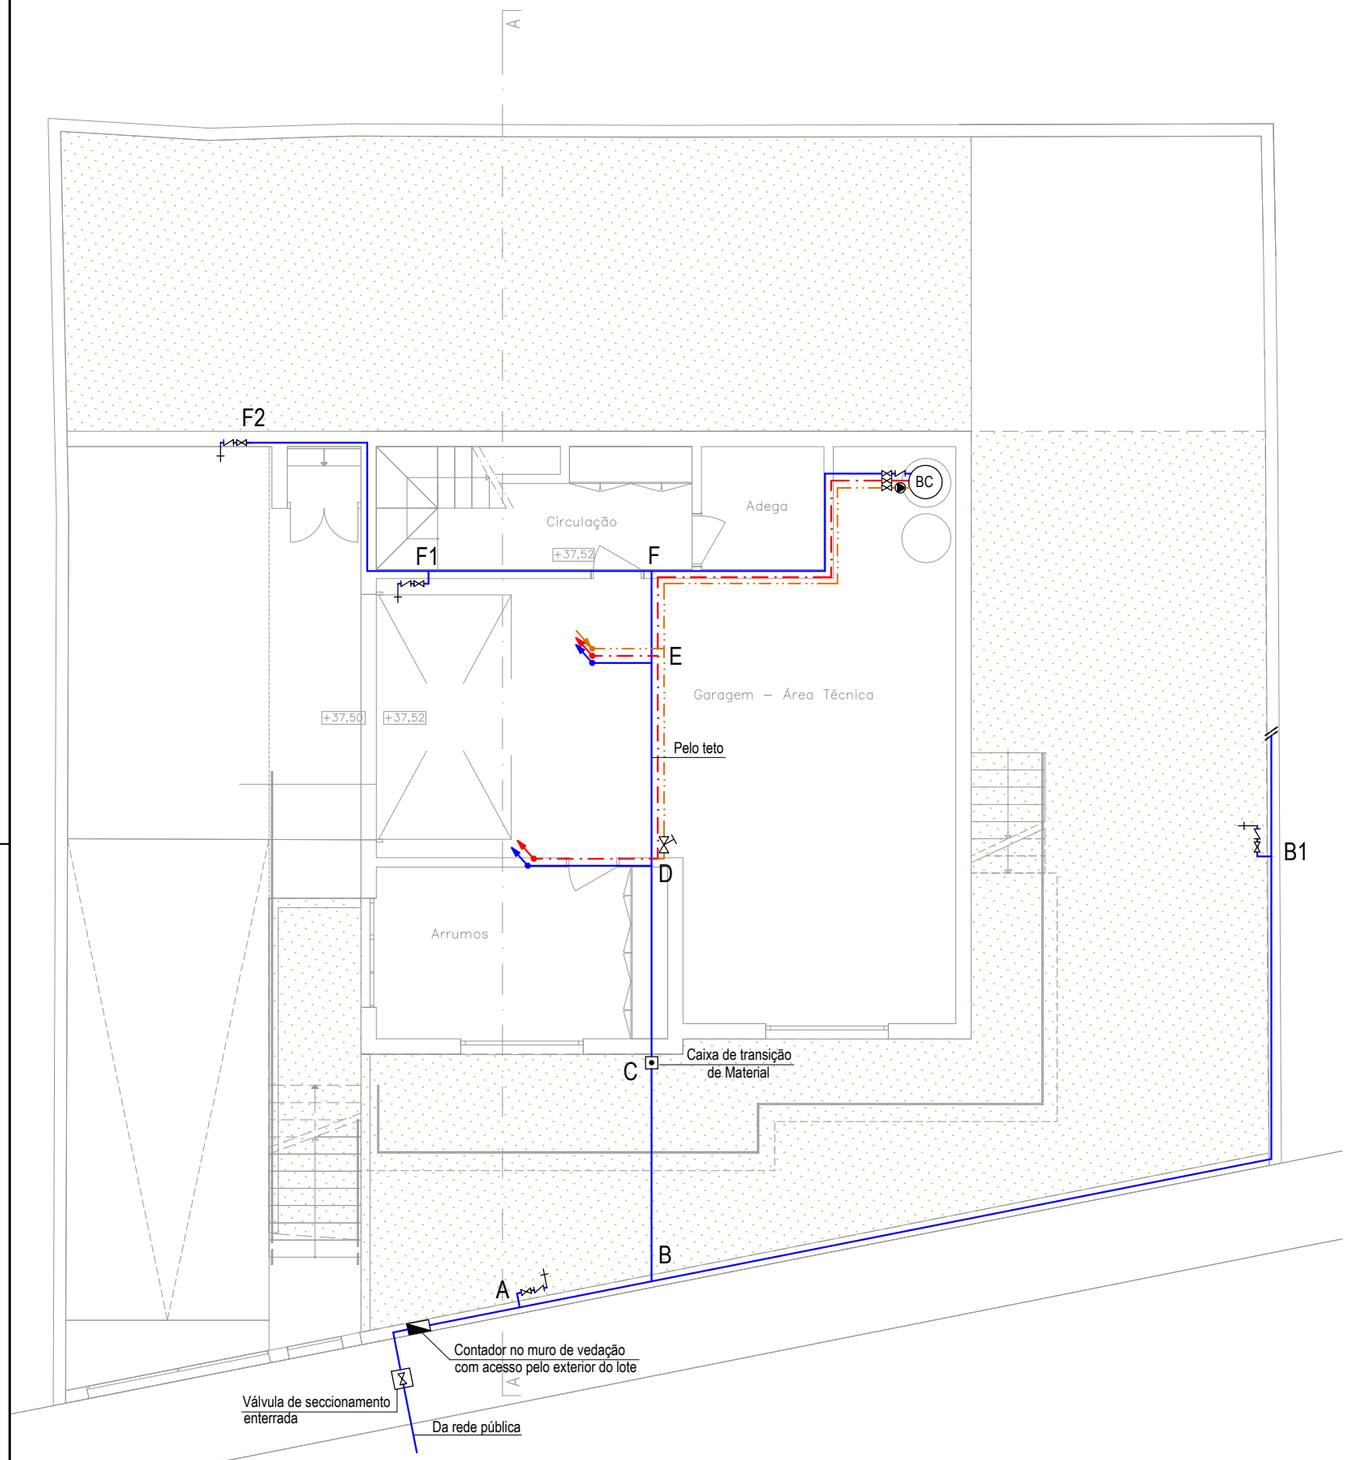

RAMAIS INDIVIDUAIS

APARELHOS	ÁGUA FRIA	ÁGUA QUENTE	DN EXT.
QUARTO DE BANHO			
- Lavatório	◦	◦	16
- Bidet	◦	◦	16
- Autoclismo	◦		16
- Banheira	◦	◦	20
- Duche	◦	◦	16
COZINHA / LAVANDARIA			
- Pia lava loiça	◦	◦	20
- M. lavar loiça	◦		16
- M. lavar roupa	◦		20

REDE DE ÁGUA FRIA

Troço	Mat.	DN	Int.
PISO -1			
E - G	MC	Ø 32	26,00
F1 - F2	MC	Ø 20	15,00
F - F1	MC	Ø 26	20,00
F - BC	MC	Ø 32	26,00
E - F	MC	Ø 32	26,00
D - E	MC	Ø 32	26,00
C - D	MC	Ø 32	26,00
B - C	PEAD	Ø 32	27,20
B2 - B3	PEAD	Ø 25	21,00
B1 - B2	PEAD	Ø 25	21,00
B - B1	PEAD	Ø 25	21,00
A - B	PEAD	Ø 40	32,60
Cont. - A	PEAD	Ø 40	32,60

REDE DE ÁGUA QUENTE

Troço	Mat.	DN	Int.
PISO -1			
E - G	MC	Ø 26	20,00
E - D1	MC	Ø 20	15,00
BC - E	MC	Ø 32	26,00

SIMBOLOGIA (REDE DE ÁGUAS):

	Canalização de água fria
	Canalização de água quente
	Canalização de água quente de retorno
	Canalização de água fria - Reutilização de águas pluviais
	Circuito fechado do fluído solar
	Contador
	Xadrêz
	Olho de boi
	Caixa de transição de material
	Boca de Incêndio exterior
BC	Bomba de Calor
	Torneira de serviço
	Torneira ou válvula de seccionamento
	Válvula de flutuador
	Válvula de Balanceamento
	Torneira misturadora
	Válvula de retenção
	Bomba circuladora para sistema de retorno de AQS
	Prumadas ascendentes com mudança de piso
	Prumadas descendentes com mudança de piso

MATERIAIS:

- Tubagens exteriores são em PEAD e desenvolvem-se pelo pavimento, com exceção das indicadas.
- Tubagens interiores são em Multicamada e desenvolvem-se pelas paredes e sobre tetos falsos, com exceção das indicadas.

GAPLR
ENGENHARIA LDA
Telem.: 967 068 588 | fax: 219 863 894 | GAPLRgeral@gmail.com

PROJETO
CONSTRUÇÃO DE MORADIA UNIFAMILIAR

ESPECIALIDADE
REDE DE AGUAS

DESIGNAÇÃO
PLANTA DO PISO -1


REQUERENTE
Natasha Lara Santric

LOCAL
Praceta da Abadia, Lote 13
Ericeira
Mafra

DATA	PROCESSO	ESCALA
Julho 2026	3775	1/125

TÉCNICO
Eng.º Luis Reis
21981 O.E.

DESENHO N.º
02

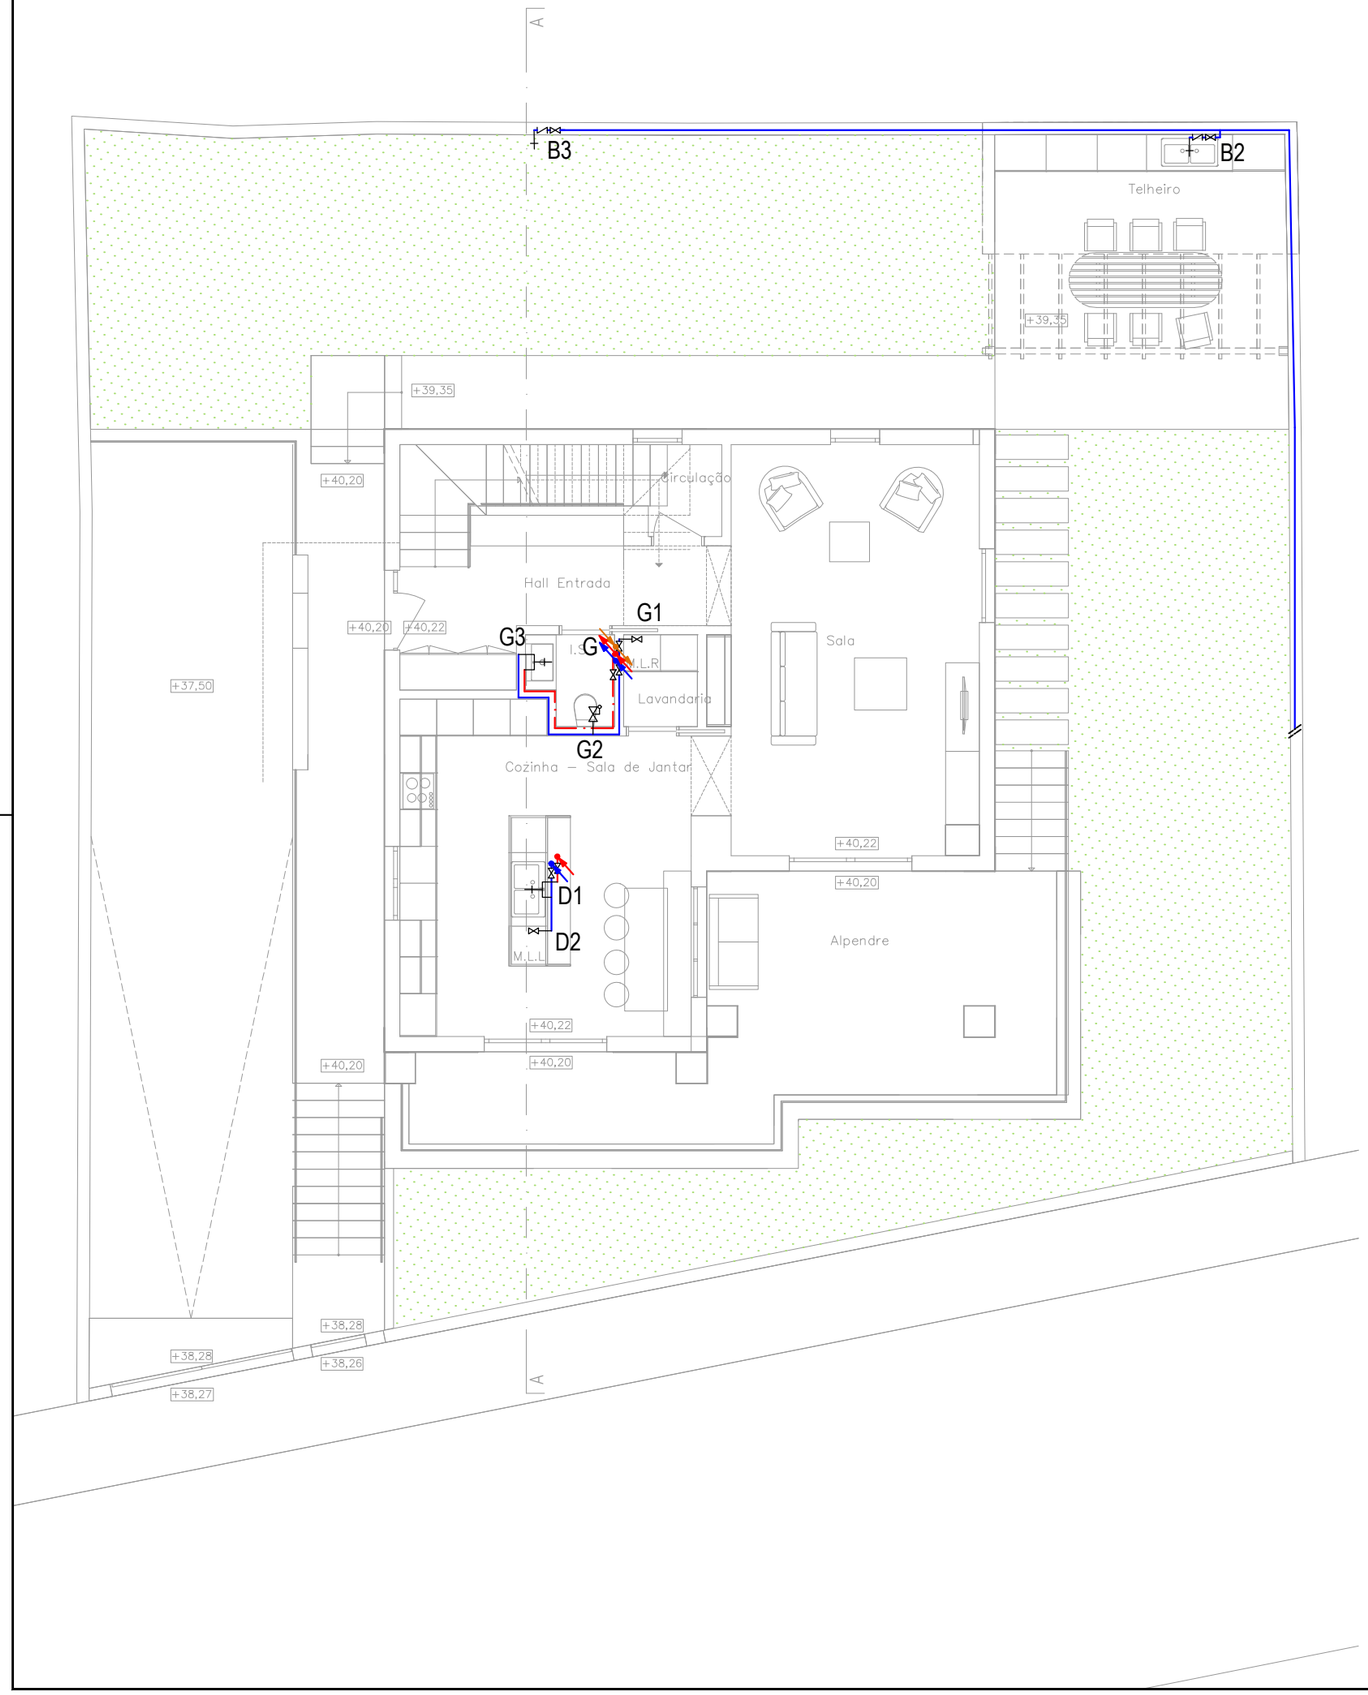

RAMAIS INDIVIDUAIS

APARELHOS	ÁGUA FRIA	ÁGUA QUENTE	DN EXT.
QUARTO DE BANHO			
- Lavatório	◦	◦	16
- Bidet	◦	◦	16
- Autoclismo	◦		16
- Banheira	◦	◦	20
- Duche	◦	◦	16
COZINHA / LAVANDARIA			
- Pia lava loiça	◦	◦	20
- M. lavar loiça	◦		16
- M. lavar roupa	◦		20

REDE DE ÁGUA FRIA

Troço	Mat.	DN	Int.
PISO 0			
G - H	MC	**Ø 26**	20,00
G2 - G3	MC	**Ø 16**	11,50
G - G2	MC	**Ø 20**	15,00
G - G1	MC	**Ø 20**	15,00
D1 - D2	MC	**Ø 20**	15,00
D - D1	MC	**Ø 26**	20,00

REDE DE ÁGUA QUENTE

Troço	Mat.	DN	Int.
PISO 0			
G - H	MC	**Ø 26**	20,00
G - G3	MC	**Ø 16**	11,50

SIMBOLOGIA (REDE DE ÁGUAS):

	Canalização de água fria
	Canalização de água quente
	Canalização de água quente de retorno
	Canalização de água fria - Reutilização de águas pluviais
	Circuito fechado do fluído solar
	Contador
	Xadrêz
	Olho de boi
	Caixa de transição de material
	Boca de Incêndio exterior
BC	Bomba de Calor
	Torneira de serviço
	Torneira ou válvula de seccionamento
	Válvula de flutuador
	Válvula de Balanceamento
	Torneira misturadora
	Válvula de retenção
	Bomba circuladora para sistema de retorno de AQS
	Prumadas ascendentes com mudança de piso
	Prumadas descendentes com mudança de piso

MATERIAIS:

- Tubagens exteriores são em PEAD e desenvolvem-se pelo pavimento, com exceção das indicadas.
- Tubagens interiores são em Multicamada e desenvolvem-se pelas paredes e sobre tetos falsos, com exceção das indicadas.

GAP LR
ENGENHARIA LDA

Telem.: 967 068 588 | fax: 219 863 894 | GAPLRgeral@gmail.com

PROJETO

CONSTRUÇÃO DE MORADIA UNIFAMILIAR

ESPECIALIDADE

REDE DE AGUAS

DESIGNAÇÃO

PLANTA DO PISO 0

REQUERENTE

Natasha Lara Santric

LOCAL

Praceta da Abadia, Lote 13
Ericeira
Mafra


DATA	PROCESSO	ESCALA
Julho 2026	3775	1/125

TÉCNICO

Eng.º Luis Reis
21981 O.E.

DESENHO N.º

03

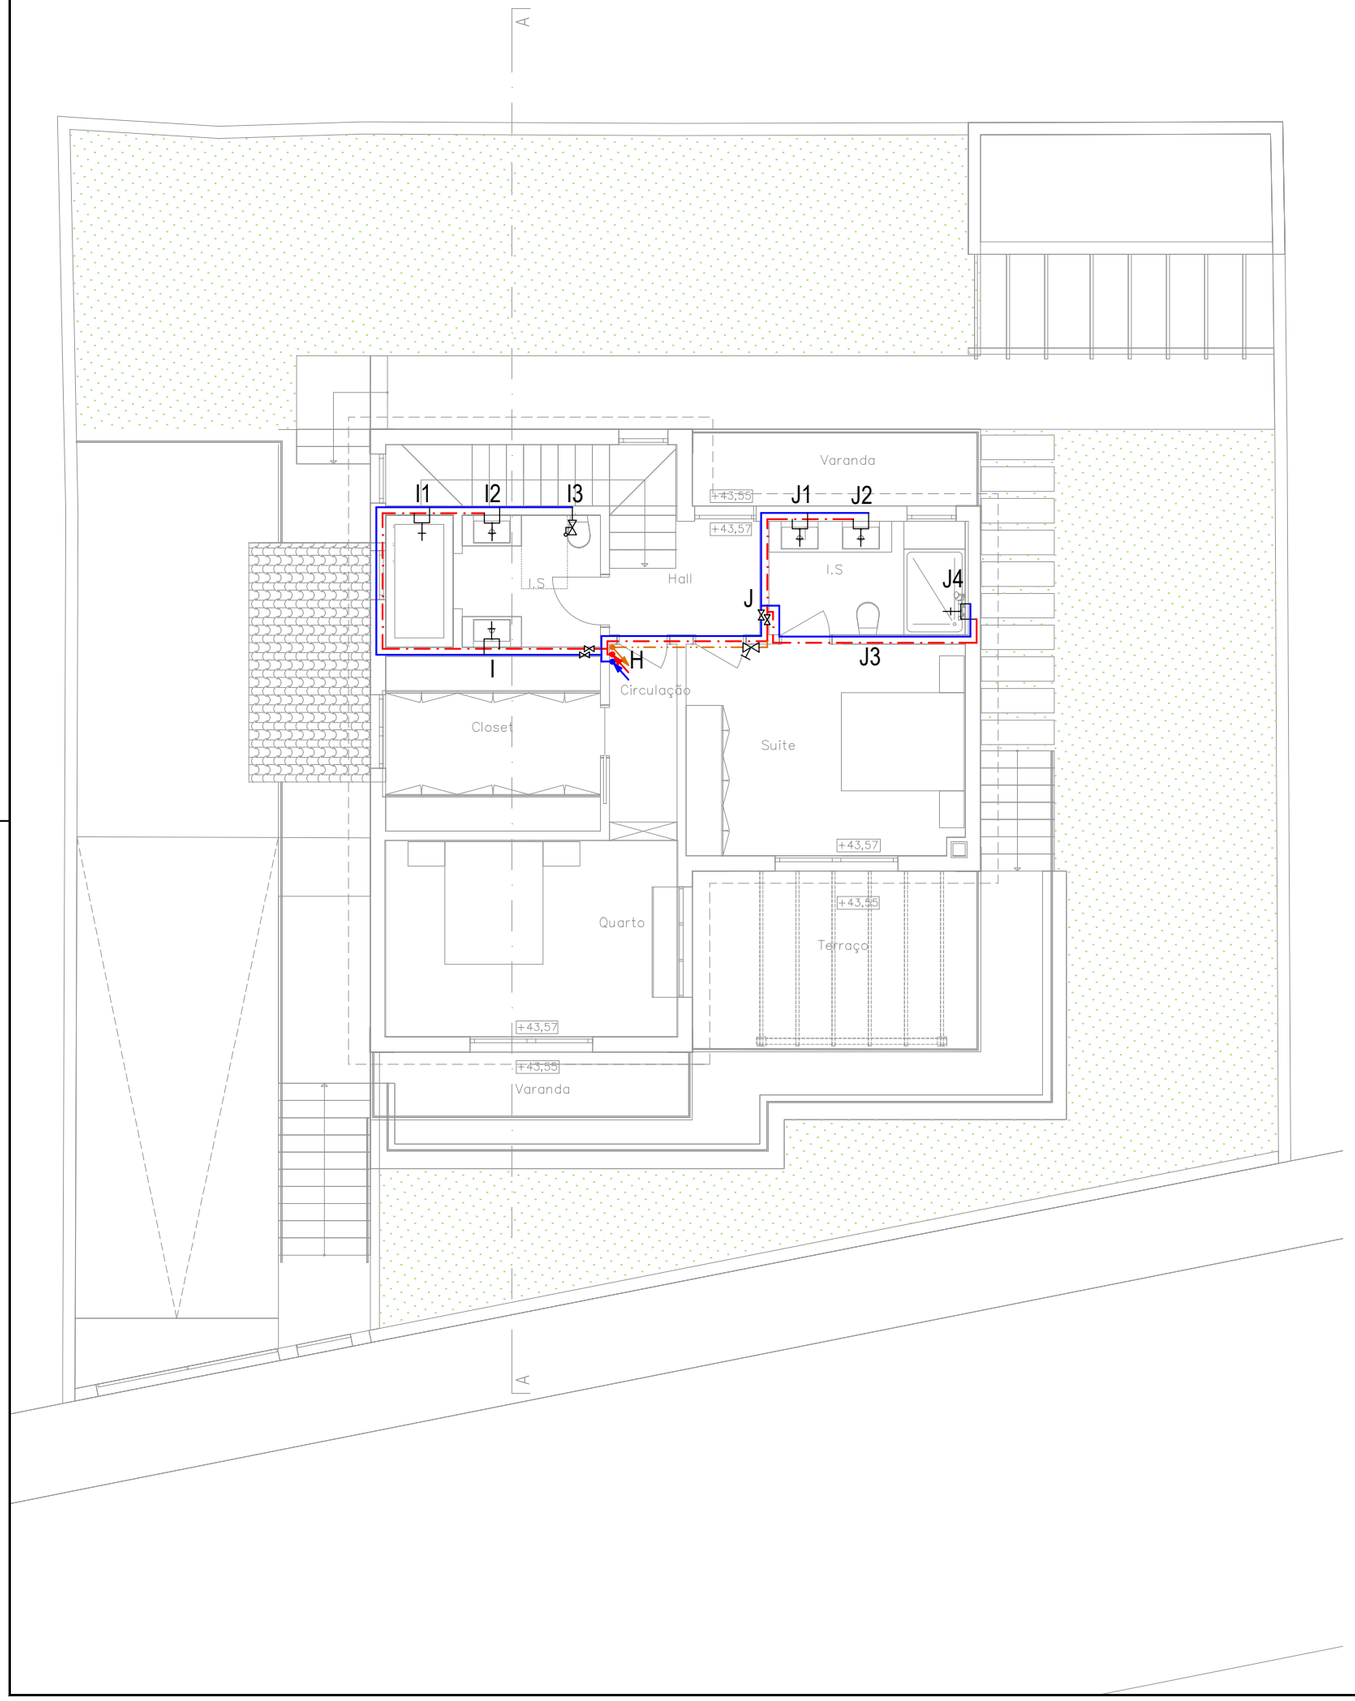

RAMAIS INDIVIDUAIS

APARELHOS	ÁGUA FRIA	ÁGUA QUENTE	DN EXT.
QUARTO DE BANHO			
- Lavatório	◦	◦	16
- Bidet	◦	◦	16
- Autoclismo	◦		16
- Banheira	◦	◦	20
- Duche	◦	◦	16
COZINHA / LAVANDARIA			
- Pia lava loiça	◦	◦	20
- M. lavar loiça	◦		16
- M. lavar roupa	◦		20

REDE DE ÁGUA FRIA

Troço	Mat.	DN	Int.
PISO 1			
J3 - J4	MC	Ø 16	11,50
J - J3	MC	Ø 20	15,00
J1 - J2	MC	Ø 16	11,50
J - J1	MC	Ø 20	15,00
H - J	MC	Ø 26	20,00
I2 - I3	MC	Ø 16	11,50
I1 - I2	MC	Ø 20	15,00
I - I1	MC	Ø 26	20,00
H - I	MC	Ø 26	20,00

REDE DE ÁGUA QUENTE

Troço	Mat.	DN	Int.
PISO 1			
J - J4	MC	Ø 16	11,50
J1 - J2	MC	Ø 16	11,50
J - J1	MC	Ø 20	15,00
H - J	MC	Ø 26	20,00
I1 - I2	MC	Ø 16	11,50
I - I1	MC	Ø 26	20,00
H - I	MC	Ø 26	20,00

SIMBOLOGIA (REDE DE ÁGUAS):

	Canalização de água fria
	Canalização de água quente
	Canalização de água quente de retorno
	Canalização de água fria - Reutilização de águas pluviais
	Circuito fechado do fluído solar
	Contador
	Xadrêz
	Olho de boi
	Caixa de transição de material
	Boca de Incêndio exterior
BC	Bomba de Calor
	Torneira de serviço
	Torneira ou válvula de seccionamento
	Válvula de flutuador
	Válvula de Balanceamento
	Torneira misturadora
	Válvula de retenção
	Bomba circuladora para sistema de retorno de AQS
	Prumadas ascendentes com mudança de piso
	Prumadas descendentes com mudança de piso

MATERIAIS:

- Tubagens exteriores são em PEAD e desenvolvem-se pelo pavimento, com exceção das indicadas.
- Tubagens interiores são em Multicamada e desenvolvem-se pelas paredes e sobre tetos falsos, com exceção das indicadas.

GAPLR
ENGENHARIA LDA
Telem.: 967 068 588 | fax: 219 863 894 | GAPLRgeral@gmail.com

PROJETO
CONSTRUÇÃO DE MORADIA UNIFAMILIAR

ESPECIALIDADE
REDE DE AGUAS

DESIGNAÇÃO
PLANTA DO PISO 1


REQUERENTE
Natasha Lara Santric

LOCAL
Praceta da Abadia, Lote 13
Ericeira
Mafra

DATA	PROCESSO	ESCALA
Julho 2026	3775	1/125

TÉCNICO
Eng.º Luis Reis
21981 O.E.

DESENHO N.º
04

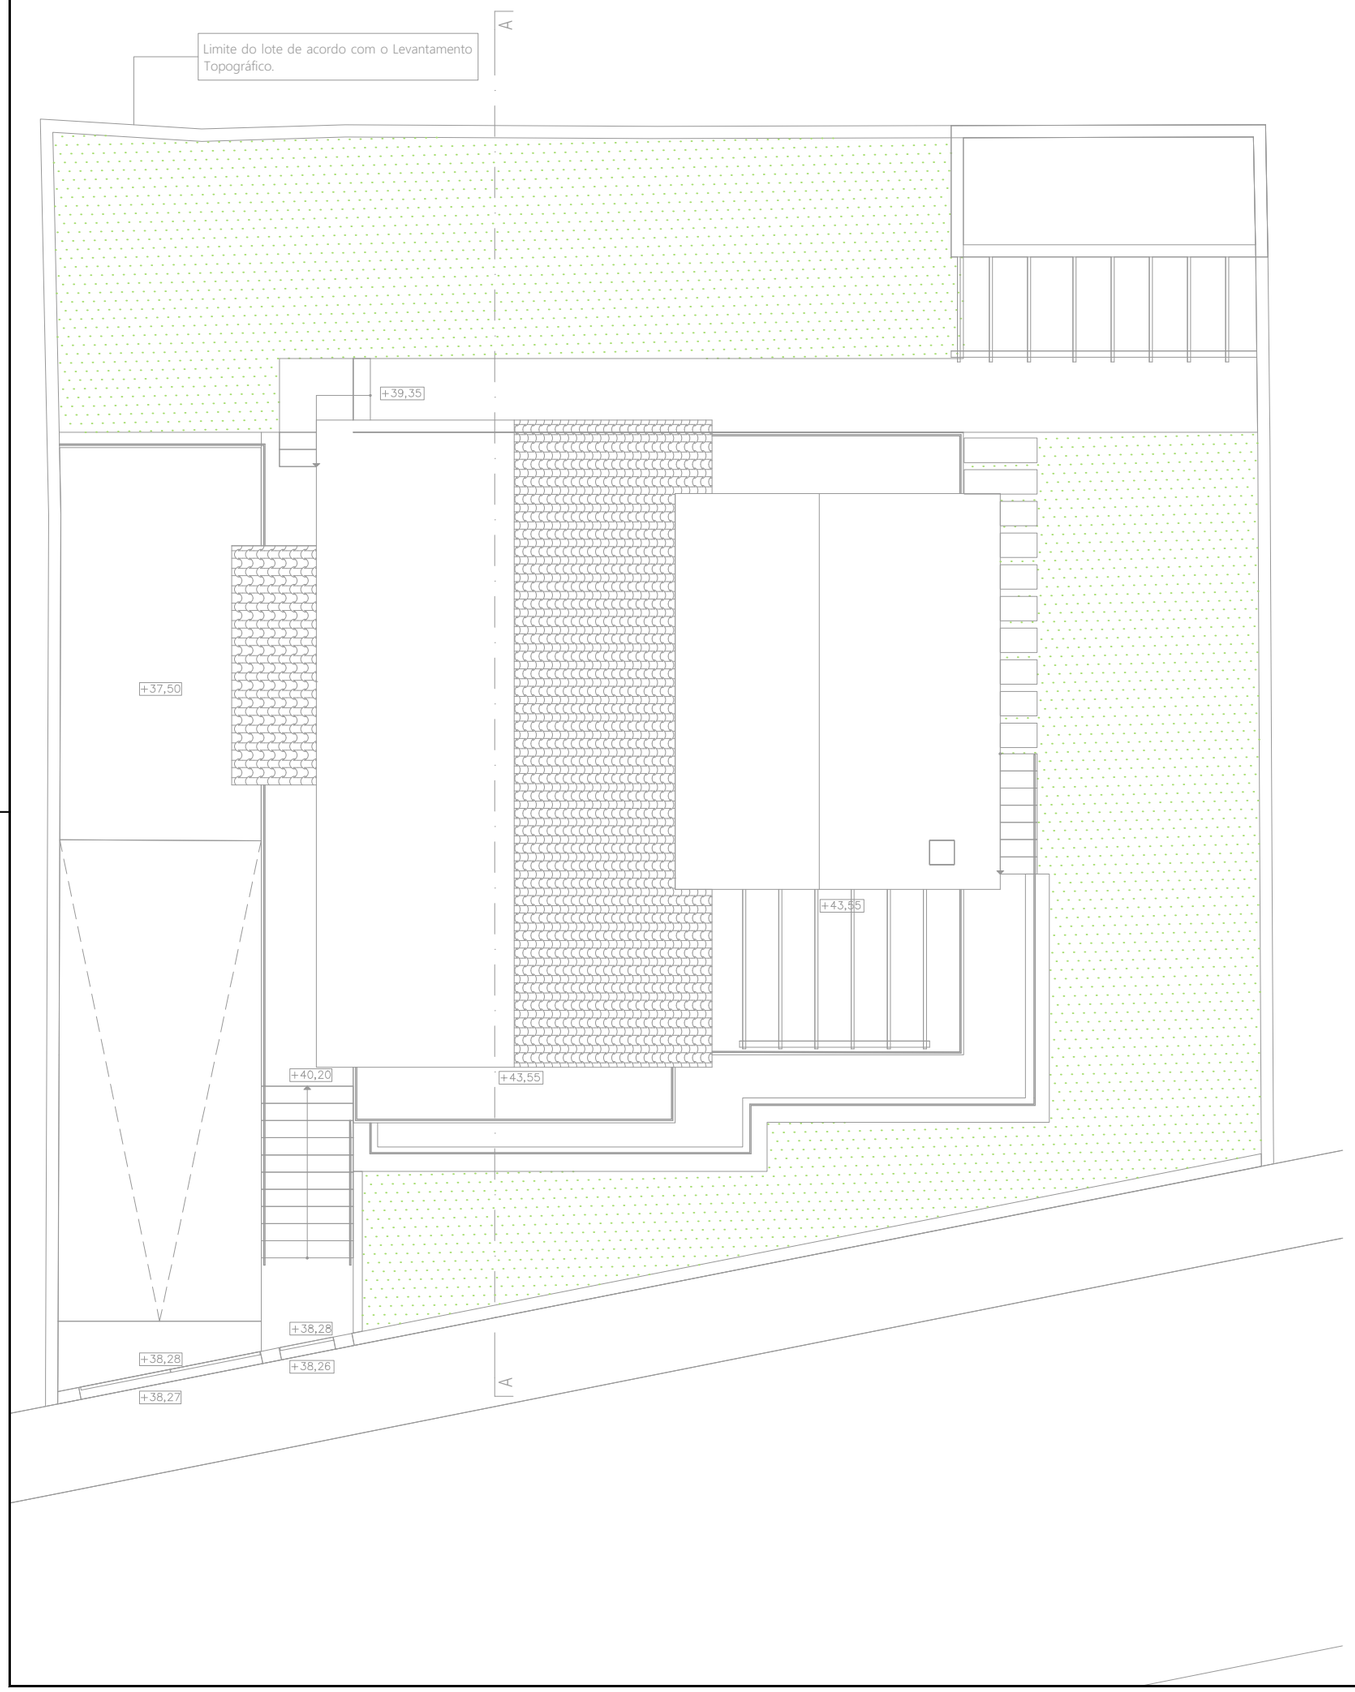

RAMAIS INDIVIDUAIS

APARELHOS	ÁGUA FRIA	ÁGUA QUENTE	DN EXT.
QUARTO DE BANHO			
- Lavatório	◦	◦	16
- Bidet	◦	◦	16
- Autoclismo	◦		16
- Banheira	◦	◦	20
- Duche	◦	◦	16
COZINHA / LAVANDARIA			
- Pia lava loiça	◦	◦	20
- M. lavar loiça	◦		16
- M. lavar roupa	◦		20

SIMBOLOGIA (REDE DE ÁGUAS):

	Canalização de água fria
	Canalização de água quente
	Canalização de água quente de retorno
	Canalização de água fria - Reutilização de águas pluviais
	Circuito fechado do fluído solar
	Contador
	Xadrêz
	Olho de boi
	Caixa de transição de material
	Boca de Incêndio exterior
BC	Bomba de Calor
	Torneira de serviço
	Torneira ou válvula de seccionamento
	Válvula de flutuador
	Válvula de Balanceamento
	Torneira misturadora
	Válvula de retenção
	Bomba circuladora para sistema de retorno de AQS
	Prumadas ascendentes com mudança de piso
	Prumadas descendentes com mudança de piso

MATERIAIS:

- Tubagens exteriores são em PEAD e desenvolvem-se pelo pavimento, com exceção das indicadas.
- Tubagens interiores são em Multicamada e desenvolvem-se pelas paredes e sobre tetos falsos, com exceção das indicadas.

GAPLR
ENGENHARIA LDA
Telem.: 967 068 588 | fax: 219 863 894 | GAPLRgeral@gmail.com

PROJETO
CONSTRUÇÃO DE MORADIA UNIFAMILIAR

ESPECIALIDADE
REDE DE AGUAS

DESIGNAÇÃO
PLANTA DA COBERTURA


REQUERENTE
Natasha Lara Santric

LOCAL
Praceta da Abadia, Lote 13
Ericeira
Mafra

DATA	PROCESSO	ESCALA
Julho 2026	3775	1/125

TÉCNICO
Eng.º Luis Reis
21981 O.E.

DESENHO N.º
05

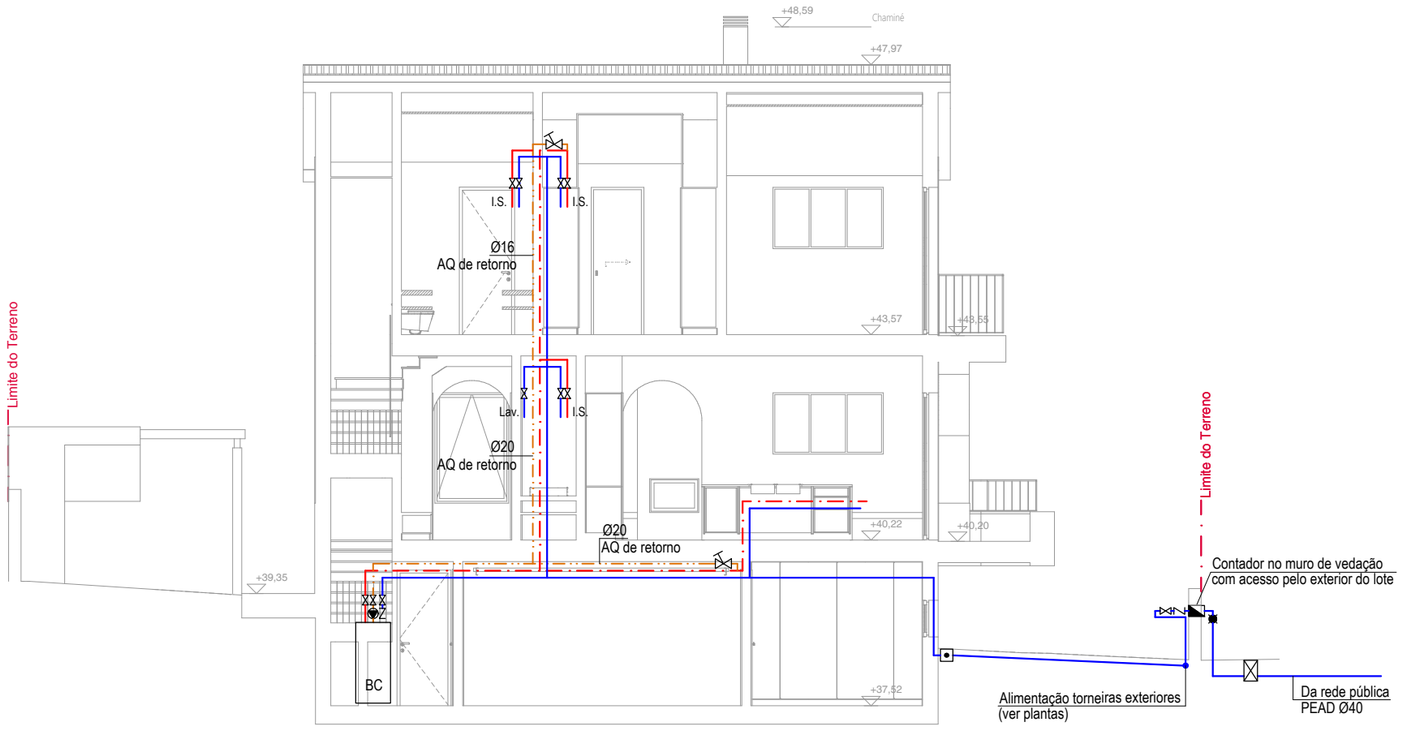

Corte A

RAMAIS INDIVIDUAIS

APARELHOS	ÁGUA FRIA	ÁGUA QUENTE	DN EXT.
QUARTO DE BANHO			
- Lavatório	°	°	16
- Bidet	°	°	16
- Autoclismo	°		16
- Banheira	°	°	20
- Duche	°	°	16
COZINHA / LAVANDARIA			
- Pia lava loiça	°	°	20
- M. lavar loiça	°		16
- M. lavar roupa	°		20

SIMBOLOGIA (REDE DE ÁGUAS):

	Canalização de água fria
	Canalização de água quente
	Canalização de água quente de retorno
	Canalização de água fria - Reutilização de águas pluviais
	Circuito fechado do fluído solar
	Contador
	Xadrêz
	Olho de boi
	Caixa de transição de material
	Boca de Incêndio exterior
BC	Bomba de Calor
	Torneira de serviço
	Torneira ou válvula de seccionamento
	Válvula de flutuador
	Válvula de Balanceamento
	Torneira misturadora
	Válvula de retenção
	Bomba circuladora para sistema de retorno de AQS
	Prumadas ascendentes com mudança de piso
	Prumadas descendentes com mudança de piso

MATERIAIS:

- Tubagens exteriores são em PEAD e desenvolvem-se pelo pavimento, com exceção das indicadas.
- Tubagens interiores são em Multicamada e desenvolvem-se pelas paredes e sobre tetos falsos, com exceção das indicadas.

GAP LR
ENGENHARIA LDA

Telem.: 967 068 588 | fax: 219 863 894 | GAPLRgeral@gmail.com

PROJETO

CONSTRUÇÃO DE MORADIA UNIFAMILIAR

ESPECIALIDADE

REDE DE AGUAS

DESIGNAÇÃO

CORTE A (Esquemático)

REQUERENTE

Natasha Lara Santric

LOCAL

Praceta da Abadia, Lote 13
Ericeira
Mafra

DATA	PROCESSO	ESCALA
Julho 2026	3775	1/125


TÉCNICO

Eng.º Luis Reis
21981 O.E.


DESENHO N.º

06


POSICIONAMENTO TIPO DA REDE INTERIOR DE UMA INSTALAÇÃO SANITÁRIA
(Esc: s/ escala)

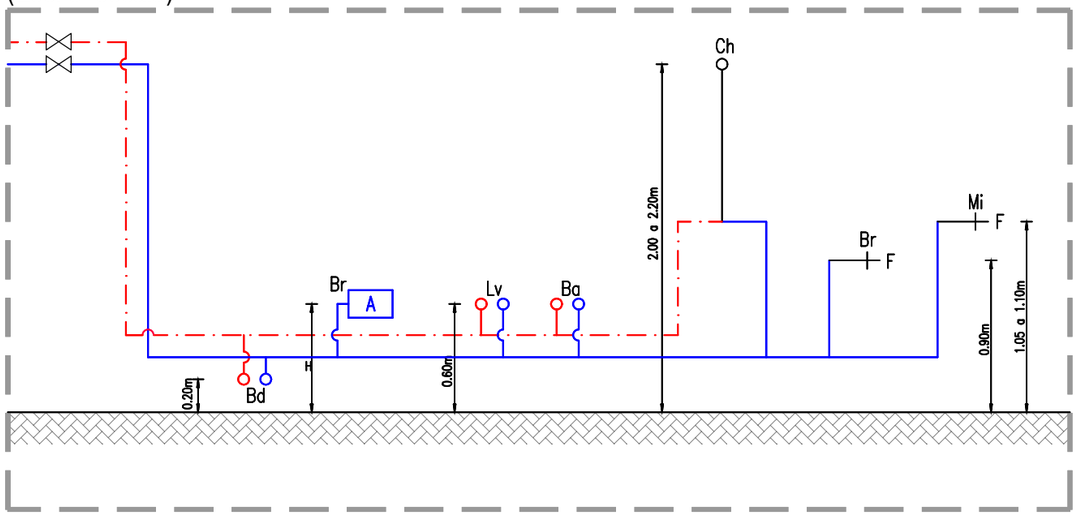


PORMENOR CAIXA DE TRANSIÇÃO DE MATERIAL
S/ESCALA

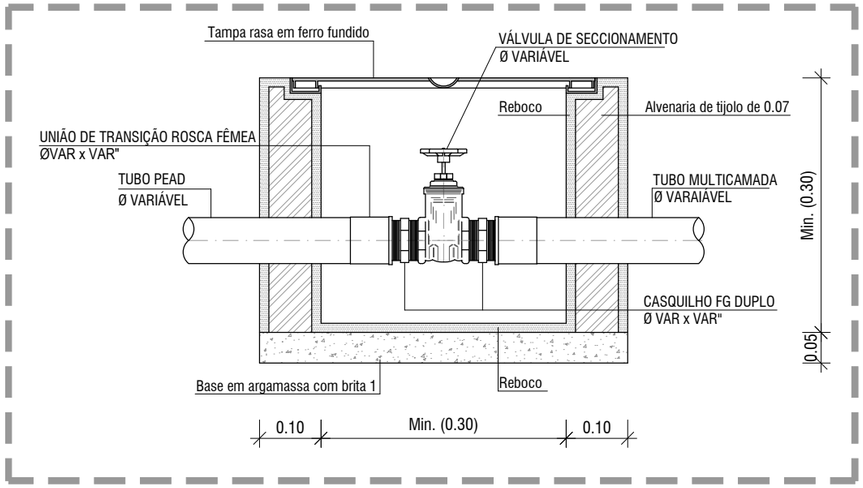

INSTALAÇÃO DE TUBAGENS À VISTA EM PARALELO
(Esc: s/ escala)

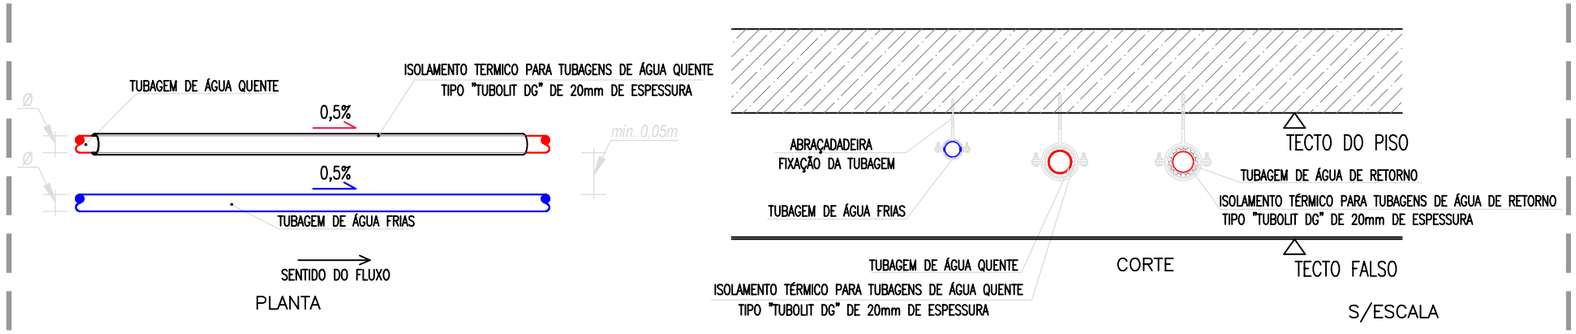

ESQUEMA DE FUNCIONAMENTO DA INSTALAÇÃO SOLAR
S/Escala

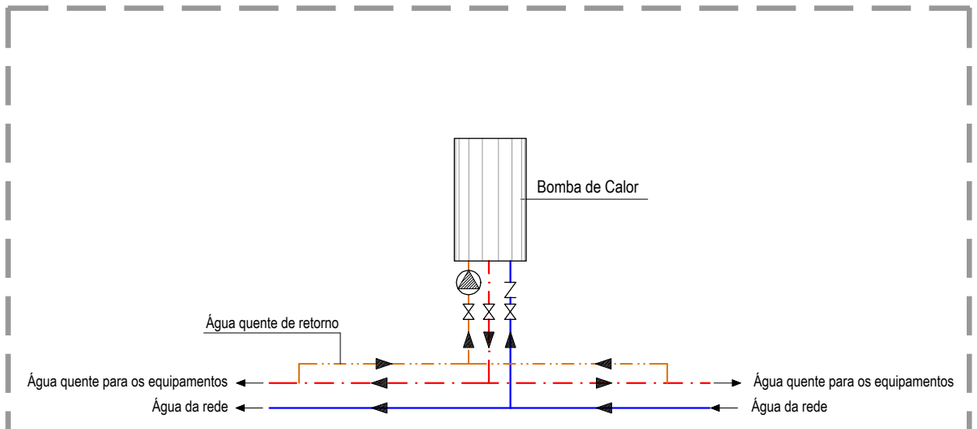

NOTAS GERAIS

- Todos os diâmetros indicados, são nominais e em milimetros;
- Antes da execução dos trabalhos a que se referem estas peças desenhadas, deverão estas ser criteriosamente observadas em conjunto com todos os projectos de especialidades verificando todas as implicações e incidências entre elas;
- Qualquer alteração ou substituição de materiais ou de soluções, deverão ter a aprovação dos autor do projecto e da fiscalização da obra;
- Todos os traçados e localização de equipamentos, deverão ser confirmados sobre os desenhos do Projecto de Arquitectura ou nas reuniões de coordenação de obra com a presença do coordenador de todos os projectos;
- Durante a execução da obra é obrigatório proceder aos ensaios previstos no regulamento geral dos sistemas públicos e prediais de distribuição de água e de drenagem de águas residuais - Decreto Regulamentar n.º 23/95, de 23 de agosto.
- Todas as peças desenhadas e escritas terão que ser obrigatóriamente confrontados e compatibilizados com a realidade da obra, IN SITU.

GAPLR
ENGENHARIA LDA
Telem.: 967 068 588 | fax: 219 863 894 | GAPLRgeral@gmail.com

PROJETO
CONSTRUÇÃO DE MORADIA UNIFAMILIAR

ESPECIALIDADE
REDE DE AGUAS

DESIGNAÇÃO
CORTES (Esquemáticos)

REQUERENTE
Natasha Lara Santric

LOCAL
Praceta da Abadia, Lote 13
Ericeira
Mafra

DATA	PROCESSO	ESCALA
Julho 2026	3775	1/125

TÉCNICO	DESENHO N.º
Eng.º Luis Reis 21981 O.E.	**07**