ÍNDICE DE PEÇAS DESENHADAS

DESENHO Nº	DESCRIÇÃO	ESCALA
00	Índice de Desenhos	S/E
01	Planta do Piso -1; Ventilação	1/100
02	Planta do Piso 0; Ventilação	1/100
03	Planta do Piso 1; Ventilação	1/100
04	Pormenores; Ventilação	S/E
01	Planta do Piso -1; Climatização	1/100
02	Planta do Piso 0; Climatização	1/100
03	Planta do Piso 1; Climatização	1/100

GAPLR
ENGENHARIA LDA
Telem.: 967 068 588 | fax: 219 863 894 | GAPLRgeral@gmail.com

PROJETO
CONSTRUÇÃO DE HABITAÇÃO UNIFAMILIAR

ESPECIALIDADE
AVAC

DESIGNAÇÃO
ÍNDICE DE DESENHOS

REQUERENTE
Natasha Lara Santric

LOCAL
Praceta da Abadia, Lote 13
Ericeira, Mafra

DATA	PROCESSO	ESCALA
Julho 2026	3775	S/E

TÉCNICO
Eng.º Téc. Pedro Batalha
29740 O.E.T.

DESENHO N.º
00


A4 (297x210mm)

NOTAS GERAIS - TUBAGEM

- Ligações entre o VMC e os plenos de distribuição feitas em conduta com flexivel com isolamento térmico e acústico.
- Ligações entre os plenos de distribuição e os difusores feitas em conduta semirrígida de PEAD.

SIMBOLOGIA (AVAC):

	Conduta exaustão
	Conduta insuflação
	Prumada de conduta de exaustão
	Recuperador de calor a biomassa/lenha
	Difusor de insuflação
	Difusor de extração
	Exaustor
	Bomba de calor compacta
	Ventilador mecânico de duplo fluxo com recuperador de calor
PD	Pleno de distribuição

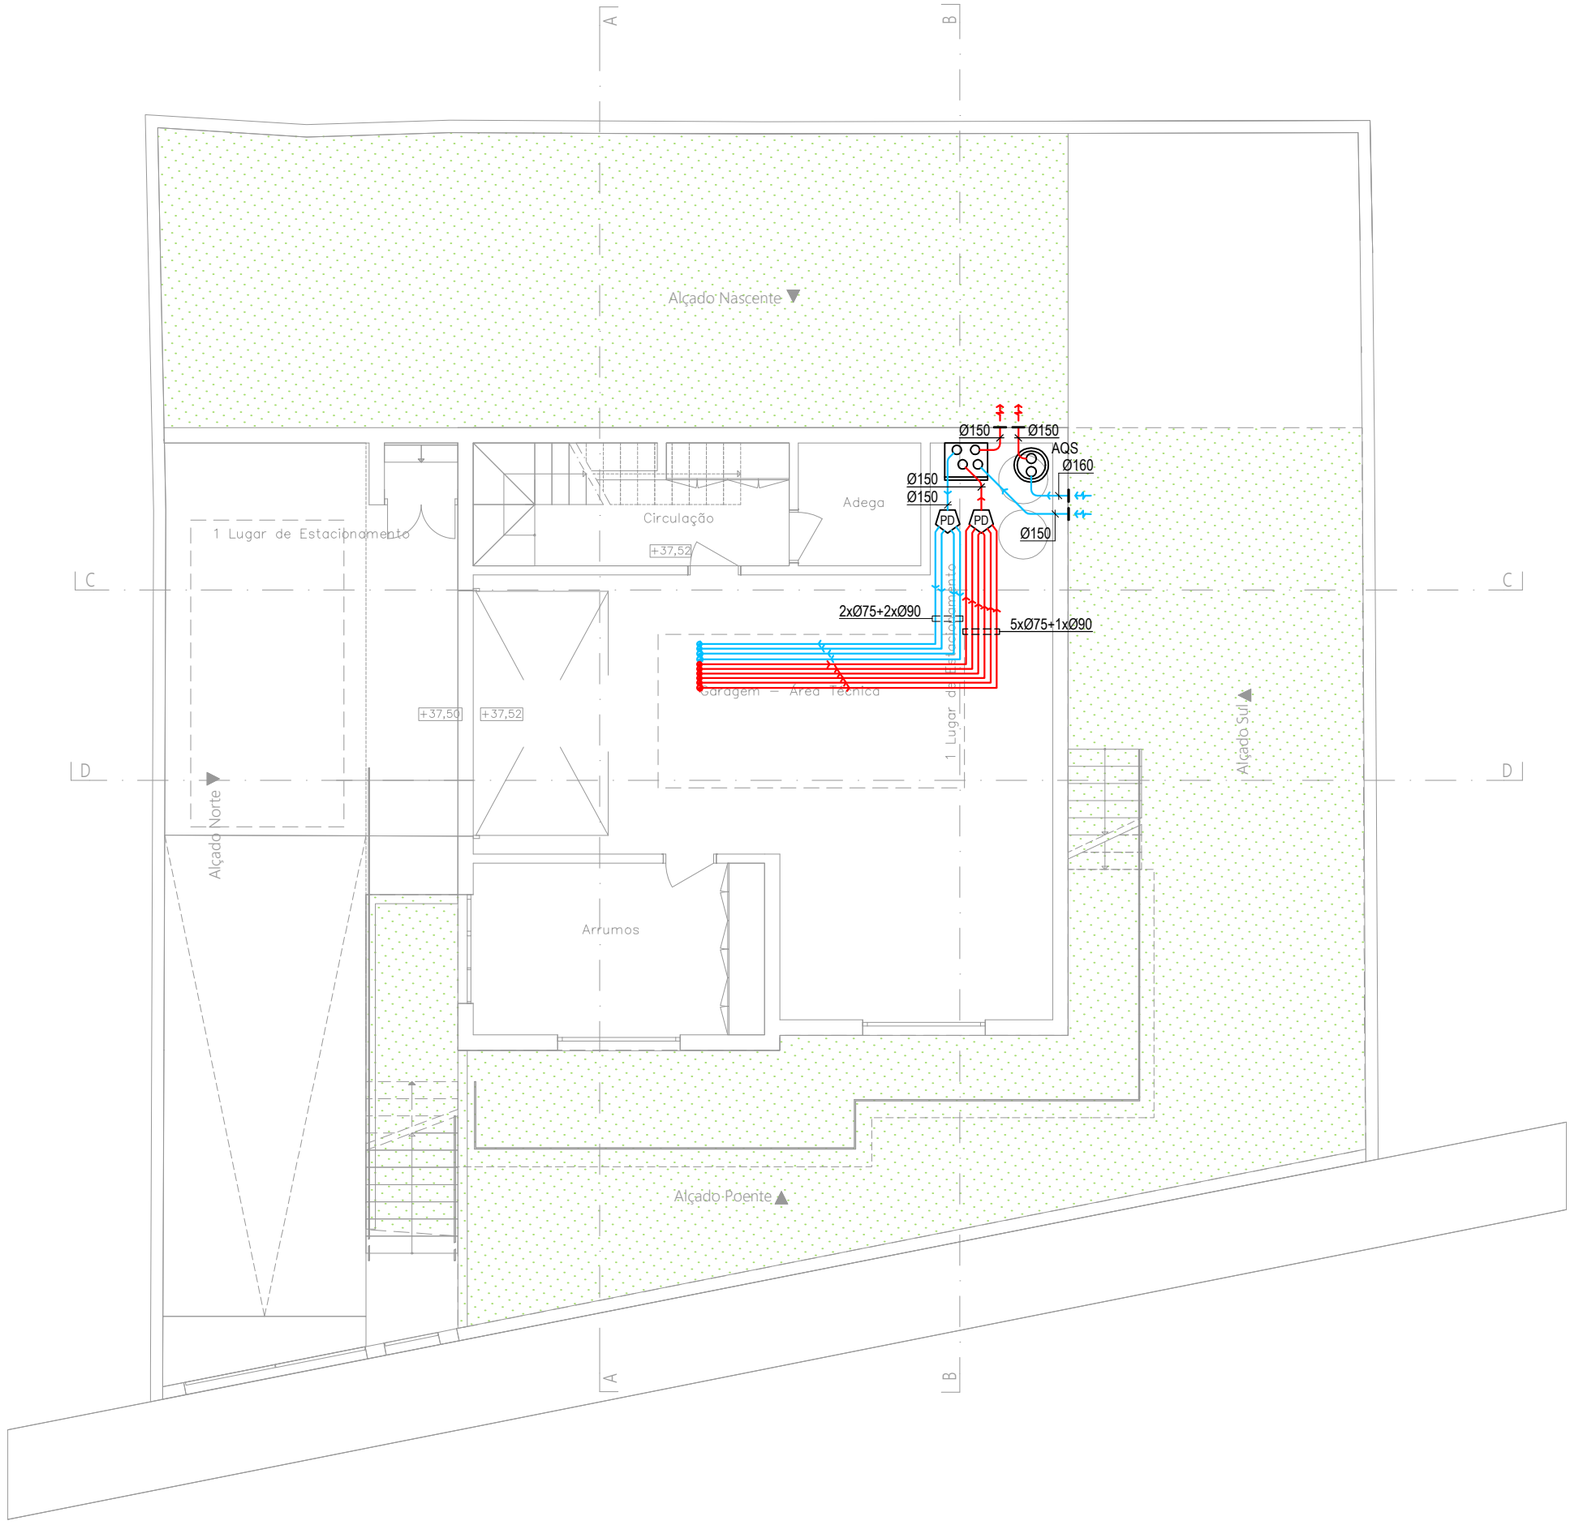

GAPLR
ENGENHARIA LDA

Telem.: 967 068 588 | fax: 219 863 894 | GAPLRgeral@gmail.com

PROJETO
CONSTRUÇÃO DE HABITAÇÃO UNIFAMILIAR

ESPECIALIDADE
AVAC

DESIGNAÇÃO
PLANTA DO PISO -1 VENTILAÇÃO

REQUERENTE
Natasha Lara Santric

LOCAL
Praceta da Abadia, Lote 13
Ericeira, Mafra

DATA	PROCESSO	ESCALA
Julho 2026	3775	1/100

TÉCNICO
Eng.º Téc. Pedro Batalha
29740 O.E.T.

DESENHO N.º
01


A3 (297x420mm)

NOTAS GERAIS - TUBAGEM

- Ligações entre o VMC e os plenos de distribuição feitas em conduta com flexivel com isolamento térmico e acústico.
- Ligações entre os plenos de distribuição e os difusores feitas em conduta semirrígida de PEAD.

SIMBOLOGIA (AVAC):

	Conduta exaustão
	Conduta insuflação
	Prumada de conduta de exaustão
	Recuperador de calor a biomassa/lenha
	Difusor de insuflação
	Difusor de extração
	Exaustor
	Bomba de calor compacta
	Ventilador mecânico de duplo fluxo com recuperador de calor
PD	Pleno de distribuição

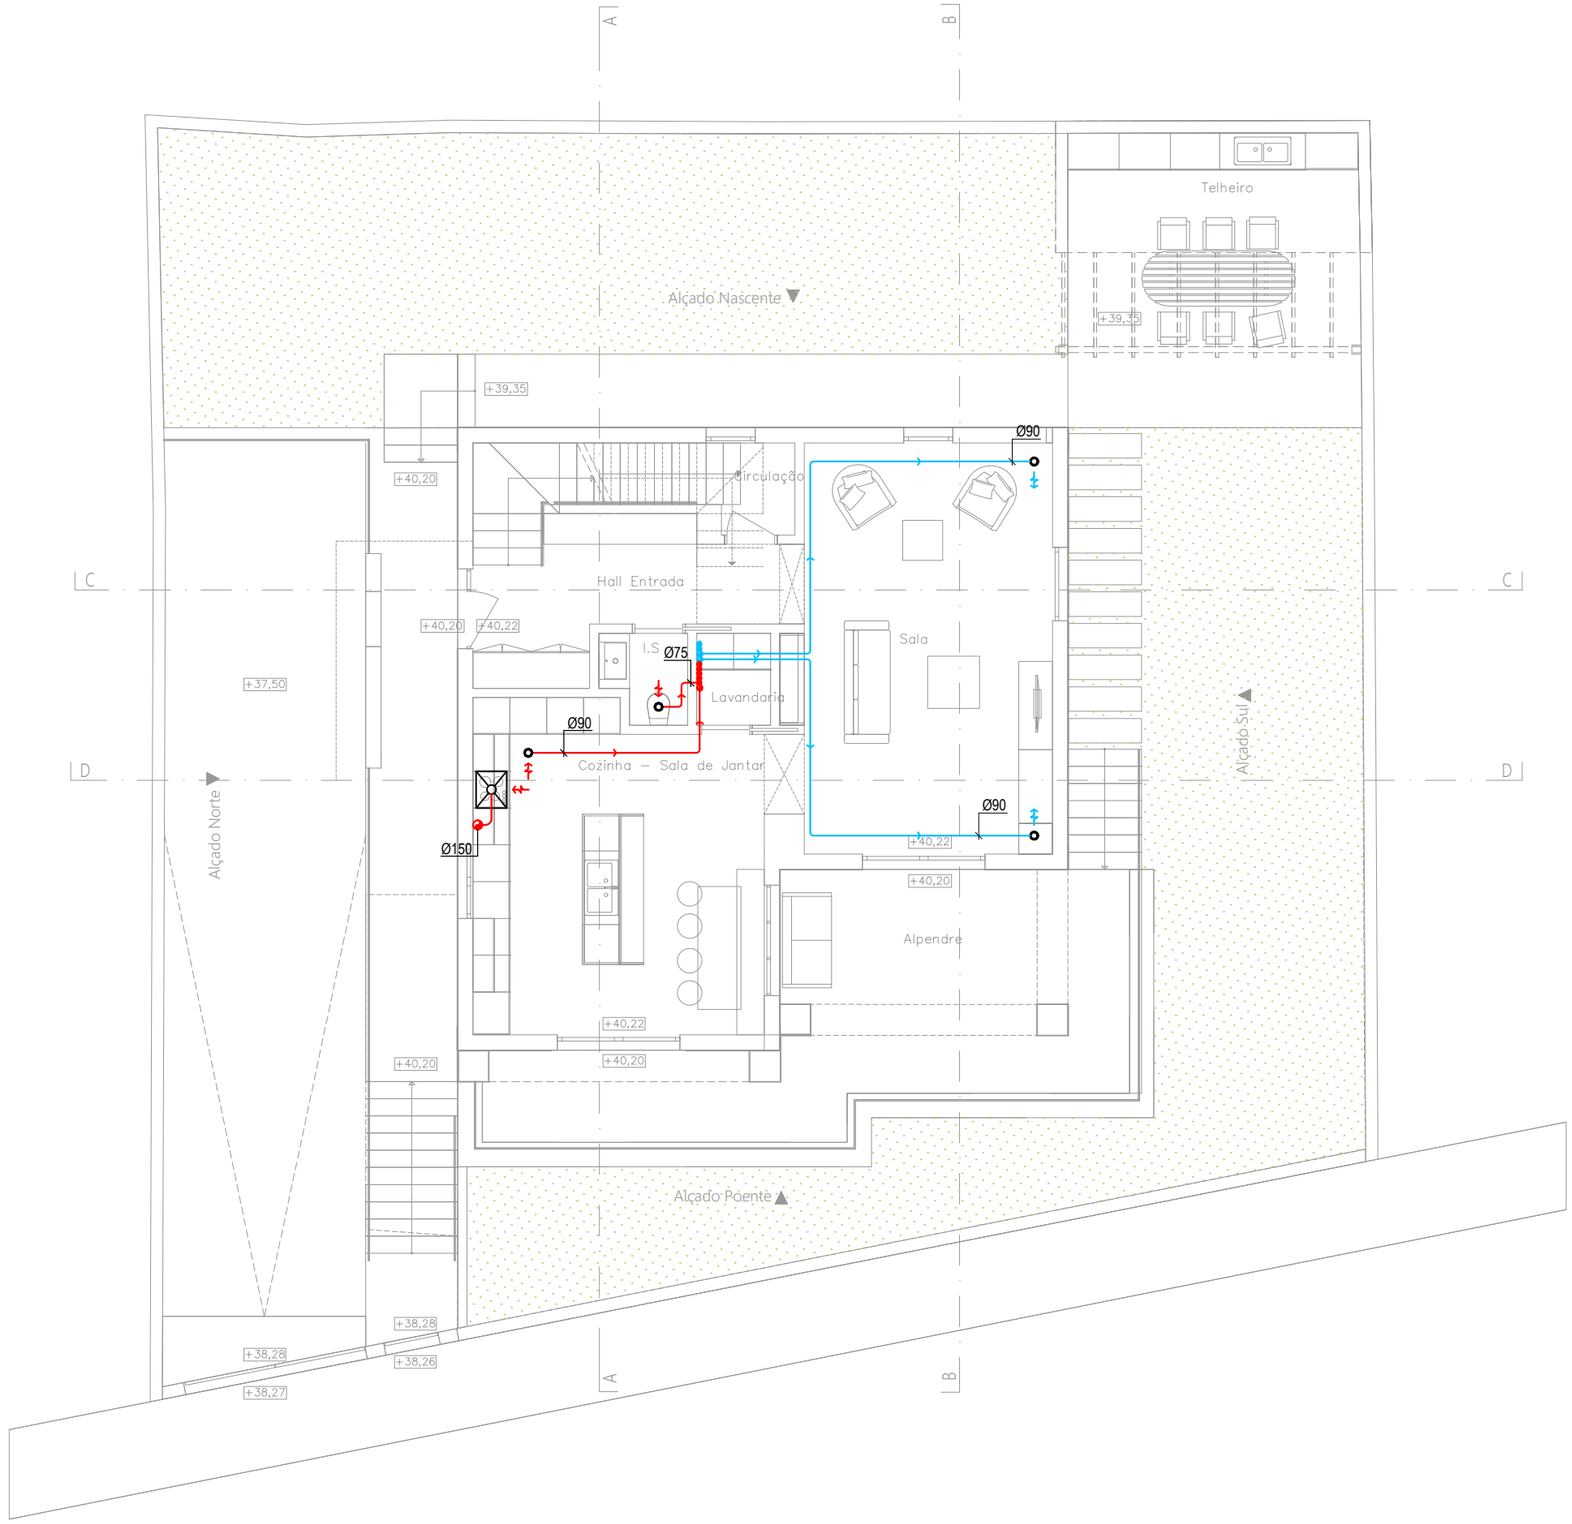

GAPLR ENGENHARIA LDA

Telem.: 967 068 588 | fax: 219 863 894 | GAPLRgeral@gmail.com

PROJETO

CONSTRUÇÃO DE HABITAÇÃO UNIFAMILIAR

ESPECIALIDADE

AVAC

DESIGNAÇÃO

PLANTA DO PISO 0 VENTILAÇÃO

REQUERENTE

Natasha Lara Santric

LOCAL

Praceta da Abadia, Lote 13
Ericeira, Mafra

DATA	PROCESSO	ESCALA
Julho 2026	3775	1/100

TÉCNICO

Eng.º Téc. Pedro Batalha
29740 O.E.T.

DESENHO N.º

02


A3 (297x420mm)

NOTAS GERAIS - TUBAGEM

- Ligações entre o VMC e os plenos de distribuição feitas em conduta com flexivel com isolamento térmico e acústico.
- Ligações entre os plenos de distribuição e os difusores feitas em conduta semirrígida de PEAD.

SIMBOLOGIA (AVAC):

	Conduta exaustão
	Conduta insuflação
	Prumada de conduta de exaustão
	Recuperador de calor a biomassa/lenha
	Difusor de insuflação
	Difusor de extração
	Exaustor
	Bomba de calor compacta
	Ventilador mecânico de duplo fluxo com recuperador de calor
PD	Pleno de distribuição

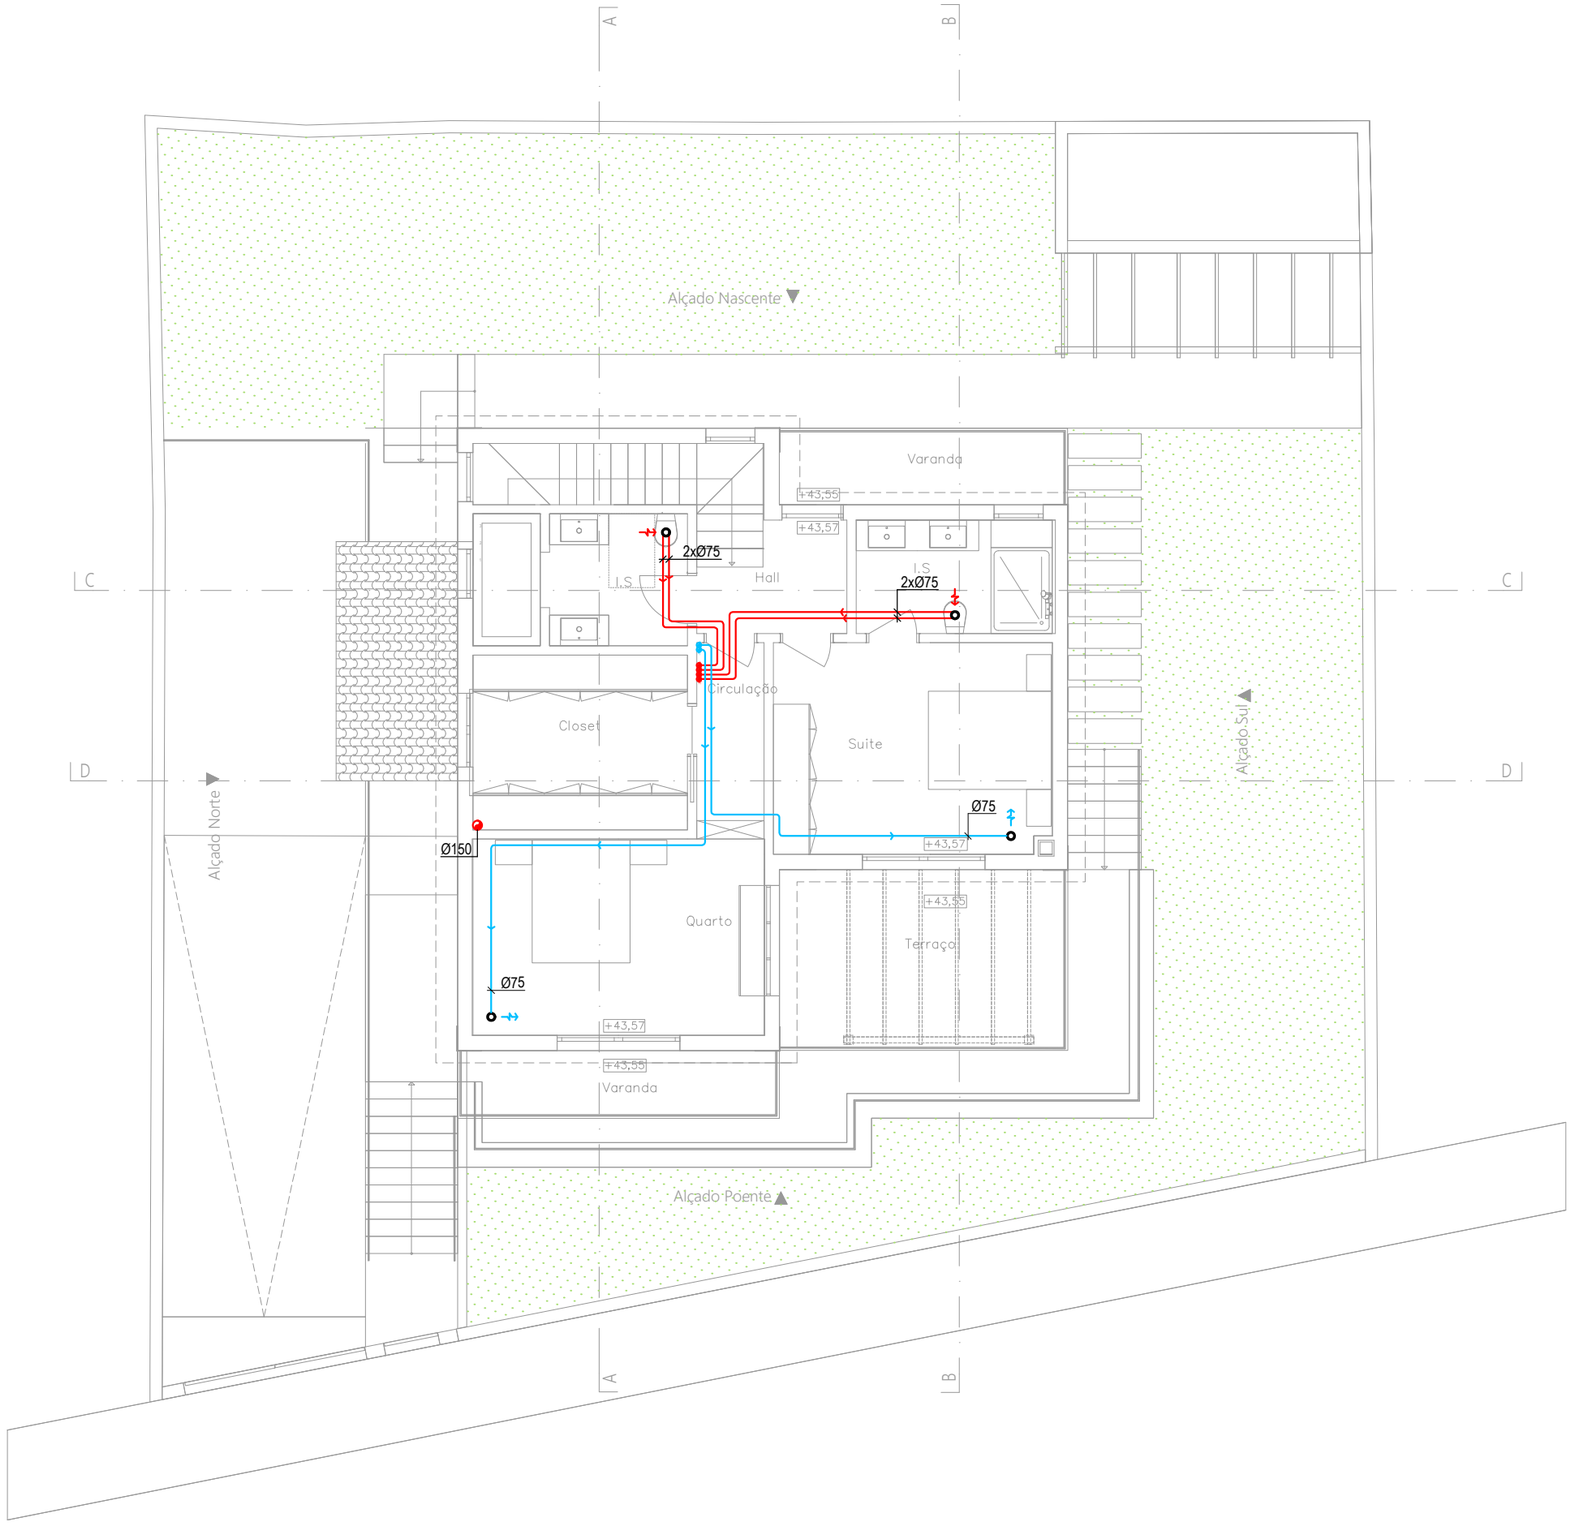

GAPLR ENGENHARIA LDA

Telem.: 967 068 588 | fax: 219 863 894 | GAPLRgeral@gmail.com

PROJETO

CONSTRUÇÃO DE HABITAÇÃO UNIFAMILIAR

ESPECIALIDADE

AVAC

DESIGNAÇÃO

PLANTA DO PISO 1 VENTILAÇÃO

REQUERENTE

Natasha Lara Santric

LOCAL


Praceta da Abadia, Lote 13
Ericeira, Mafra

DATA	PROCESSO	ESCALA
Julho 2026	3775	1/100

TÉCNICO	DESENHO N.º
Eng.º Téc. Pedro Batalha 29740 O.E.T.	**03**

A3 (297x420mm)

PORMENOR EXAUSTOR DE COZINHA

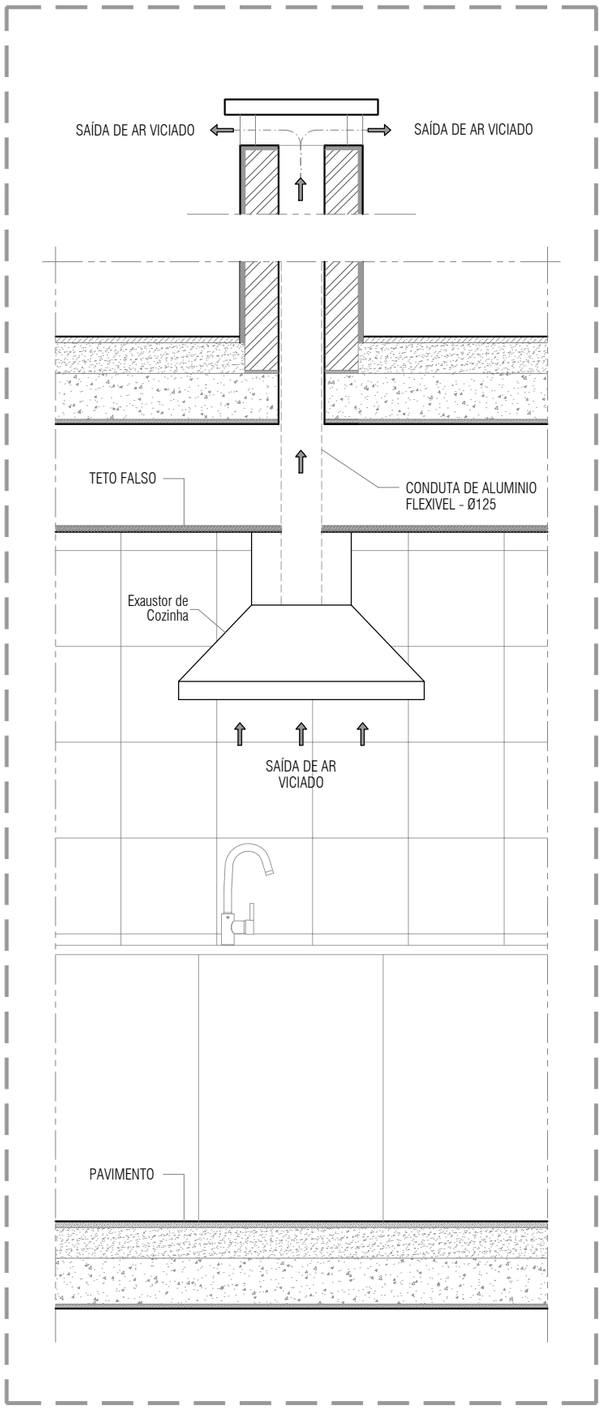

A3 (297x420mm)

GAPLR
ENGENHARIA LDA

Telem.: 967 068 588 | fax: 219 863 894 | GAPLRgeral@gmail.com

PROJETO
CONSTRUÇÃO DE HABITAÇÃO UNIFAMILIAR

ESPECIALIDADE
AVAC

DESIGNAÇÃO
PORMENORES VENTILAÇÃO

REQUERENTE
Natasha Lara Santric

LOCAL
Praceta da Abadia, Lote 13
Ericeira, Mafra

DATA	PROCESSO	ESCALA
Julho 2026	3775	S/E

TÉCNICO	DESENHO N.º
Eng.º Téc. Pedro Batalha 29740 O.E.T.	**04**

NOTAS GERAIS - TUBAGEM


- Sistemas de Expansão Direta: Tubagem em cobre, própria para o fluido frigorigéneo dos sistemas instalados, isolada termicamente e com caraterísticas de acordo com especificações dos fabricantes das unidades de climatização/refrigeração.
- Tubagem de fluido frigorigéneo embebida em paredes e, quando em teto falso, couretes ou no exterior será instalada sobre esteira.
- Tubagem de fluido frigorigéneo quando no exterior será instalada sobre esteira elevada e protegida com forra mecânica e/ou com esteira metálica opaca.
- Tubagem de condensados em PVC e com ligação sifonada aos esgotos "limpos" nos pontos indicados no Projeto de Esgotos; Traçado da rede de condensados a coordenar em obra de acordo com atravancamentos existentes.
- Tubagem de condensados isolada termicamente junto às unidades interiores de expansão direta e unidades de tratamento de ar num comprimento mínimo de 1 m.
- Tubagem de condensados com pendente mínima de 1%, sendo os traçados aferidos em obra e coordenados com a Empreitada de Esgotos.

SIMBOLOGIA (AVAC):

	Tubagem de fluido frigorigéneo - líquido + gás (mm)
	Tubagem de drenagem de condensados
•	Prumada de tubagem de fluido frigorigéneo
	Unidade Exterior - tipo multisplit
	Unidade Interior - tipo conduta
	Alçapão para manutenção

UNIDADES CLIMATIZAÇÃO

Designação	**Compartimento**	**Potência** (kW)	**Modelo Sugerido** (Midea)
UE1	---	5,98	M3OG-21HFN8-Q
UI1.1	Cozinha	3,05	MTJ-12HWFNX
UI1.2	Sala	2,93	MTJ-12HWFNX
UE2	---	4,25	M3OG-21HFN8-Q
UI2.1	Quarto	2,29	MTJ-09HWFNX
UI2.2	Suite	1,96	MTJ-09HWFNX

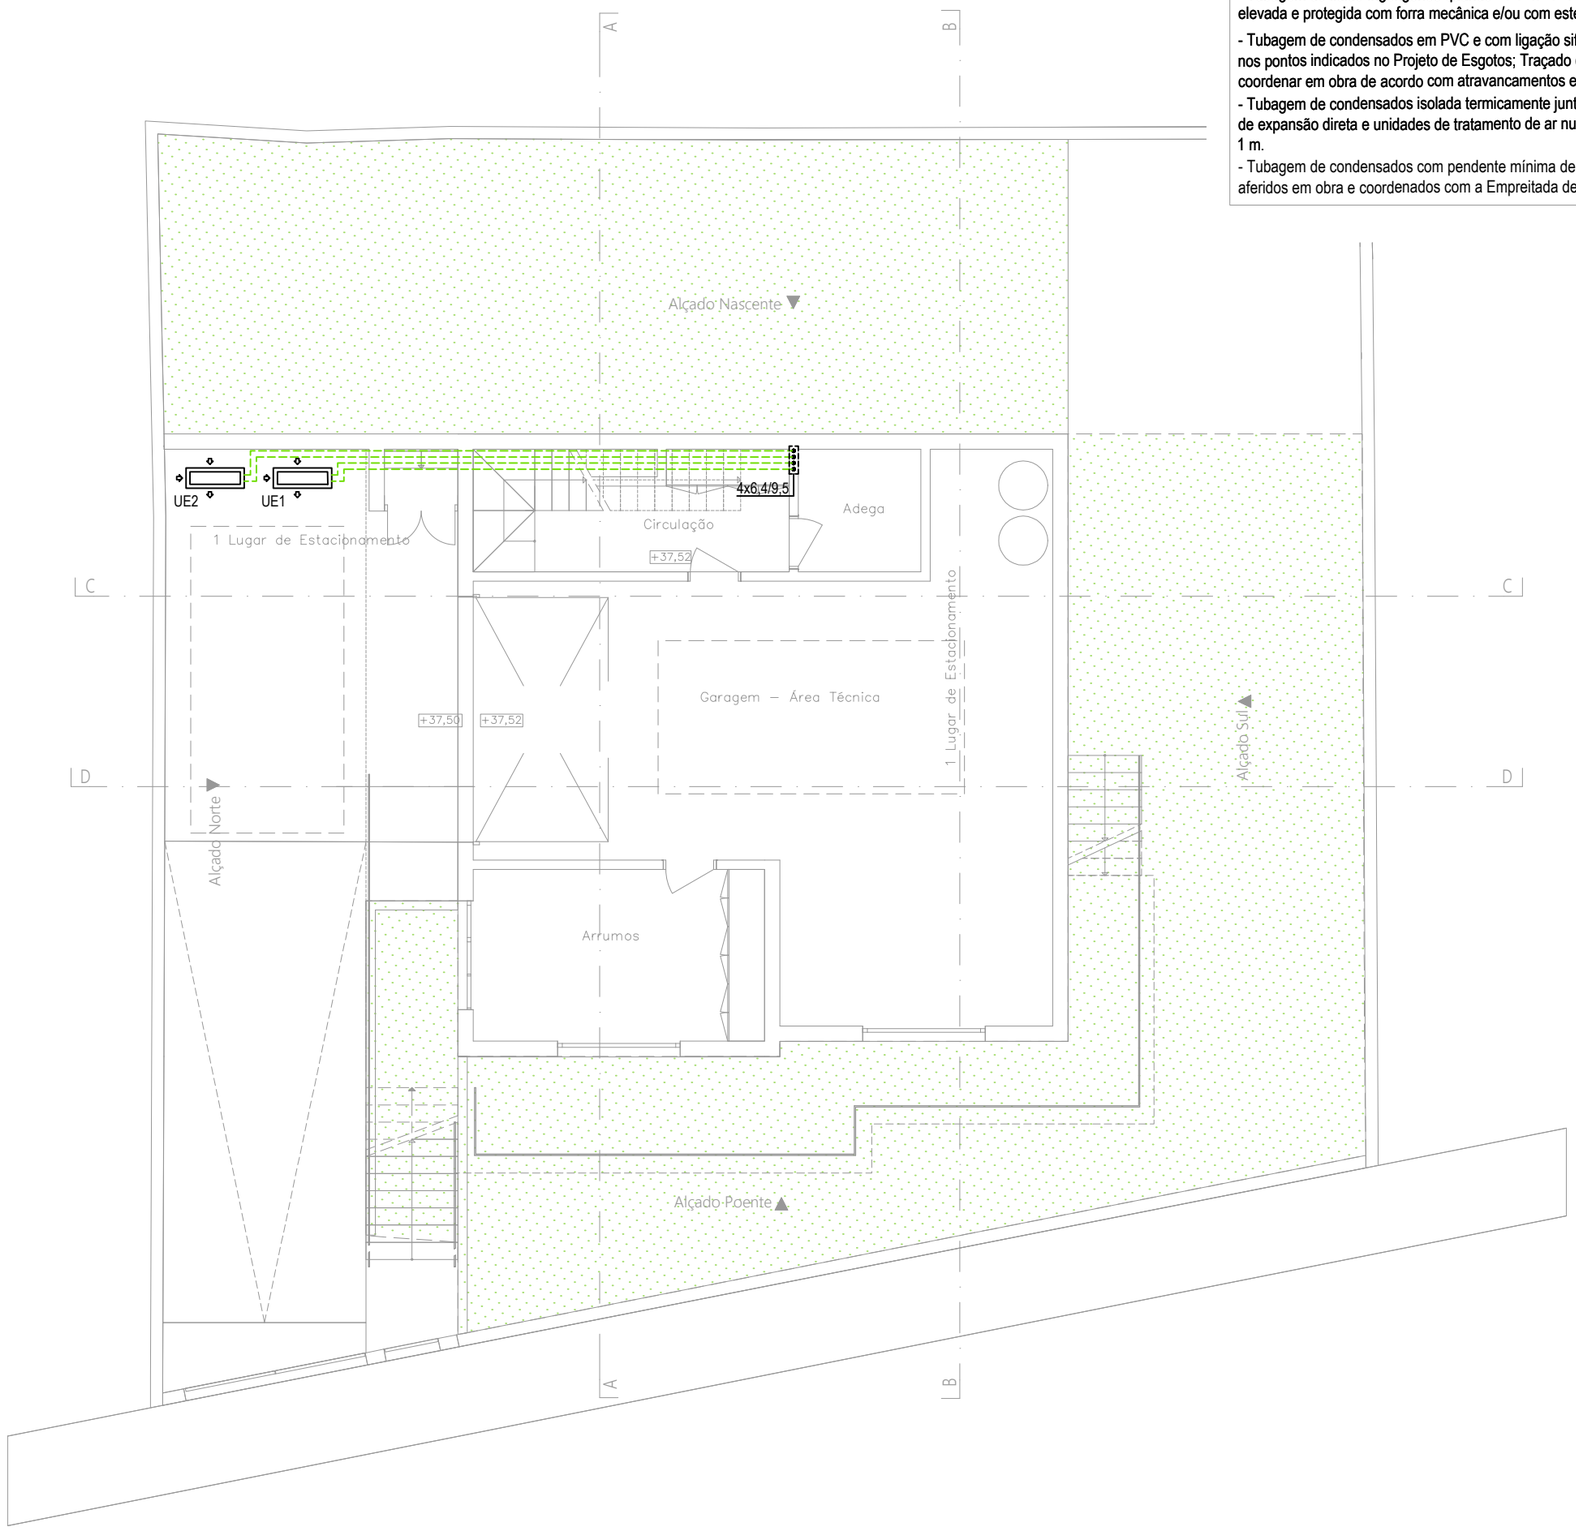

GAPLR ENGENHARIA LDA

Telem.: 967 068 588 | fax: 219 863 894 | GAPLRgeral@gmail.com

PROJETO

CONSTRUÇÃO DE HABITAÇÃO UNIFAMILIAR

ESPECIALIDADE

AVAC

DESIGNAÇÃO

PLANTA DO PISO -1 CLIMATIZAÇÃO

REQUERENTE

Natasha Lara Santric

LOCAL

Praceta da Abadia, Lote 13
Ericeira, Mafra

DATA	PROCESSO	ESCALA
Julho 2026	3775	1/100

TÉCNICO

Eng.º Téc. Pedro Batalha
29740 O.E.T.

DESENHO N.º

05

A3 (297x420mm)

NOTAS GERAIS - TUBAGEM


- Sistemas de Expansão Direta: Tubagem em cobre, própria para o fluido frigorigéneo dos sistemas instalados, isolada termicamente e com caraterísticas de acordo com especificações dos fabricantes das unidades de climatização/refrigeração.
- Tubagem de fluido frigorigéneo embebida em paredes e, quando em teto falso, couretes ou no exterior será instalada sobre esteira.
- Tubagem de fluido frigorigéneo quando no exterior será instalada sobre esteira elevada e protegida com forra mecânica e/ou com esteira metálica opaca.
- Tubagem de condensados em PVC e com ligação sifonada aos esgotos "limpos" nos pontos indicados no Projeto de Esgotos; Traçado da rede de condensados a coordenar em obra de acordo com atravancamentos existentes.
- Tubagem de condensados isolada termicamente junto às unidades interiores de expansão direta e unidades de tratamento de ar num comprimento mínimo de 1 m.
- Tubagem de condensados com pendente mínima de 1%, sendo os traçados aferidos em obra e coordenados com a Empreitada de Esgotos.

SIMBOLOGIA (AVAC):

	Tubagem de fluido frigorigéneo - líquido + gás (mm)
	Tubagem de drenagem de condensados
•	Prumada de tubagem de fluido frigorigéneo
	Unidade Exterior - tipo multisplit
	Unidade Interior - tipo conduta
	Alçapão para manutenção

UNIDADES CLIMATIZAÇÃO

Designação	**Compartimento**	**Potência** (kW)	**Modelo Sugerido** (Midea)
UE1	---	5,98	M3OG-21HFN8-Q
UI1.1	Cozinha	3,05	MTJ-12HWFNX
UI1.2	Sala	2,93	MTJ-12HWFNX
UE2	---	4,25	M3OG-21HFN8-Q
UI2.1	Quarto	2,29	MTJ-09HWFNX
UI2.2	Suite	1,96	MTJ-09HWFNX

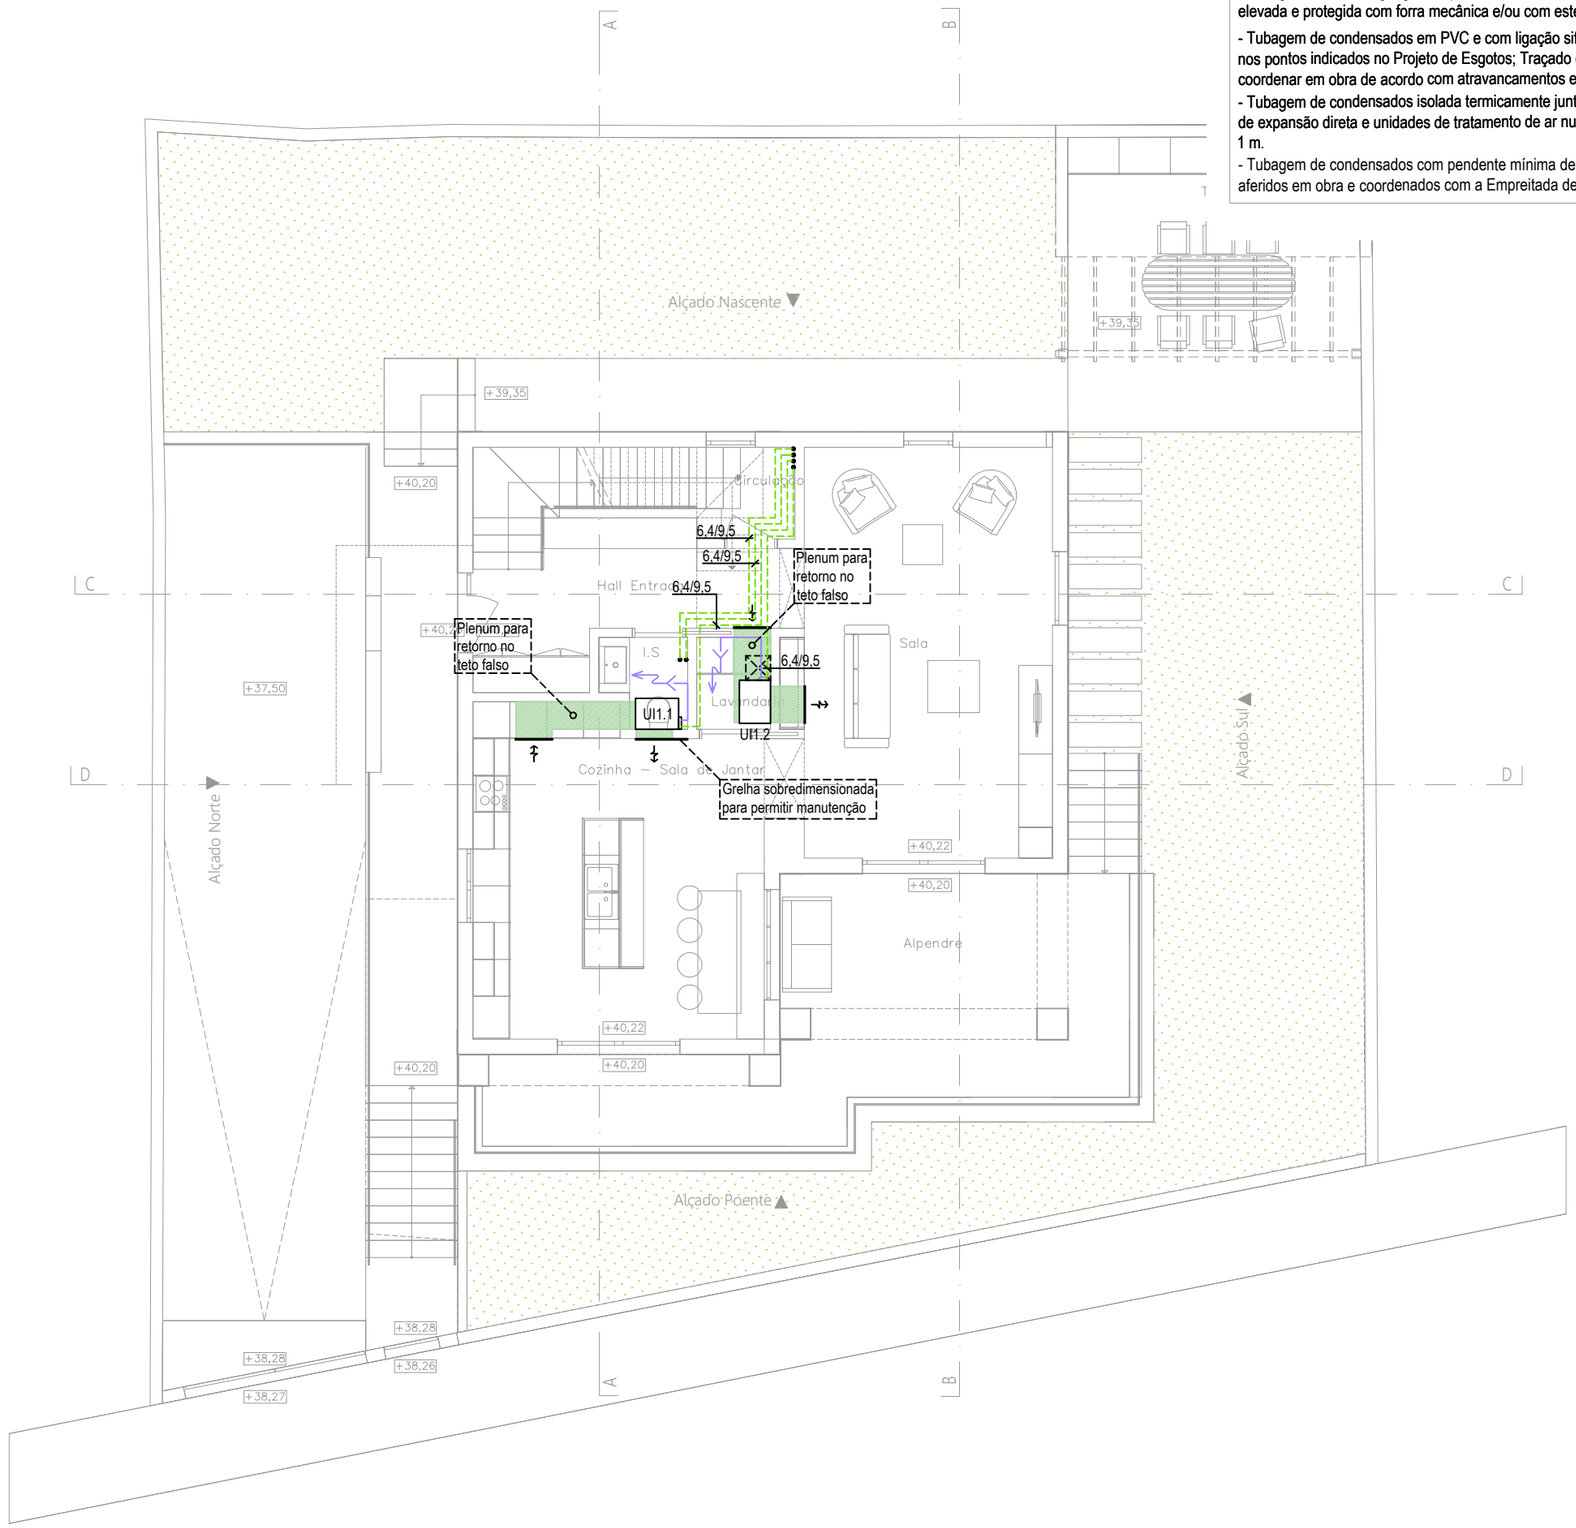

GAPLR ENGENHARIA LDA

Telem.: 967 068 588 | fax: 219 863 894 | GAPLRgeral@gmail.com

PROJETO

CONSTRUÇÃO DE HABITAÇÃO UNIFAMILIAR

ESPECIALIDADE

AVAC

DESIGNAÇÃO

PLANTA DO PISO 0 CLIMATIZAÇÃO

REQUERENTE

Natasha Lara Santric

LOCAL

Praceta da Abadia, Lote 13
Ericeira, Mafra

DATA	PROCESSO	ESCALA
Julho 2026	3775	1/100

TÉCNICO

Eng.º Téc. Pedro Batalha
29740 O.E.T.

DESENHO N.º

06


A3 (297x420mm)

NOTAS GERAIS - TUBAGEM

- Sistemas de Expansão Direta: Tubagem em cobre, própria para o fluido frigorigéneo dos sistemas instalados, isolada termicamente e com caraterísticas de acordo com especificações dos fabricantes das unidades de climatização/refrigeração.
- Tubagem de fluido frigorigéneo embebida em paredes e, quando em teto falso, couretes ou no exterior será instalada sobre esteira.
- Tubagem de fluido frigorigéneo quando no exterior será instalada sobre esteira elevada e protegida com forra mecânica e/ou com esteira metálica opaca.
- Tubagem de condensados em PVC e com ligação sifonada aos esgotos "limpos" nos pontos indicados no Projeto de Esgotos; Traçado da rede de condensados a coordenar em obra de acordo com atravancamentos existentes.
- Tubagem de condensados isolada termicamente junto às unidades interiores de expansão direta e unidades de tratamento de ar num comprimento mínimo de 1 m.
- Tubagem de condensados com pendente mínima de 1%, sendo os traçados aferidos em obra e coordenados com a Empreitada de Esgotos.

SIMBOLOGIA (AVAC):

	Tubagem de fluido frigorigéneo - líquido + gás (mm)
	Tubagem de drenagem de condensados
•	Prumada de tubagem de fluido frigorigéneo
	Unidade Exterior - tipo multisplit
	Unidade Interior - tipo conduta
	Alçapão para manutenção

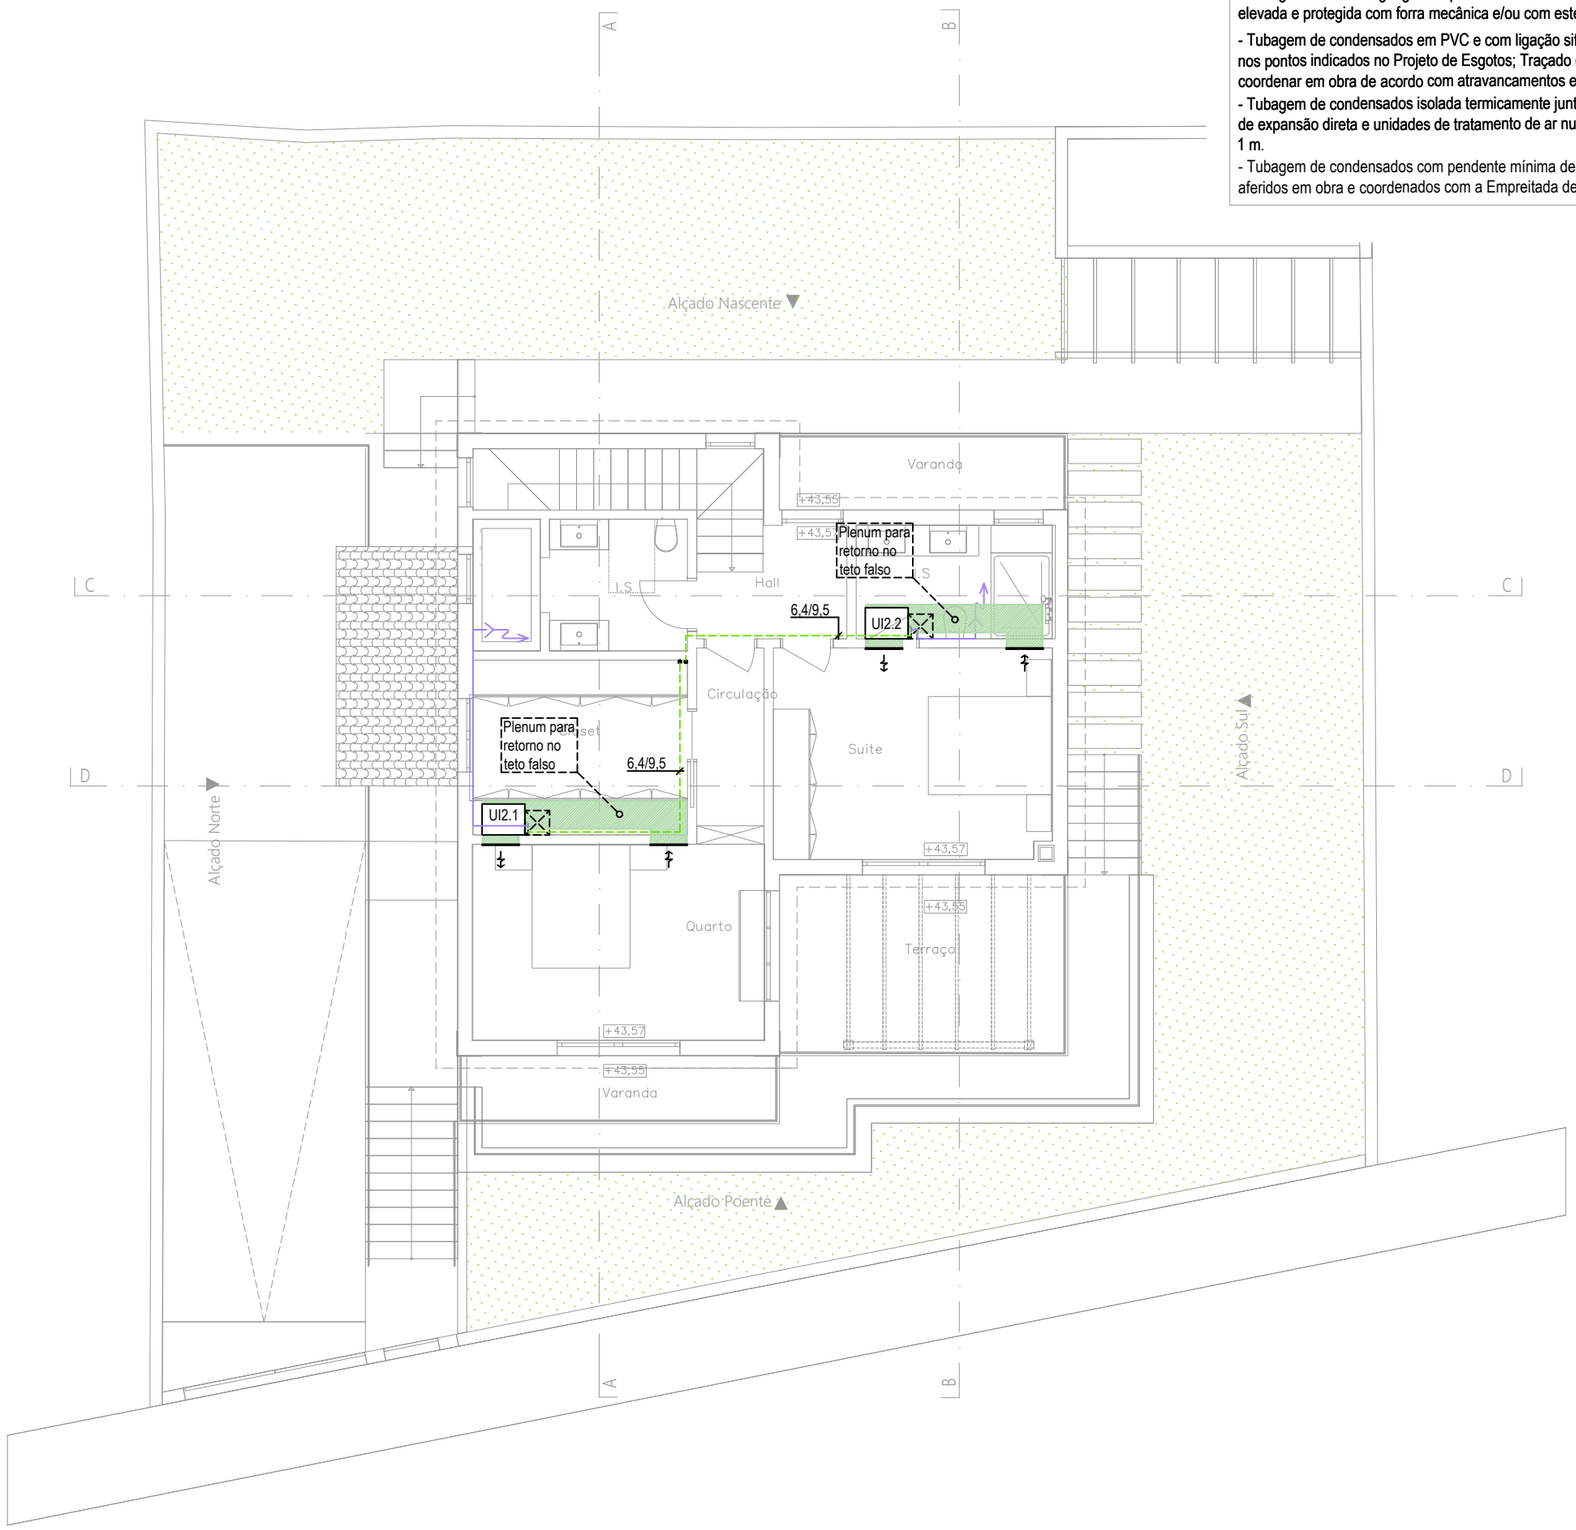

UNIDADES CLIMATIZAÇÃO

Designação	**Compartimento**	**Potência** (kW)	**Modelo Sugerido** (Midea)
UE1	---	5,98	M3OG-21HFN8-Q
UI1.1	Cozinha	3,05	MTJ-12HWFNX
UI1.2	Sala	2,93	MTJ-12HWFNX
UE2	---	4,25	M3OG-21HFN8-Q
UI2.1	Quarto	2,29	MTJ-09HWFNX
UI2.2	Suite	1,96	MTJ-09HWFNX

GAPLR ENGENHARIA LDA

Telem.: 967 068 588 | fax: 219 863 894 | GAPLRgeral@gmail.com

PROJETO

CONSTRUÇÃO DE HABITAÇÃO UNIFAMILIAR

ESPECIALIDADE

AVAC

DESIGNAÇÃO

PLANTA DO PISO 1 CLIMATIZAÇÃO

REQUERENTE

Natasha Lara Santric

LOCAL

Praceta da Abadia, Lote 13
Ericeira, Mafra

DATA	PROCESSO	ESCALA
Julho 2026	3775	1/100

TÉCNICO

Eng.º Téc. Pedro Batalha
29740 O.E.T.

DESENHO N.º

07

A3 (297x420mm)