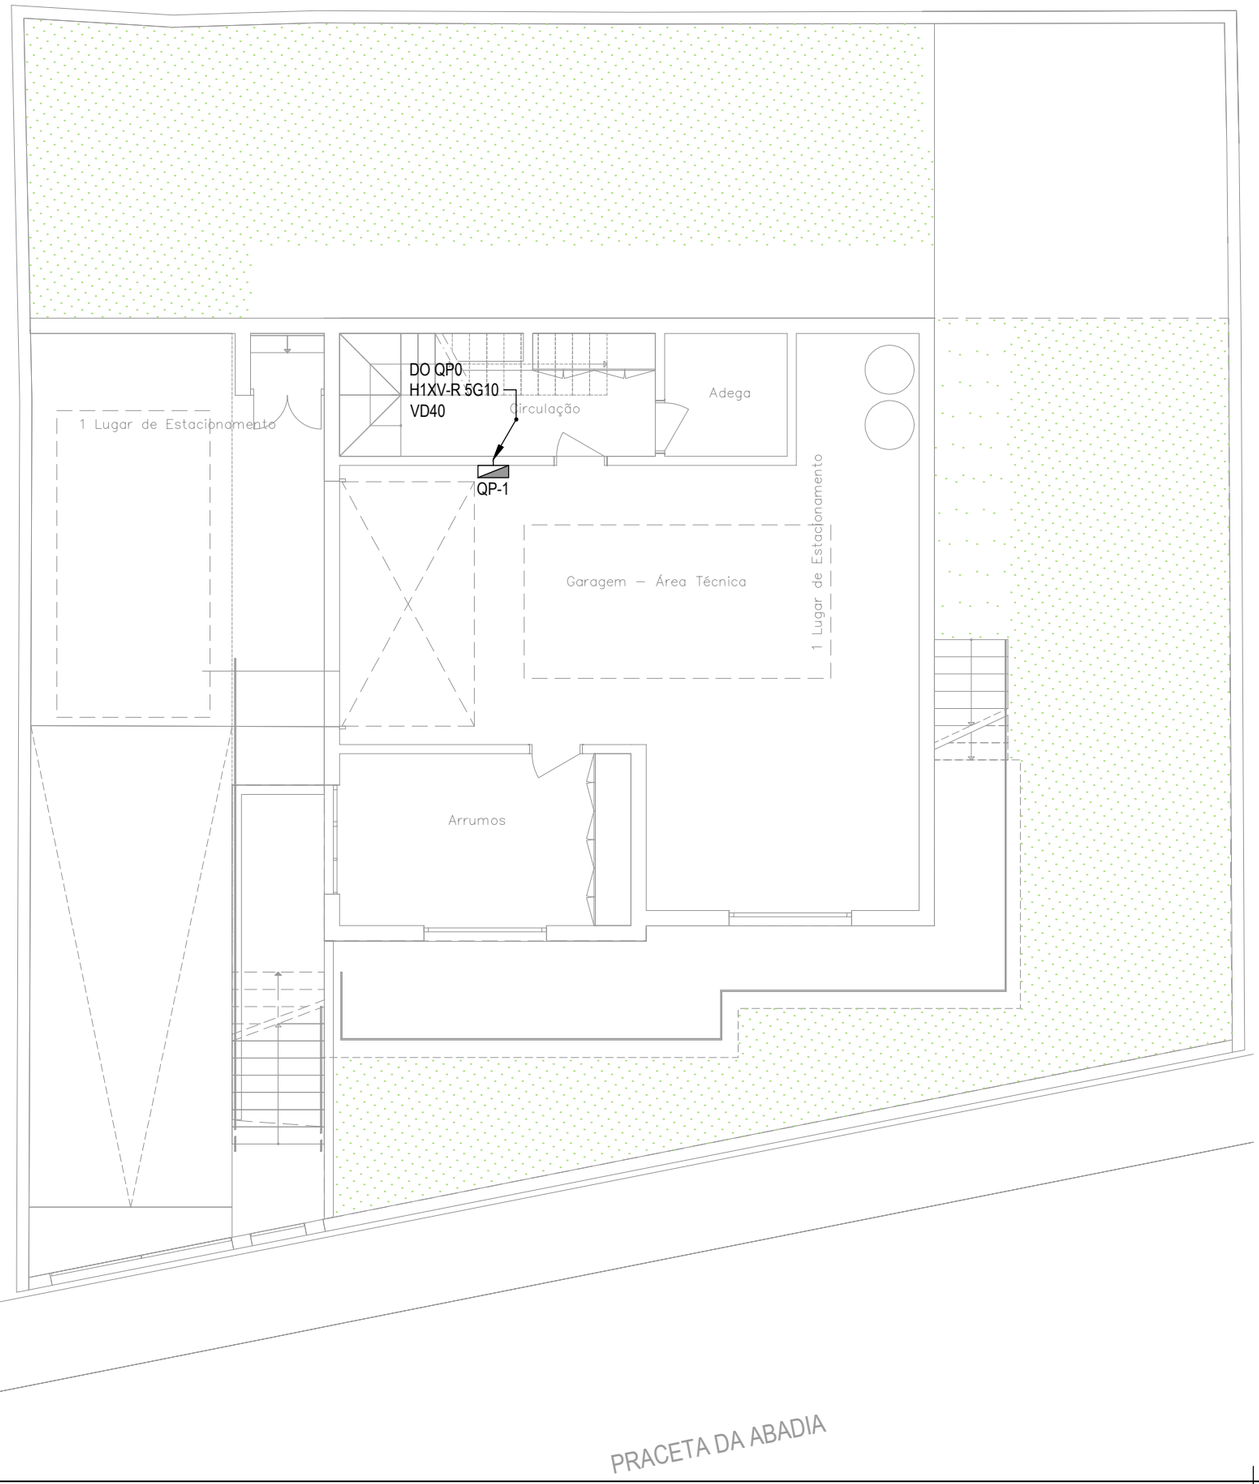


LOCAL	CLASSIFICAÇÃO DOS LOCAIS QUANTO ÀS INFLUÊNCIAS EXTERNAS	ÍNDICES	
		DE PROTECÇÃO	CONTRA IMPACTOS MECÂNICOS
EXTERIOR ABRIGADO	AA7, AB7, AD3, AL2, BC3, XX1	IP 43	IK 04
EXTERIOR NÃO ABRIGADO	AA8, AB8, AD5, AE5, AK2, AL2, BB2, BC3, XX1	IP 65	IK 08
SALAS, QUARTOS, CIRCULAÇÕES	AA4, AB4, XX1	IP 20	IK 04
I.S. / COZINHA / LAVANDARIA	AA4, AB4, XX1	IP 21	IK 04
CASAS DE BANHO (VOLUME DE PROTECÇÃO)	(V0) AA4, AB4, AD7, BB3, BC3, XX1 (V1) AA4, AB4, AD4, BB3, BC3, XX1 (V2) AA4, AB4, AD3, BB2, BC3, XX1 (V3) AA4, AB4, AD2, BB2, BC3, XX1	IP 27 IP 24 IP 23 IP 21	IK 04 IK 04 IK 04 IK 04
ARRUMOS/ÁREAS TÉCNICAS	AA4, AB4, AE2, XX1	IP 41	IK 04
GARAGEM	AA4, AB4, AE4, XX1	IP 51	IK 08

— — —	INSTALAÇÃO ENTERRADA
———	INSTALAÇÃO EMBEBIDA OU À VISTA EM TUBO VD / CC
	QUADRO ELÉTRICO
	PORTINHOLA
kWh	CONTADOR DE ENERGIA
	ELETRODO DE TERRA
	LIGADOR AMOVÍVEL

GAP LR
ENGENHARIA LDA

Telem.: 967 068 588 | fax: 219 863 894 | GAPLRgeral@gmail.com

PROJETO

CONSTRUÇÃO DE HABITAÇÃO UNIFAMILIAR

ESPECIALIDADE

INSTALAÇÕES ELÉTRICAS

DESIGNAÇÃO

Alimentações Gerais
Planta do Piso -1

REQUERENTE

Natasha Lara Santric


LOCAL

Praceta da Abadia, Lote 13
Ericeira
Mafra

DATA	PROCESSO	ESCALA
Julho 2026	3775	1/100

TÉCNICO	DESENHO N.º
Pedro Costa, Eng. 47924	**01**

A3 (297x420mm)

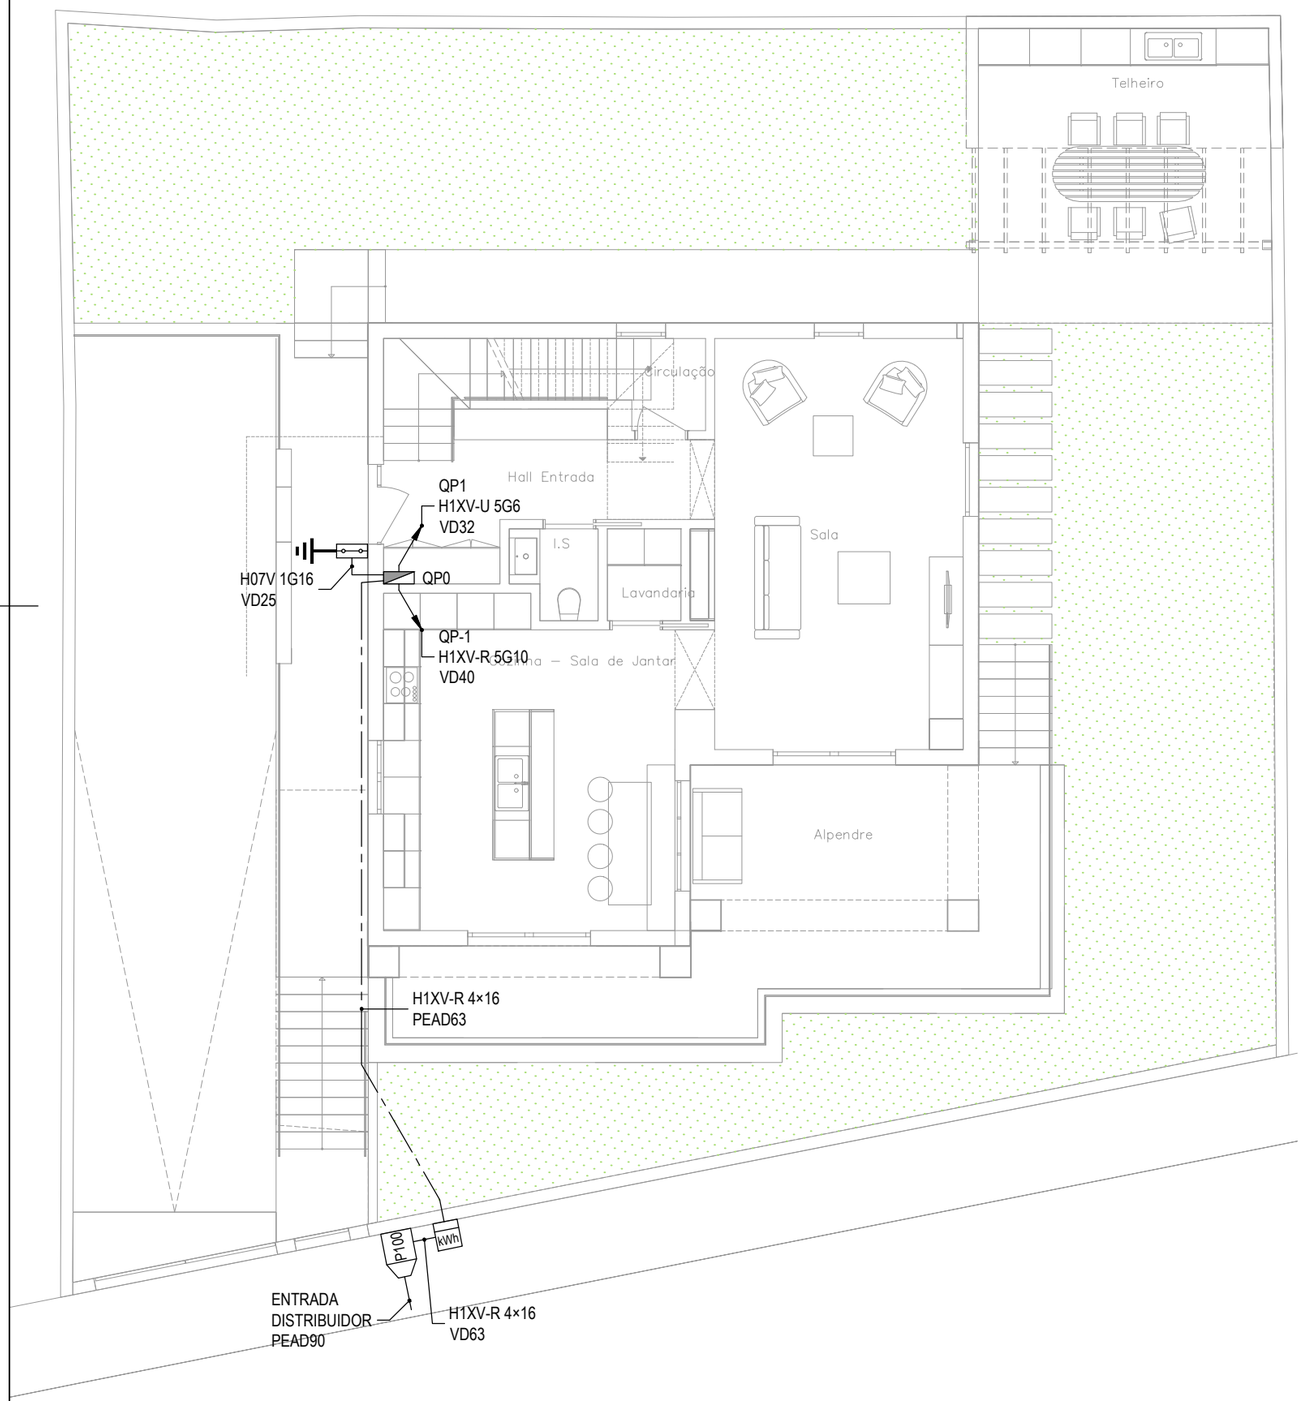

LOCAL	CLASSIFICAÇÃO DOS LOCAIS QUANTO ÀS INFLUÊNCIAS EXTERNAS	ÍNDICES	
		DE PROTECÇÃO	CONTRA IMPACTOS MECÂNICOS
EXTERIOR ABRIGADO	AA7, AB7, AD3, AL2, BC3, XX1	IP 43	IK 04
EXTERIOR NÃO ABRIGADO	AA8, AB8, AD5, AE5, AK2, AL2, BB2, BC3, XX1	IP 65	IK 08
SALAS, QUARTOS, CIRCULAÇÕES	AA4, AB4, XX1	IP 20	IK 04
I.S. / COZINHA / LAVANDARIA	AA4, AB4, XX1	IP 21	IK 04
CASAS DE BANHO (VOLUME DE PROTECÇÃO)	(V0) AA4, AB4, AD7, BB3, BC3, XX1 (V1) AA4, AB4, AD4, BB3, BC3, XX1 (V2) AA4, AB4, AD3, BB2, BC3, XX1 (V3) AA4, AB4, AD2, BB2, BC3, XX1	IP 27 IP 24 IP 23 IP 21	IK 04 IK 04 IK 04 IK 04
ARRUMOS/ÁREAS TÉCNICAS	AA4, AB4, AE2, XX1	IP 41	IK 04
GARAGEM	AA4, AB4, AE4, XX1	IP 51	IK 08

— - —	INSTALAÇÃO ENTERRADA
———	INSTALAÇÃO EMBEBIDA OU À VISTA EM TUBO VD / CC
	QUADRO ELÉTRICO
	PORTINHOLA
kWh	CONTADOR DE ENERGIA
	ELETRODO DE TERRA
	LIGADOR AMOVÍVEL

GAP LR
ENGENHARIA LDA
Telem.: 967 068 588 | fax: 219 863 894 | GAPLRgeral@gmail.com

PROJETO

CONSTRUÇÃO DE HABITAÇÃO UNIFAMILIAR

ESPECIALIDADE

Instalações Elétricas

DESIGNAÇÃO

Alimentações Gerais
Planta do Piso 0

REQUERENTE

Natasha Lara Santric


LOCAL

Praceta da Abadia, Lote 13
Ericeira
Mafra

DATA	PROCESSO	ESCALA
Julho 2026	3775	1/100

TÉCNICO	DESENHO N.º
Pedro Costa, Eng. 47924	**02**

A3 (297x420mm)

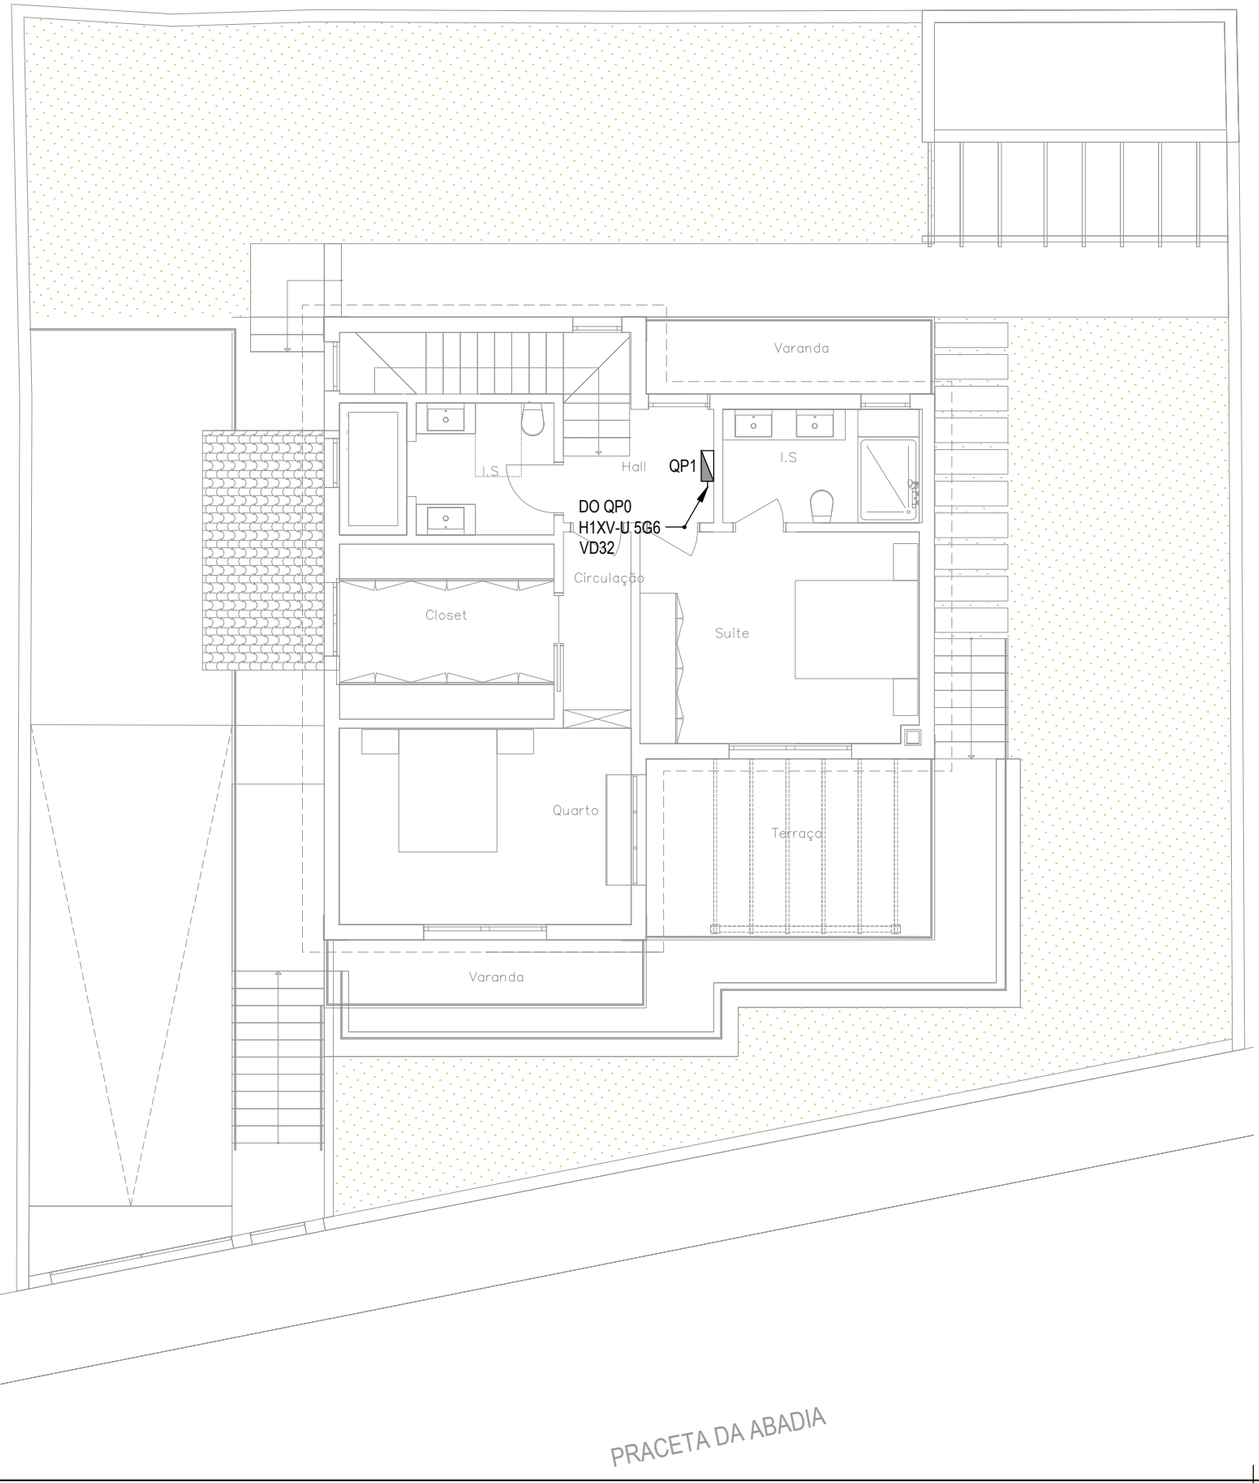

LOCAL	CLASSIFICAÇÃO DOS LOCAIS QUANTO ÀS INFLUÊNCIAS EXTERNAS	ÍNDICES	
		DE PROTECÇÃO	CONTRA IMPACTOS MECÂNICOS
EXTERIOR ABRIGADO	AA7, AB7, AD3, AL2, BC3, XX1	IP 43	IK 04
EXTERIOR NÃO ABRIGADO	AA8, AB8, AD5, AE5, AK2, AL2, BB2, BC3, XX1	IP 65	IK 08
SALAS, QUARTOS, CIRCULAÇÕES	AA4, AB4, XX1	IP 20	IK 04
I.S. / COZINHA / LAVANDARIA	AA4, AB4, XX1	IP 21	IK 04
CASAS DE BANHO (VOLUME DE PROTECÇÃO)	(V0) AA4, AB4, AD7, BB3, BC3, XX1 (V1) AA4, AB4, AD4, BB3, BC3, XX1 (V2) AA4, AB4, AD3, BB2, BC3, XX1 (V3) AA4, AB4, AD2, BB2, BC3, XX1	IP 27 IP 24 IP 23 IP 21	IK 04 IK 04 IK 04 IK 04
ARRUMOS/ÁREAS TÉCNICAS	AA4, AB4, AE2, XX1	IP 41	IK 04
GARAGEM	AA4, AB4, AE4, XX1	IP 51	IK 08

— — —	INSTALAÇÃO ENTERRADA
———	INSTALAÇÃO EMBEBIDA OU À VISTA EM TUBO VD / CC
	QUADRO ELÉTRICO
	PORTINHOLA
kWh	CONTADOR DE ENERGIA
	ELETRODO DE TERRA
	LIGADOR AMOVÍVEL

GAP LR
ENGENHARIA LDA

Telem.: 967 068 588 | fax: 219 863 894 | GAPLRgeral@gmail.com

PROJETO

CONSTRUÇÃO DE HABITAÇÃO UNIFAMILIAR

ESPECIALIDADE

INSTALAÇÕES ELÉTRICAS

DESIGNAÇÃO

Alimentações Gerais
Planta do Piso 1

REQUERENTE

Natasha Lara Santric


LOCAL

Praceta da Abadia, Lote 13
Ericeira
Mafra

DATA	PROCESSO	ESCALA
Julho 2026	3775	1/100

TÉCNICO	DESENHO N.º
Pedro Costa, Eng. 47924	**03**

A3 (297x420mm)

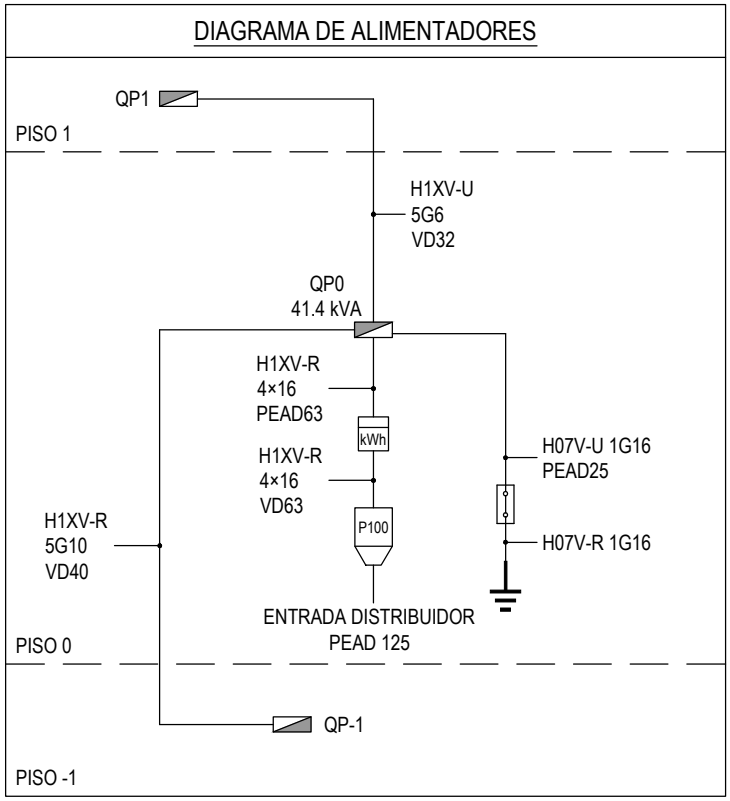

GAP LR
ENGENHARIA LDA

Telem.: 967 068 588 | fax: 219 863 894 | GAPLRgeral@gmail.com

PROJETO

CONSTRUÇÃO DE HABITAÇÃO UNIFAMILIAR

ESPECIALIDADE

INSTALAÇÕES ELÉTRICAS

DESIGNAÇÃO

Diagrama de Alimentadores

REQUERENTE

Natasha Lara Santric

LOCAL

Praceta da Abadia, Lote 13
Ericeira
Mafra

DATA	PROCESSO	ESCALA
Julho 2026	3775	S/E

TÉCNICO	DESENHO N.º
Pedro Costa, Eng. 47924	**04**

A4 (297x210mm)