INDICE

01 a 03 - PLANTAS
04 a 06 - ÁREAS
07 a 09 - ENVOLVENTES PAVIMENTOS
10 a 12 - ENVOLVENTES COBERTURAS

GAPLR
ENGENHARIA LDA
Telem.: 967 068 588 | fax: 219 863 894 | GAPLRgeral@gmail.com

PROJETO
CONSTRUÇÃO DE
MORADIA UNIFAMILIAR

ESPECIALIDADE
COMPORTAMENTO TÉRMICO

DESIGNAÇÃO
INDICE


REQUERENTE
NATASHA LARA SANTRIC


LOCAL
PRACETA DA ABADIA LOTE 13
ERICEIRA
MAFRA

DATA	PROCESSO	ESCALA
JUL DE 2026	3775	1/100

TÉCNICO	DESENHO N.º
Eng.º Luis Reis 21981 O.E.	INDICE

A4 (297x210mm)

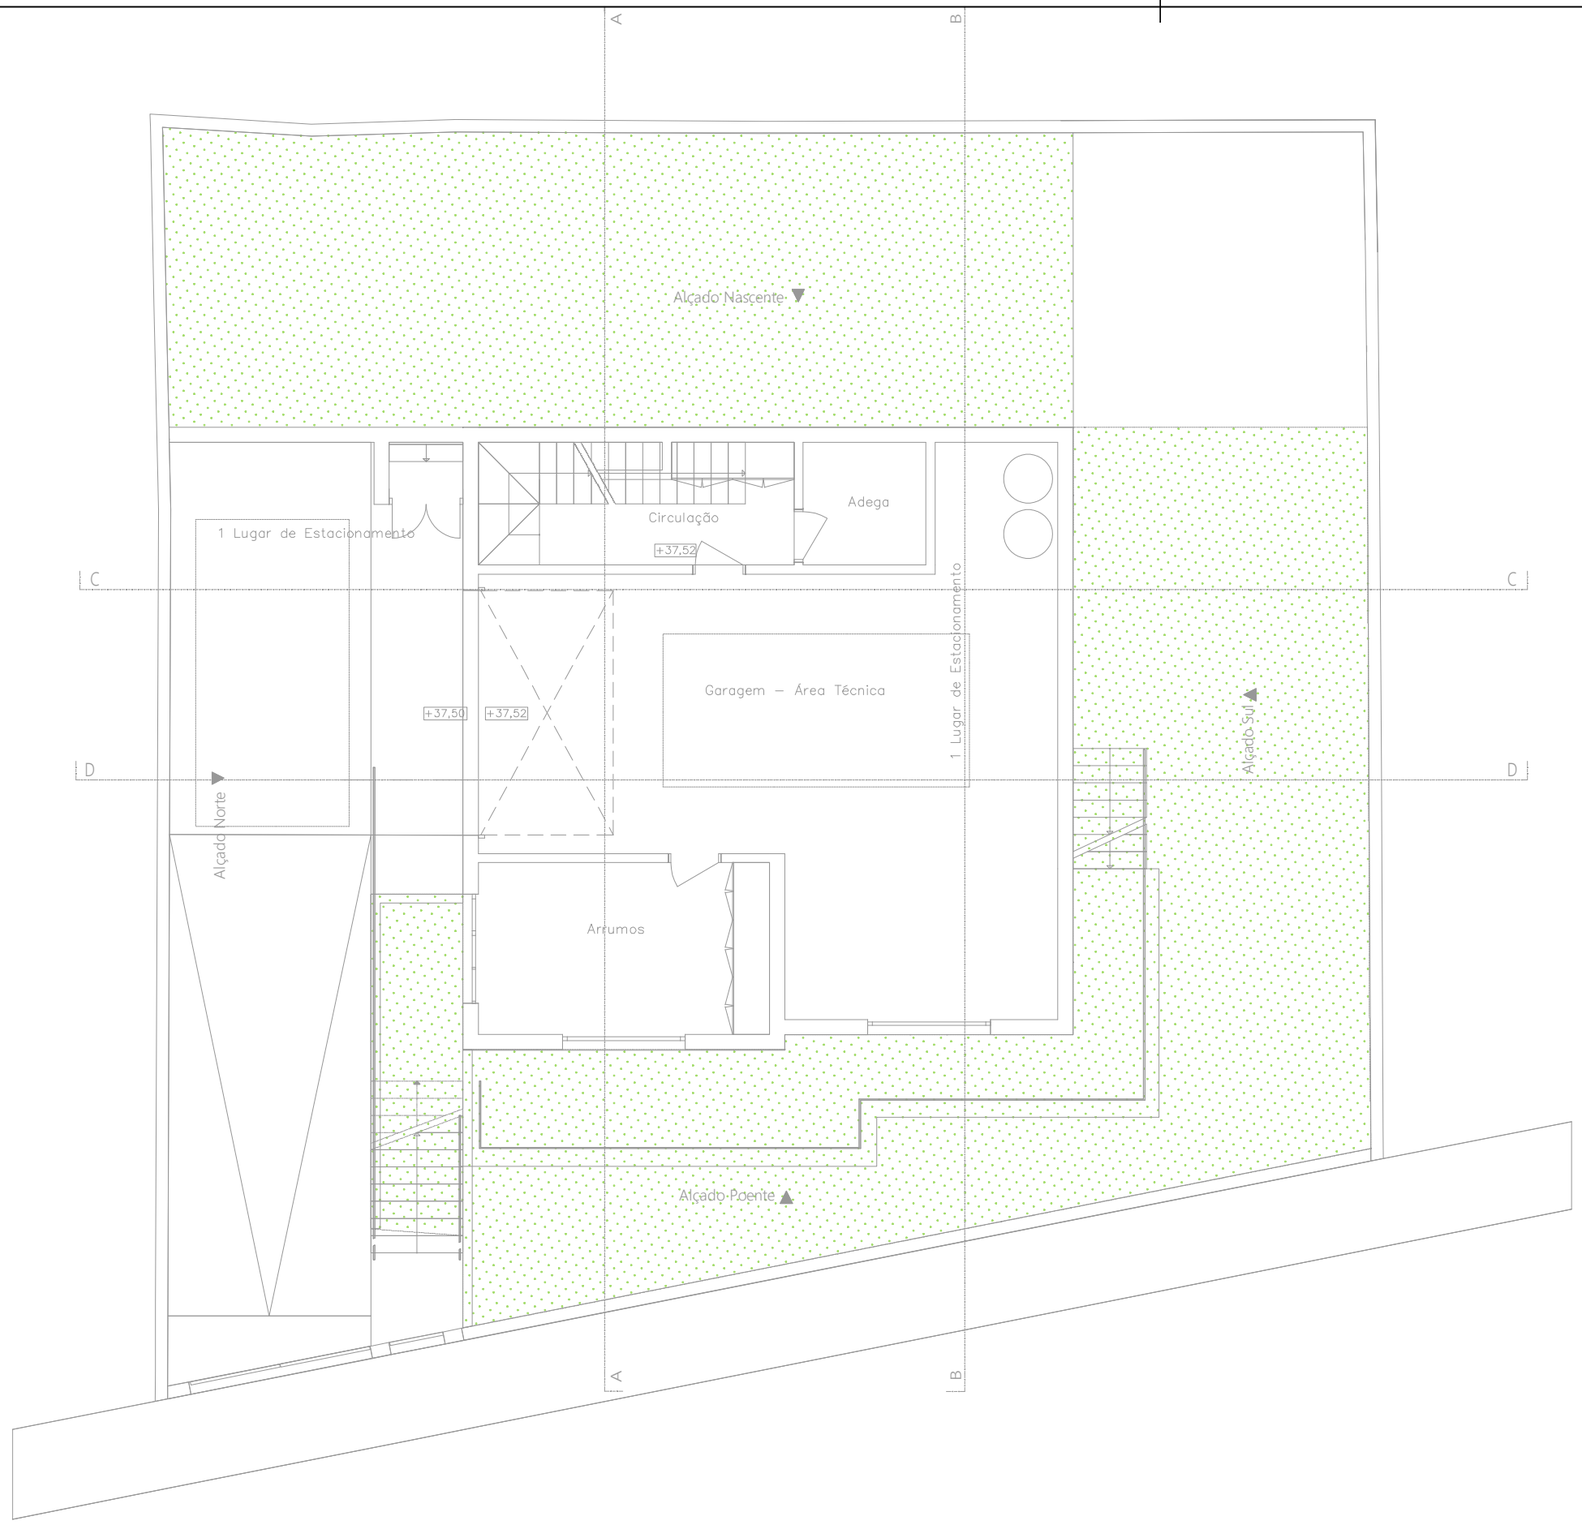

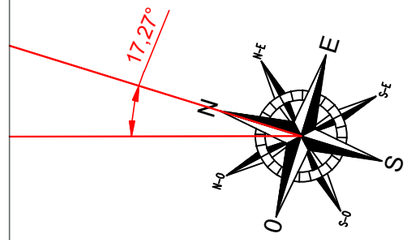

Planta do Piso -1

A3 (297x420mm)

GAPLR
ENGENHARIA LDA
Telem.: 967 068 588 | fax: 219 863 894 | GAPLRgeral@gmail.com

PROJETO
CONSTRUÇÃO DE MORADIA UNIFAMILIAR

ESPECIALIDADE
COMPORTAMENTO TÉRMICO


DESIGNAÇÃO
Planta do Piso -1


REQUERENTE
NATASHA LARA SANTRIC

LOCAL
PRACETA DA ABADIA LOTE 13
ERICEIRA
MAFRA

DATA	PROCESSO	ESCALA
JUL DE 2026	3775	1/100

TÉCNICO	DESENHO N.º
Eng.º Luis Reis 21981 O.E.	01

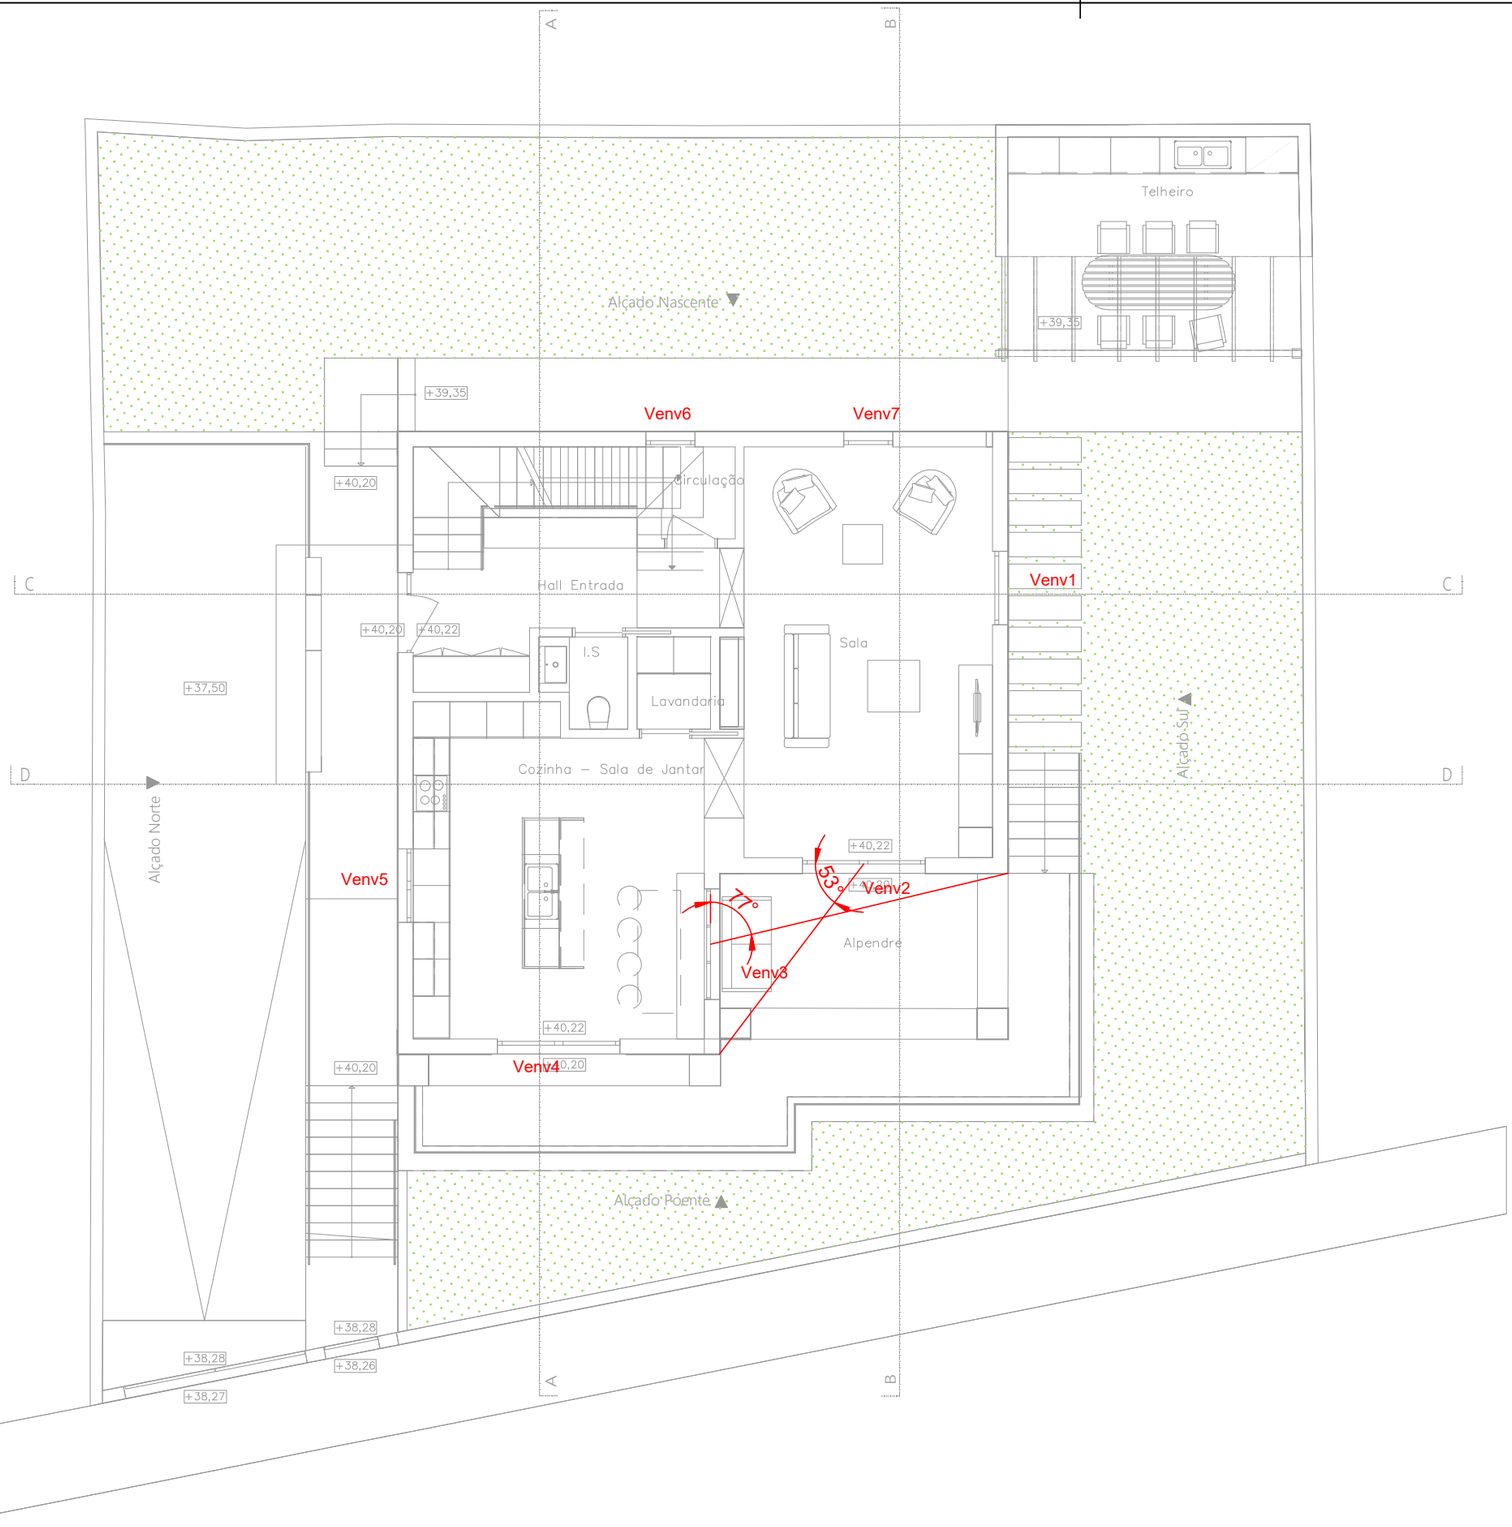

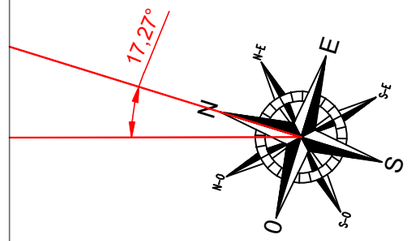

Planta do Piso 0

A3 (297x420mm)

GAPLR
ENGENHARIA LDA
Telem.: 967 068 588 | fax: 219 863 894 | GAPLRgeral@gmail.com

PROJETO
CONSTRUÇÃO DE MORADIA UNIFAMILIAR

ESPECIALIDADE
COMPORTAMENTO TÉRMICO


DESIGNAÇÃO
Planta do Piso 0

REQUERENTE
NATASHA LARA SANTRIC


LOCAL
PRACETA DA ABADIA LOTE 13
ERICEIRA
MAFRA

DATA	PROCESSO	ESCALA
JUL DE 2026	3775	1/100

TÉCNICO	DESENHO N.º
Eng.º Luis Reis 21981 O.E.	02

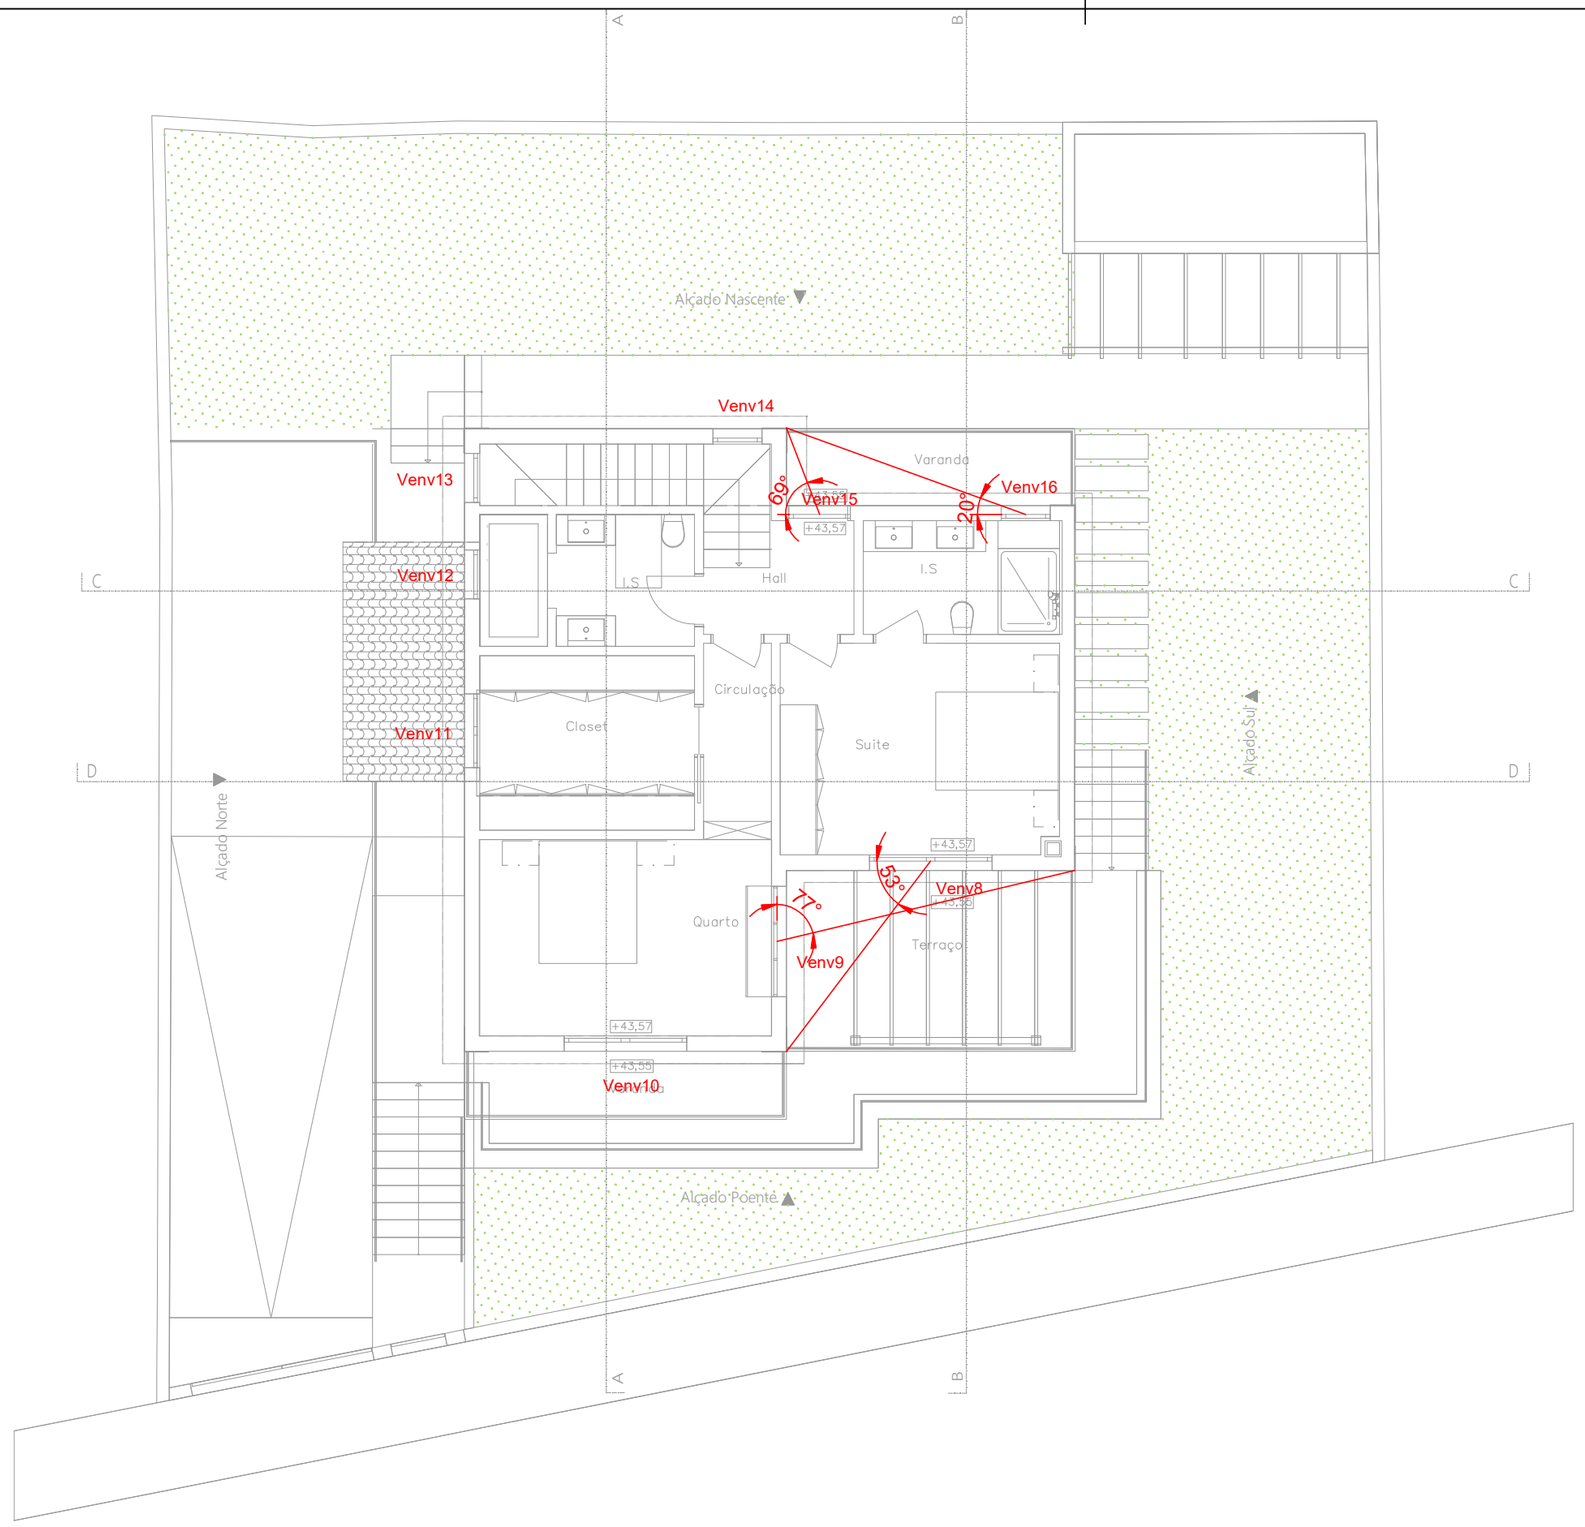

Planta do Piso 1

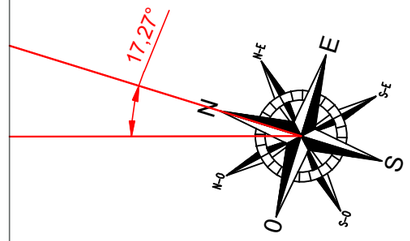

GAPLR
ENGENHARIA LDA
Telem.: 967 068 588 | fax: 219 863 894 | GAPLRgeral@gmail.com

PROJETO
CONSTRUÇÃO DE MORADIA UNIFAMILIAR

ESPECIALIDADE
COMPORTAMENTO TÉRMICO

DESIGNAÇÃO
Planta do Piso 1

REQUERENTE
NATASHA LARA SANTRIC


LOCAL
PRACETA DA ABADIA LOTE 13
ERICEIRA
MAFRA

DATA	PROCESSO	ESCALA
JUL DE 2026	3775	1/100


TÉCNICO
Eng.º Luis Reis
21981 O.E.

DESENHO N.º
03

A3 (297x420mm)

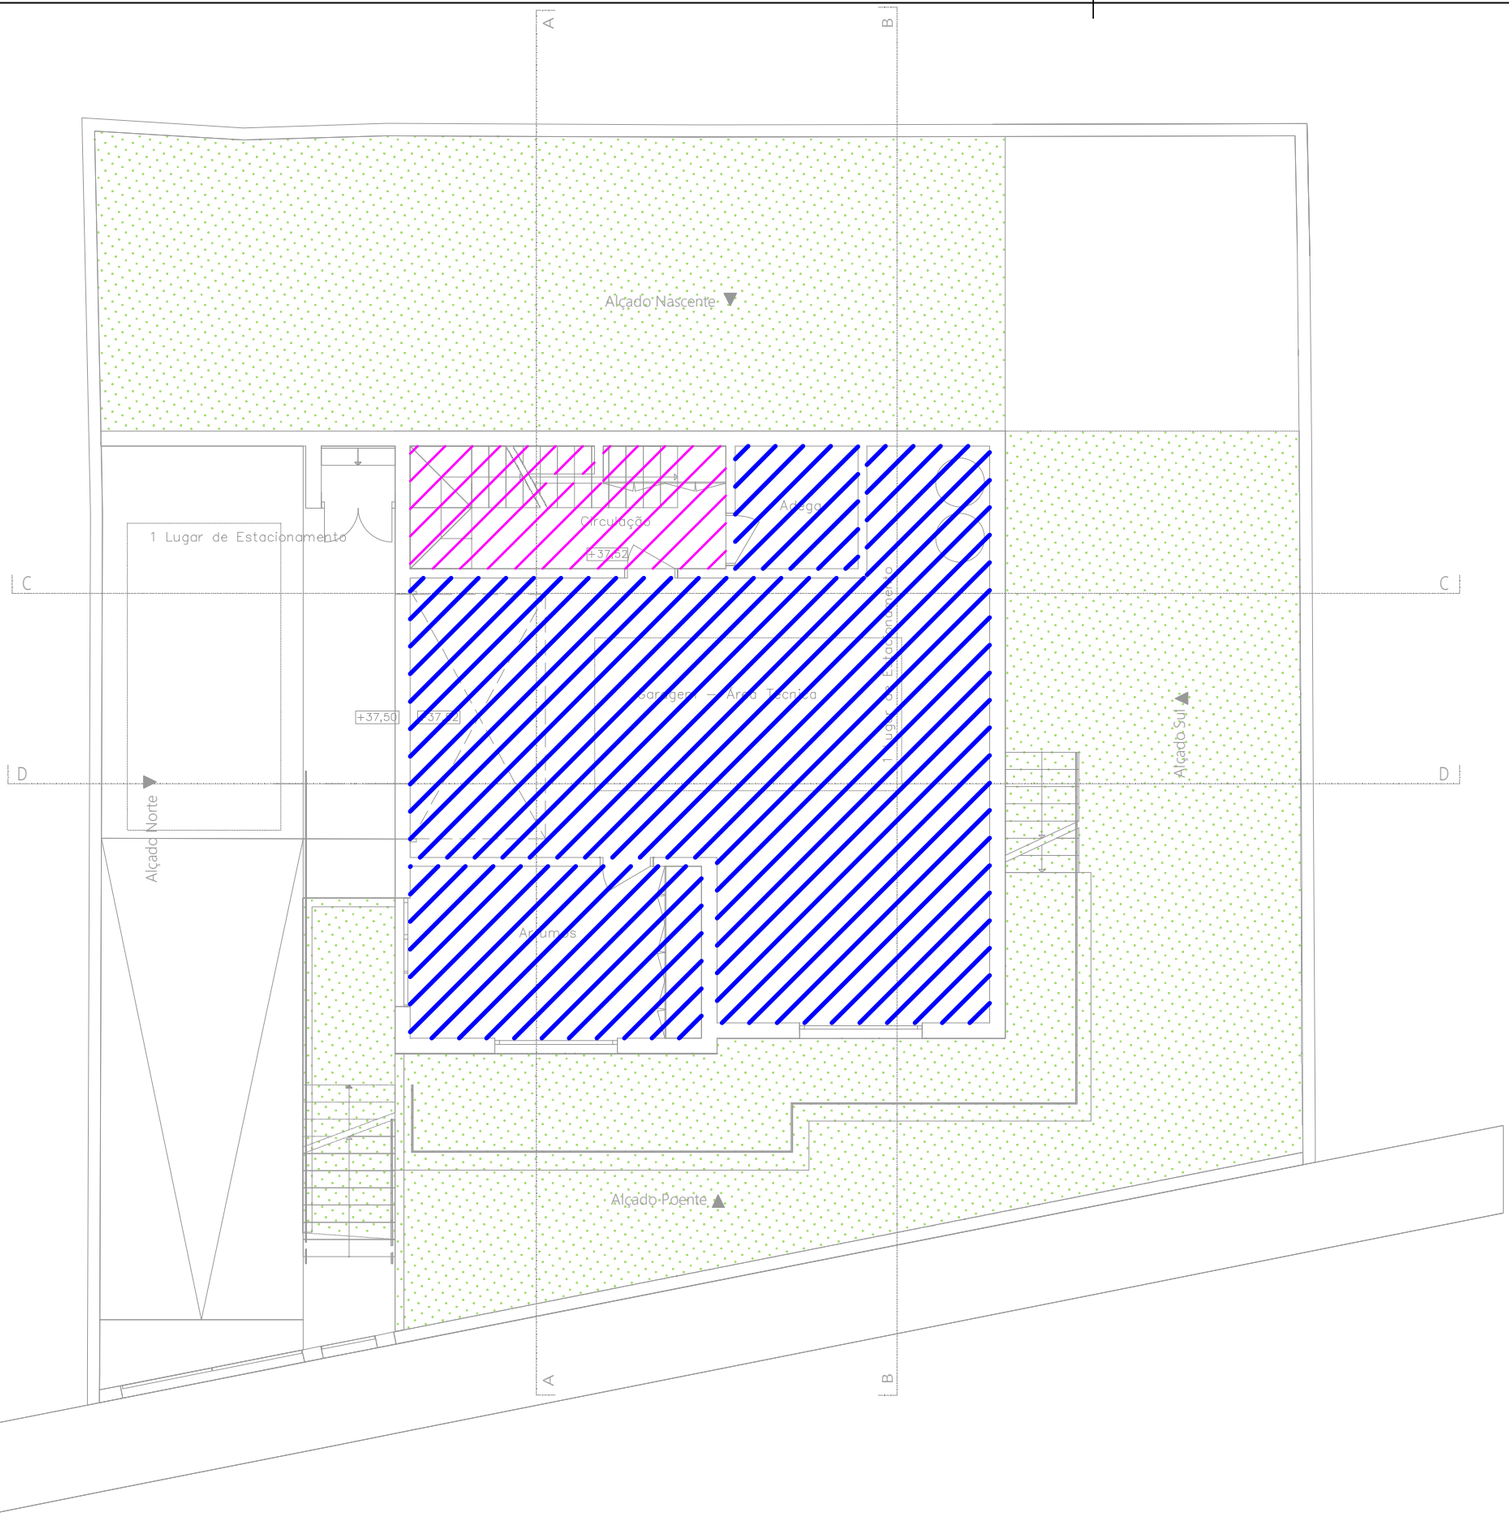

Planta do Piso -1

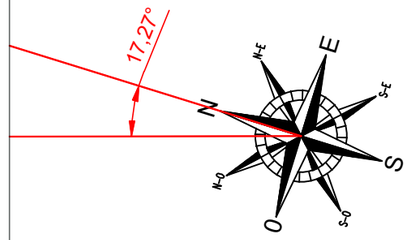

Legenda:

- Espaço interior Útil
- Espaço interior Não Útil (bztu>0.7)
- Espaço interior Não Útil (bztu<=0.7)

GAPLR
ENGENHARIA LDA
Telem.: 967 068 588 | fax: 219 863 894 | GAPLRgeral@gmail.com

PROJETO
CONSTRUÇÃO DE MORADIA UNIFAMILIAR

ESPECIALIDADE
COMPORTAMENTO TÉRMICO

DESIGNAÇÃO
Planta de def. de áreas - Piso -1

REQUERENTE
NATASHA LARA SANTRIC


LOCAL
PRACETA DA ABADIA LOTE 13
ERICEIRA
MAFRA

DATA	PROCESSO	ESCALA
JUL DE 2026	3775	1/100


TÉCNICO
Eng.º Luis Reis
21981 O.E.

DESENHO N.º
04

A3 (297x420mm)

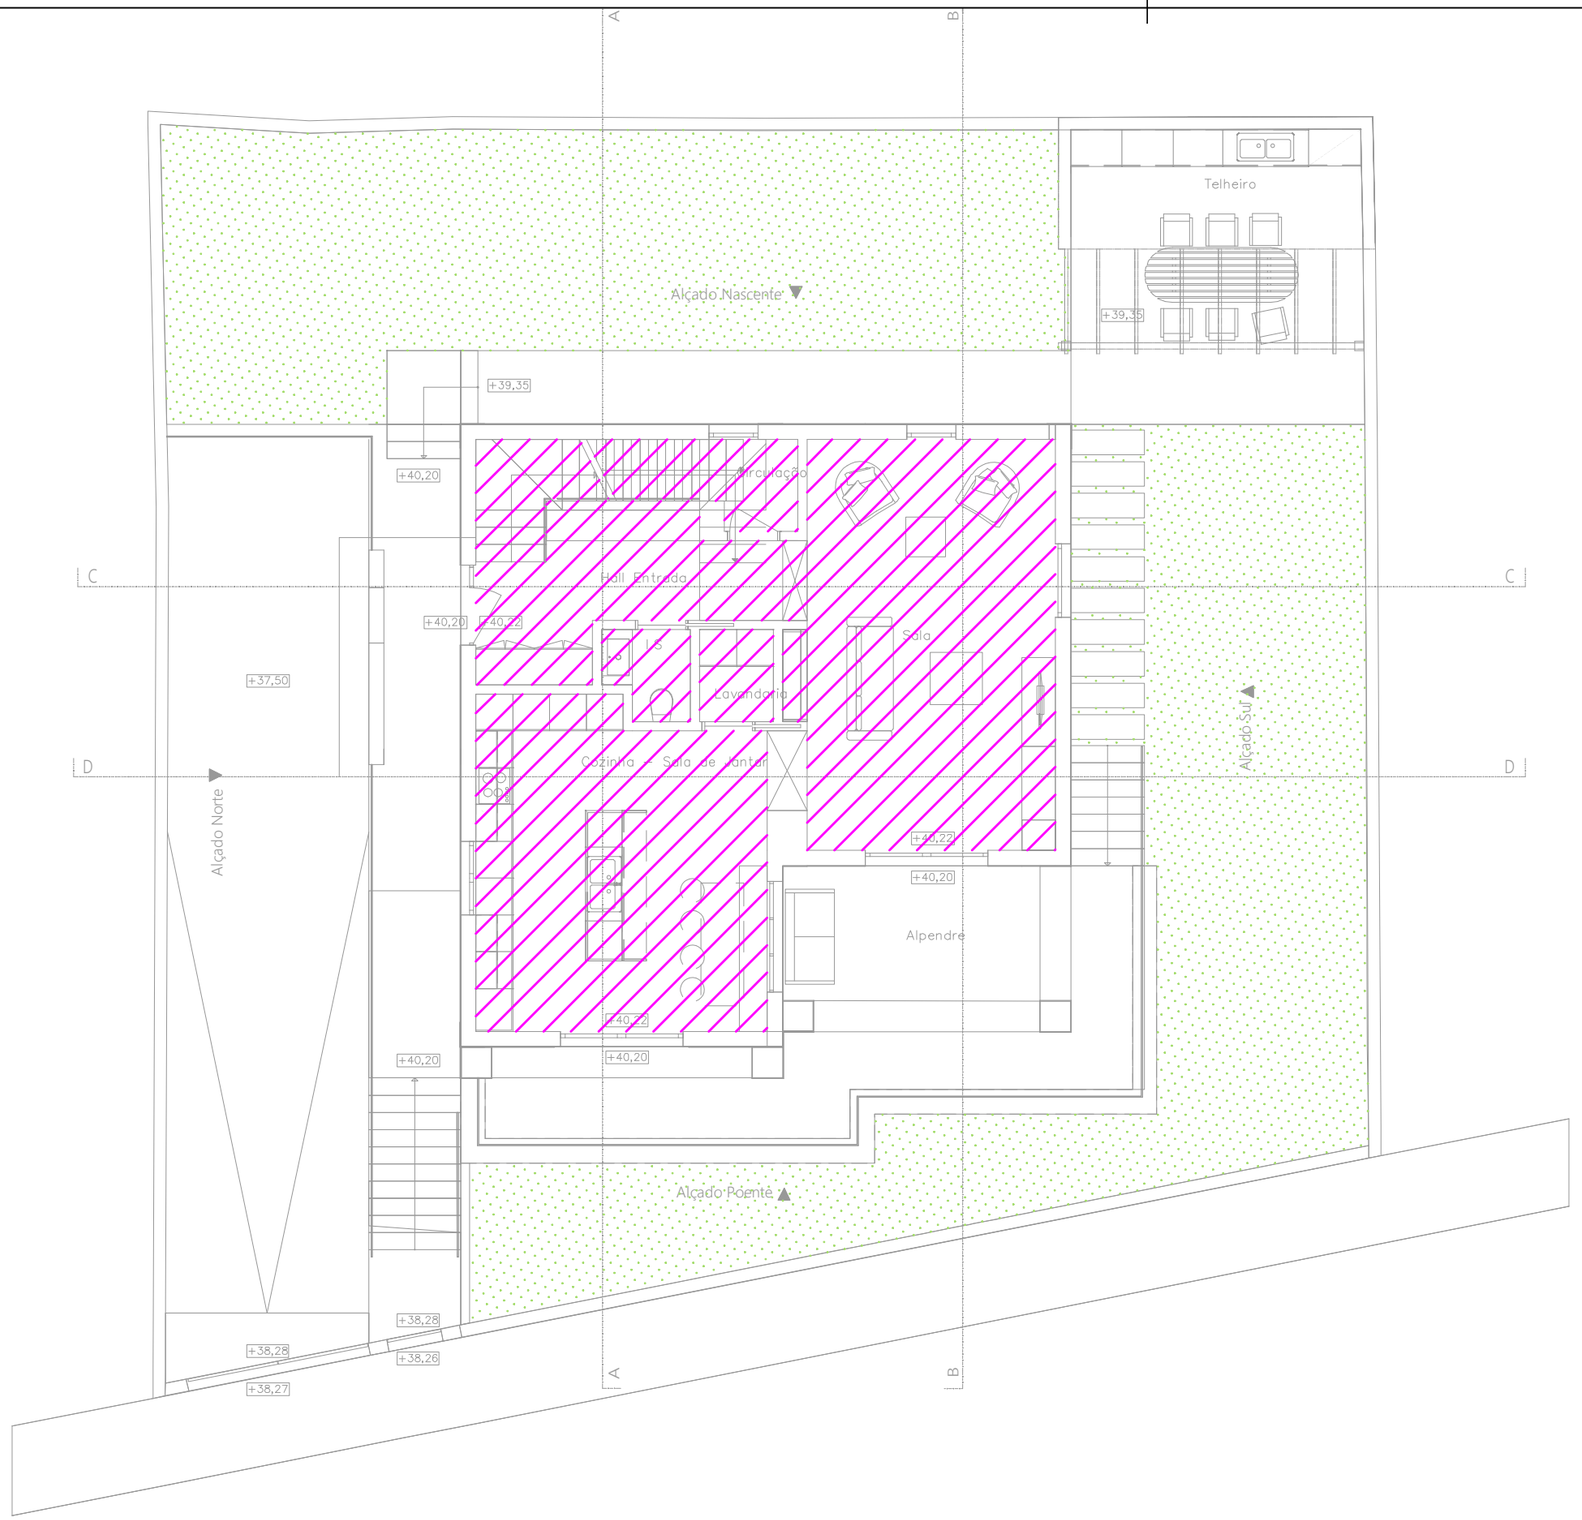

Planta do Piso 0

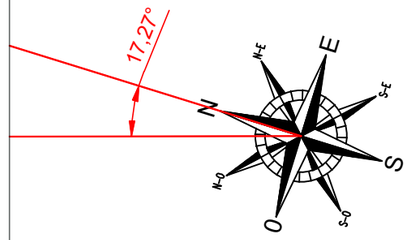

Legenda:

- Espaço interior Útil
- Espaço interior Não Útil (bztu>0.7)
- Espaço interior Não Útil (bztu<=0.7)

GAPLR
ENGENHARIA LDA
Telem.: 967 068 588 | fax: 219 863 894 | GAPLRgeral@gmail.com

PROJETO
CONSTRUÇÃO DE MORADIA UNIFAMILIAR

ESPECIALIDADE
COMPORTAMENTO TÉRMICO

DESIGNAÇÃO
Planta de def. de áreas - Piso 0


REQUERENTE
NATASHA LARA SANTRIC

LOCAL
PRACETA DA ABADIA LOTE 13
ERICEIRA
MAFRA


DATA	PROCESSO	ESCALA
JUL DE 2026	3775	1/100

TÉCNICO	DESENHO N.º
Eng.º Luis Reis 21981 O.E.	05

A3 (297x420mm)

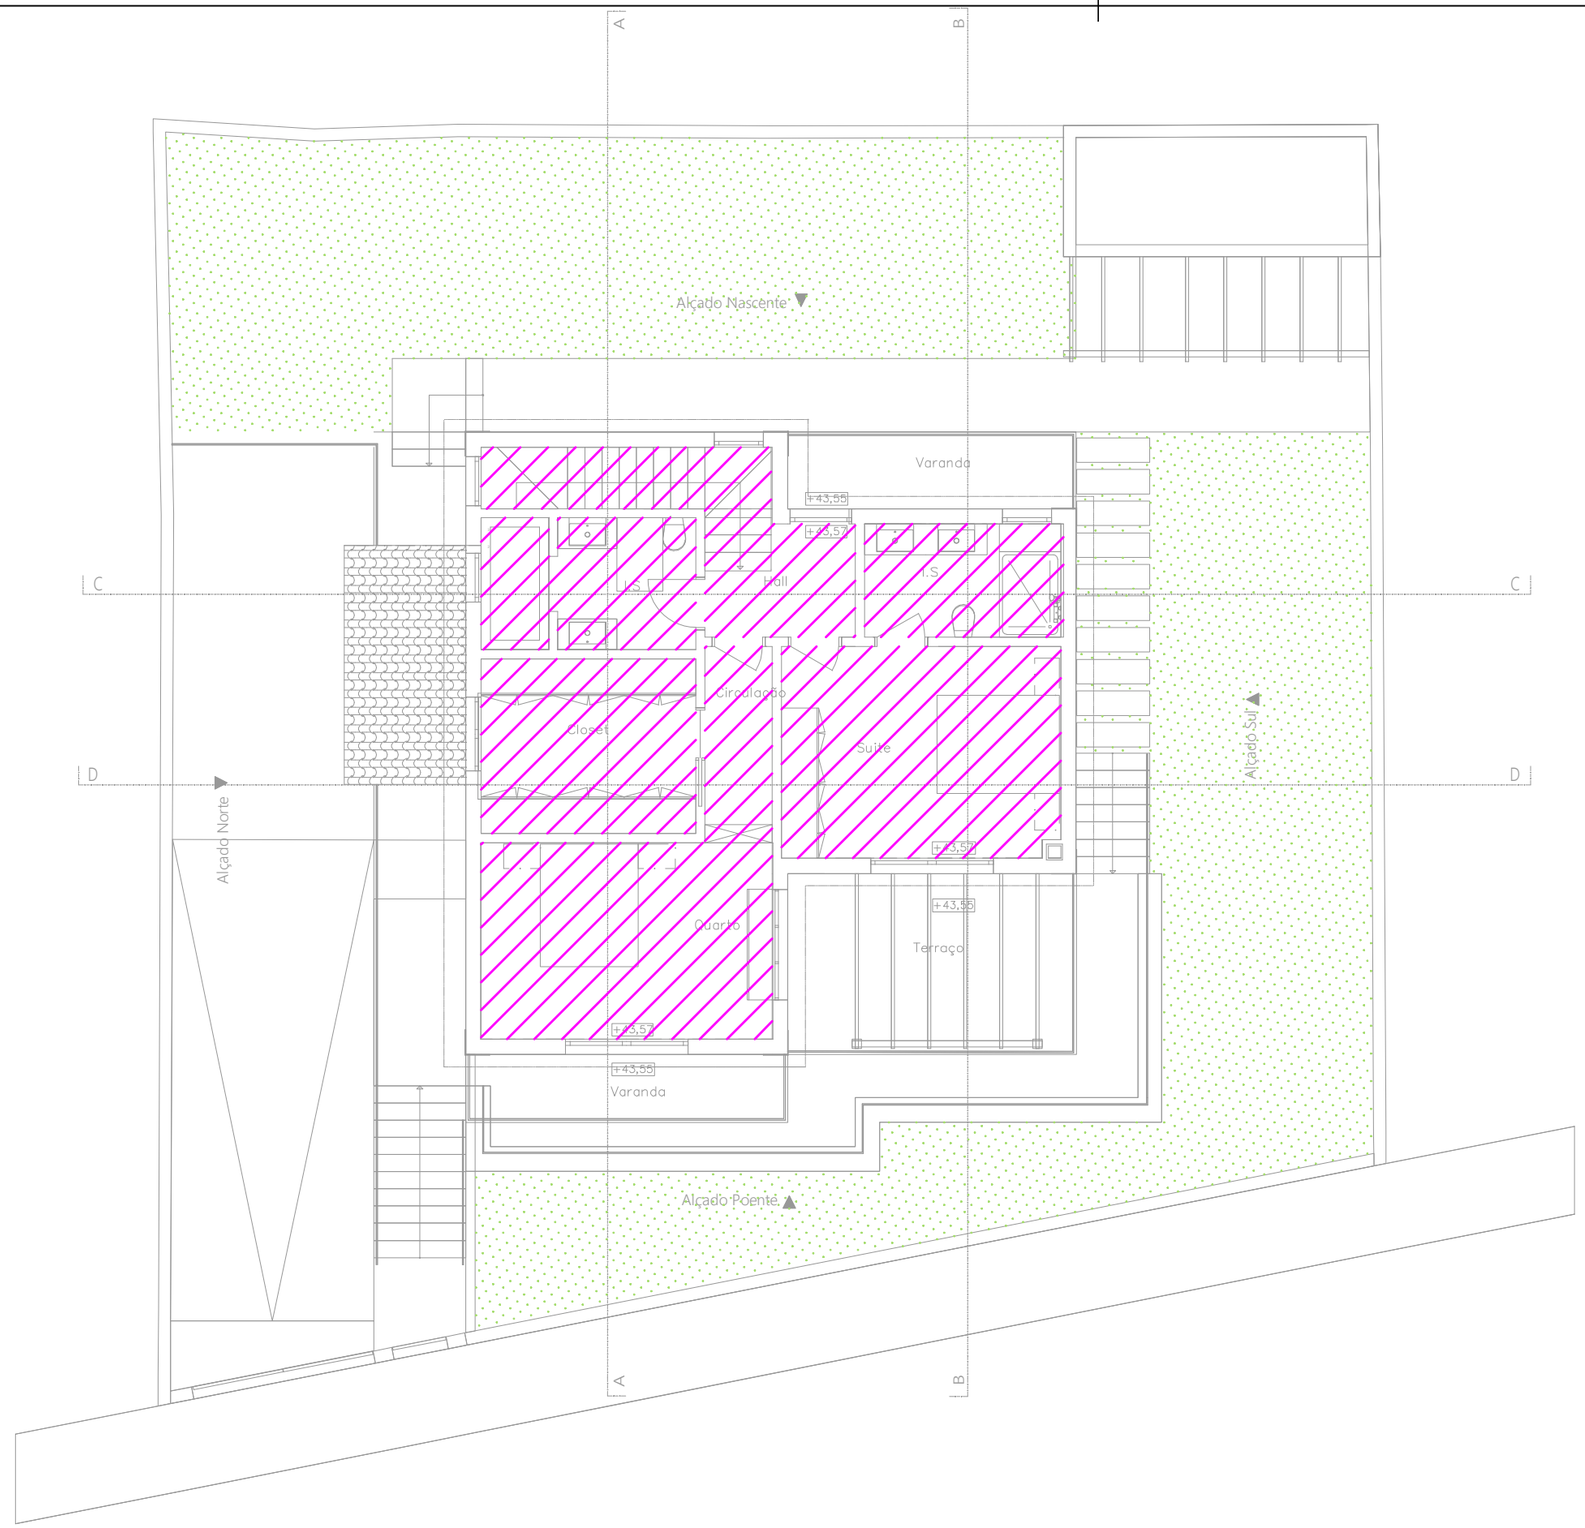

Planta do Piso 1

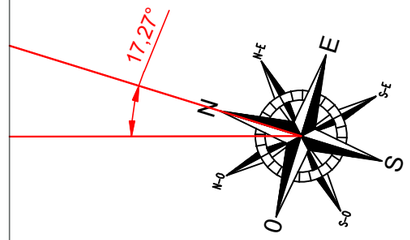

Legenda:

- Espaço interior Útil
- Espaço interior Não Útil (bztu>0.7)
- Espaço interior Não Útil (bztu<=0.7)

GAPLR ENGENHARIA LDA

Telem.: 967 068 588 | fax: 219 863 894 | GAPLRgeral@gmail.com

PROJETO
CONSTRUÇÃO DE MORADIA UNIFAMILIAR

ESPECIALIDADE
COMPORTAMENTO TÉRMICO

DESIGNAÇÃO
Planta de def. de áreas - Piso 1

REQUERENTE
NATASHA LARA SANTRIC


LOCAL
PRACETA DA ABADIA LOTE 13
ERICEIRA
MAFRA


DATA	PROCESSO	ESCALA
JUL DE 2026	3775	1/100

TÉCNICO
Eng.º Luis Reis
21981 O.E.

DESENHO N.º
06

A3 (297x420mm)

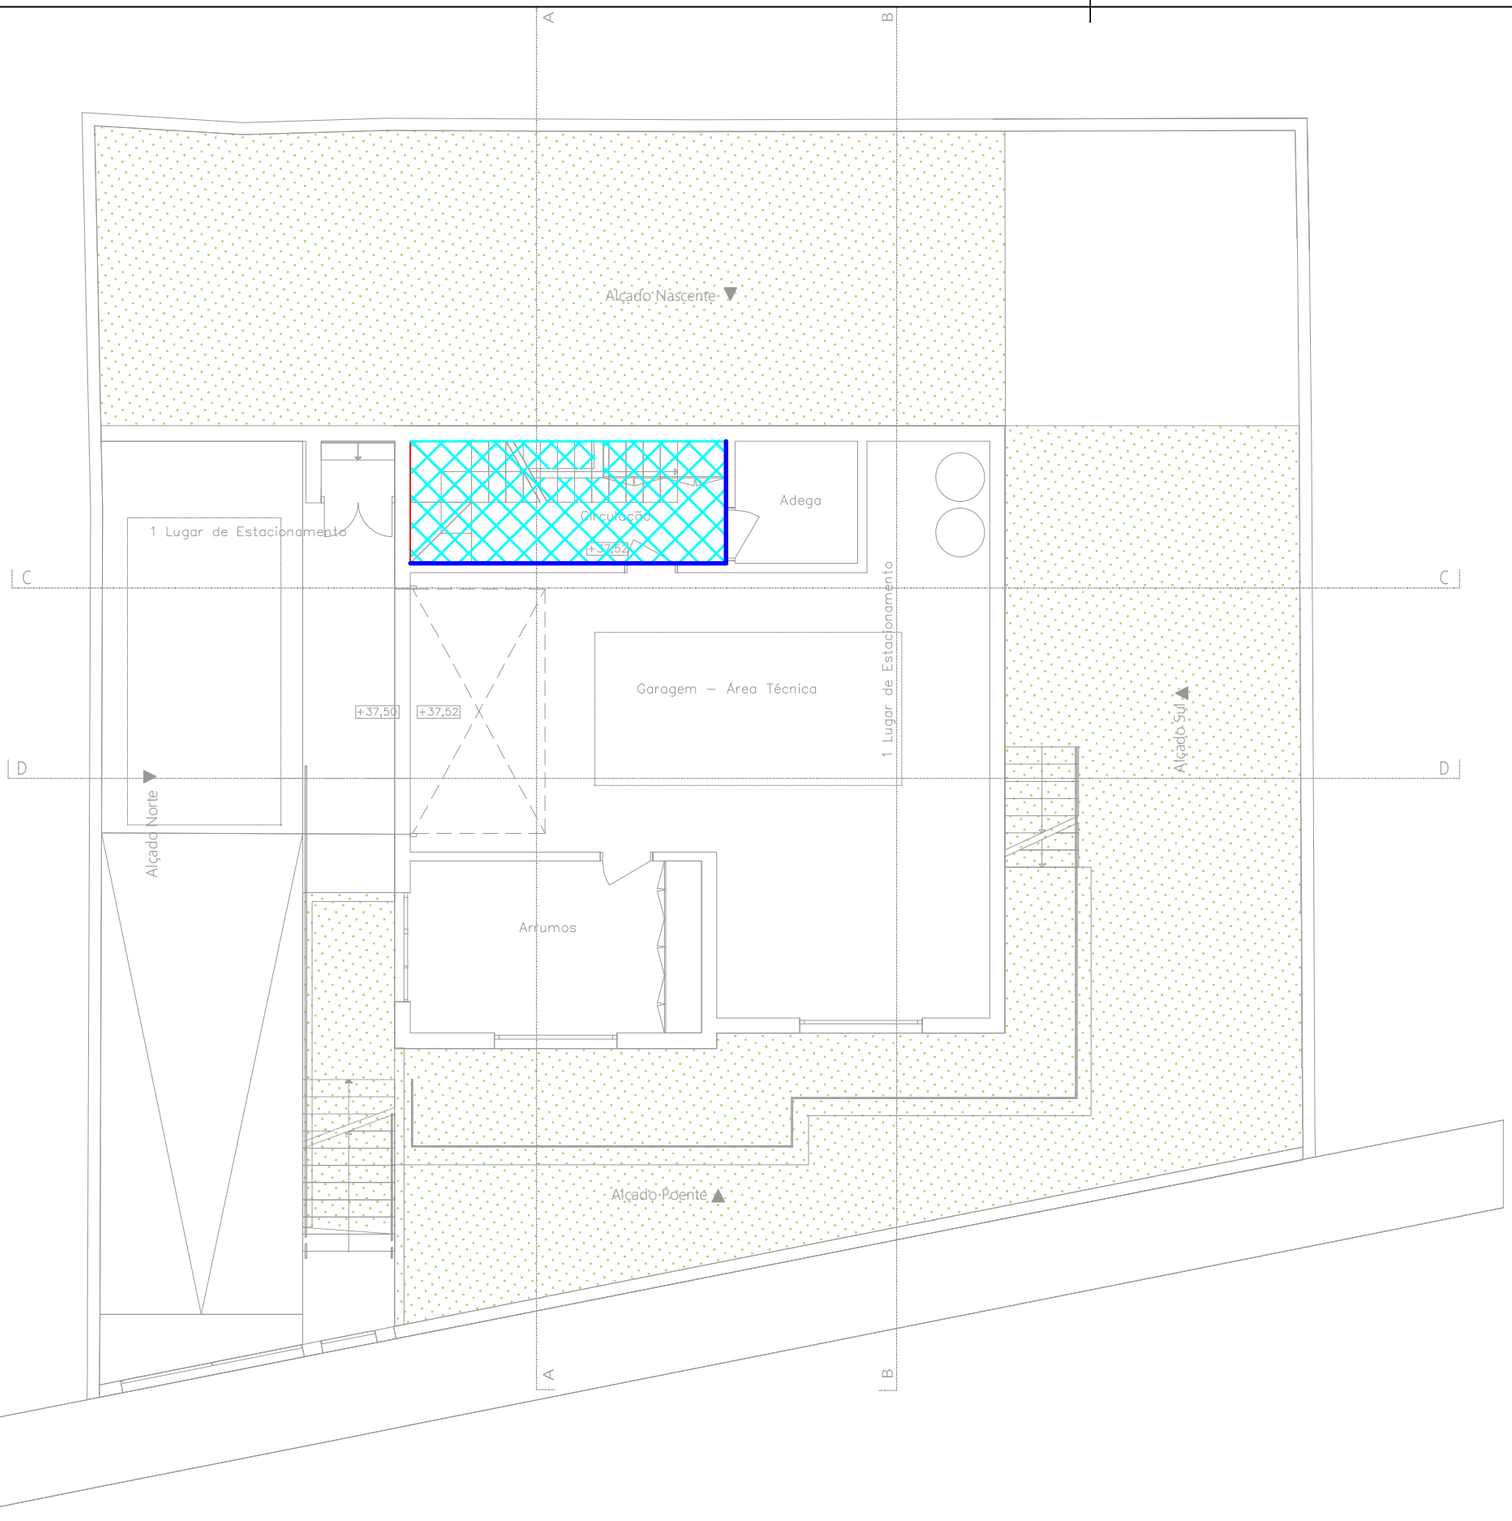

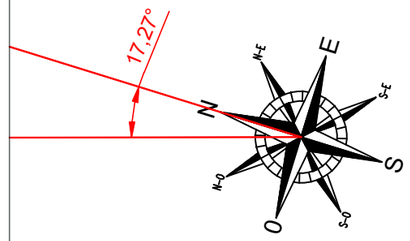

Legenda:

- Pavimento interior com requisitos de interior - PavI1
- Pavimento em contacto com o solo - PavS1
- Envolvente exterior - ParE1
- Envolvente interior com requisitos de interior - ParI1
- Envolvente em contacto com o solo - ParS1

Planta do Piso -1

A3 (297x420mm)

GAPLR
ENGENHARIA LDA
Telem.: 967 068 588 | fax: 219 863 894 | GAPLRgeral@gmail.com

PROJETO
CONSTRUÇÃO DE MORADIA UNIFAMILIAR

ESPECIALIDADE
COMPORTAMENTO TÉRMICO


DESIGNAÇÃO
Plt. de envol. - Pav. do Piso -1

REQUERENTE
NATASHA LARA SANTRIC


LOCAL
PRACETA DA ABADIA LOTE 13
ERICEIRA
MAFRA

DATA	PROCESSO	ESCALA
JUL DE 2026	3775	1/100

TÉCNICO	DESENHO N.º
Eng.º Luis Reis 21981 O.E.	07

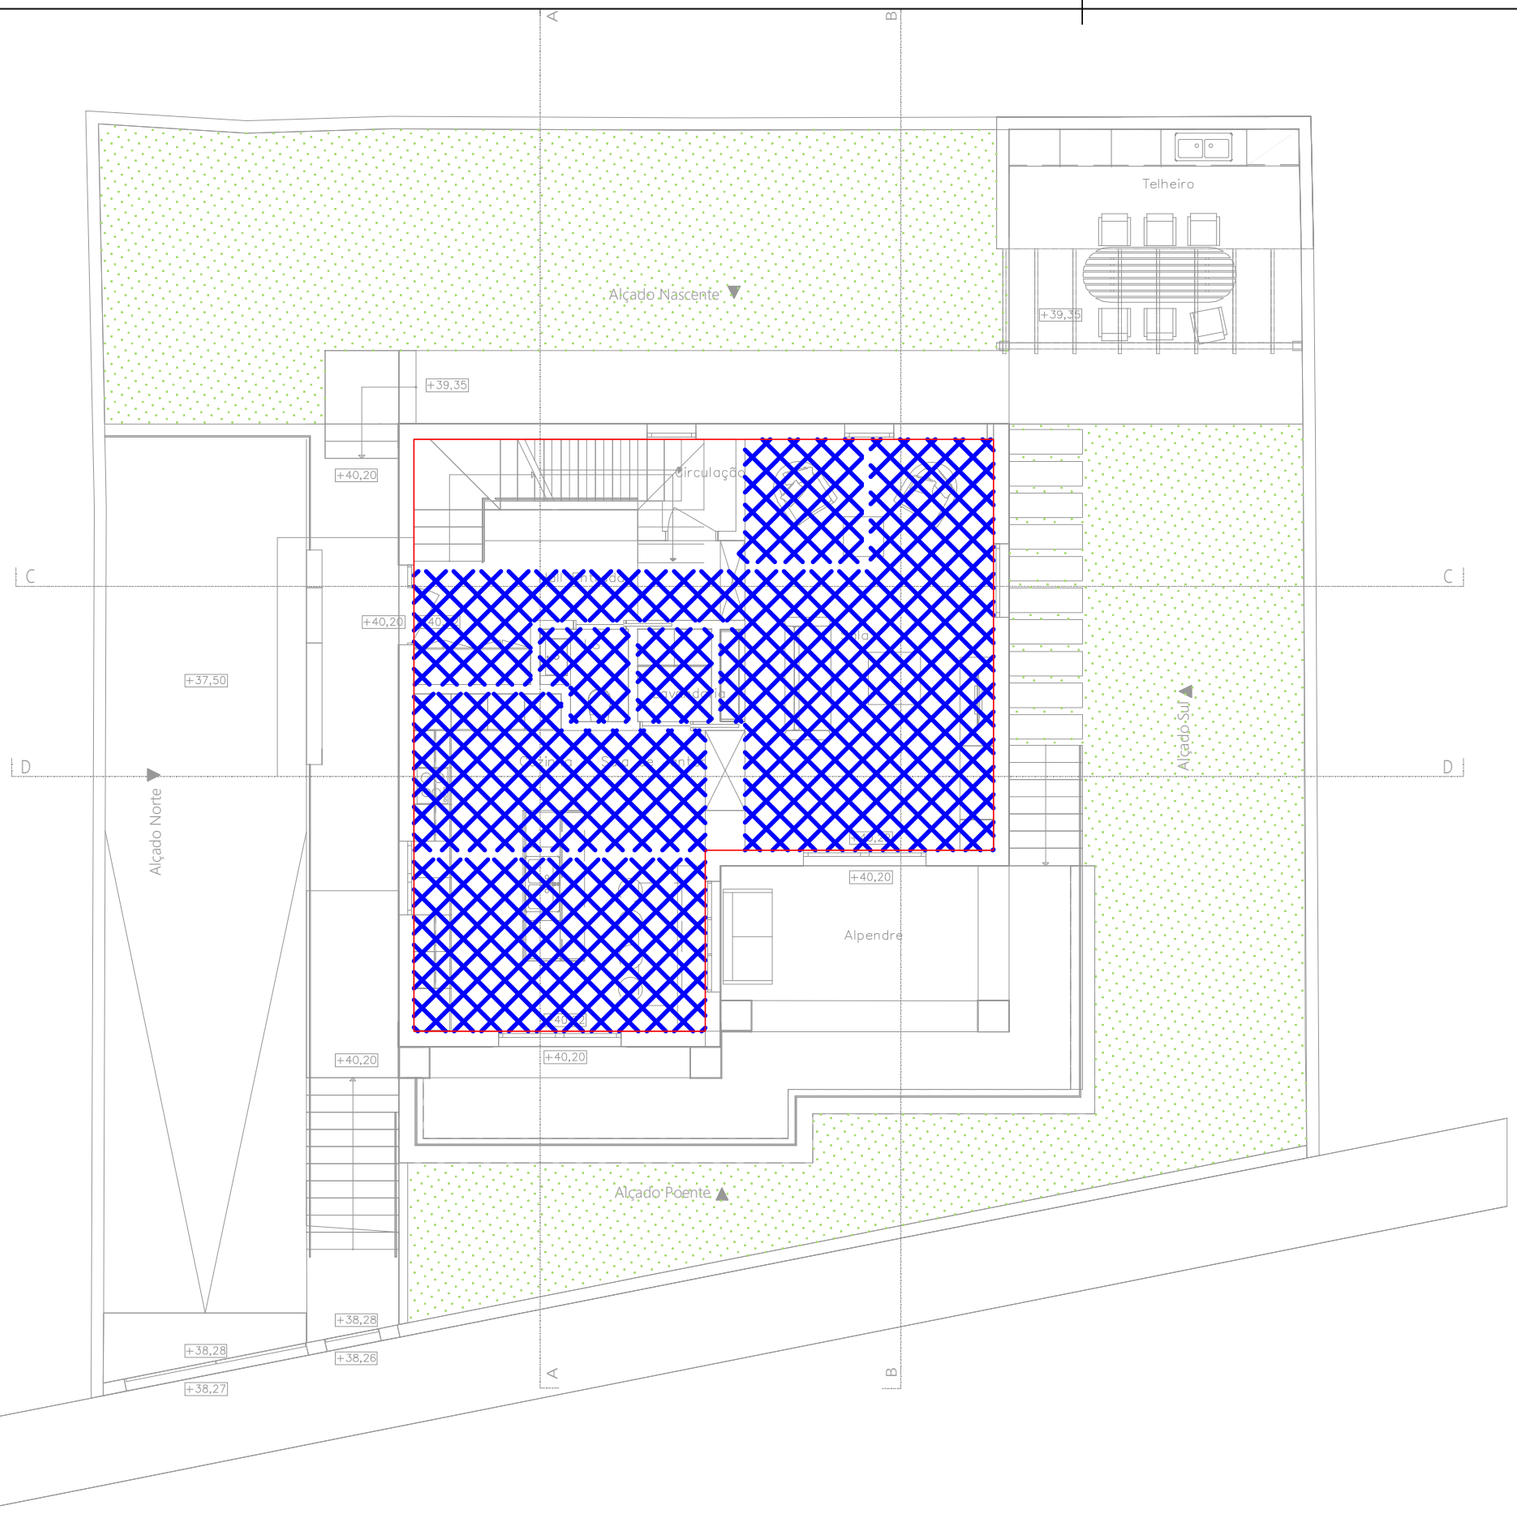

Planta do Piso 0

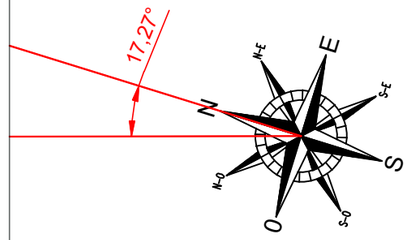

Legenda:

- Pavimento interior com requisitos de interior - PavI1
- Pavimento em contacto com o solo - PavS1
- Envolvente exterior - ParE1
- Envolvente interior com requisitos de interior - ParI1
- Envolvente em contacto com o solo - ParS1

GAPLR ENGENHARIA LDA

Telem.: 967 068 588 | fax: 219 863 894 | GAPLRgeral@gmail.com

PROJETO
CONSTRUÇÃO DE MORADIA UNIFAMILIAR

ESPECIALIDADE
COMPORTAMENTO TÉRMICO

DESIGNAÇÃO
Plt. de envol. - Pav. do Piso 0

REQUERENTE
NATASHA LARA SANTRIC


LOCAL
PRACETA DA ABADIA LOTE 13
ERICEIRA
MAFRA


DATA	PROCESSO	ESCALA
JUL DE 2026	3775	1/100

TÉCNICO
Eng.º Luis Reis
21981 O.E.

DESENHO N.º
08

A3 (297x420mm)

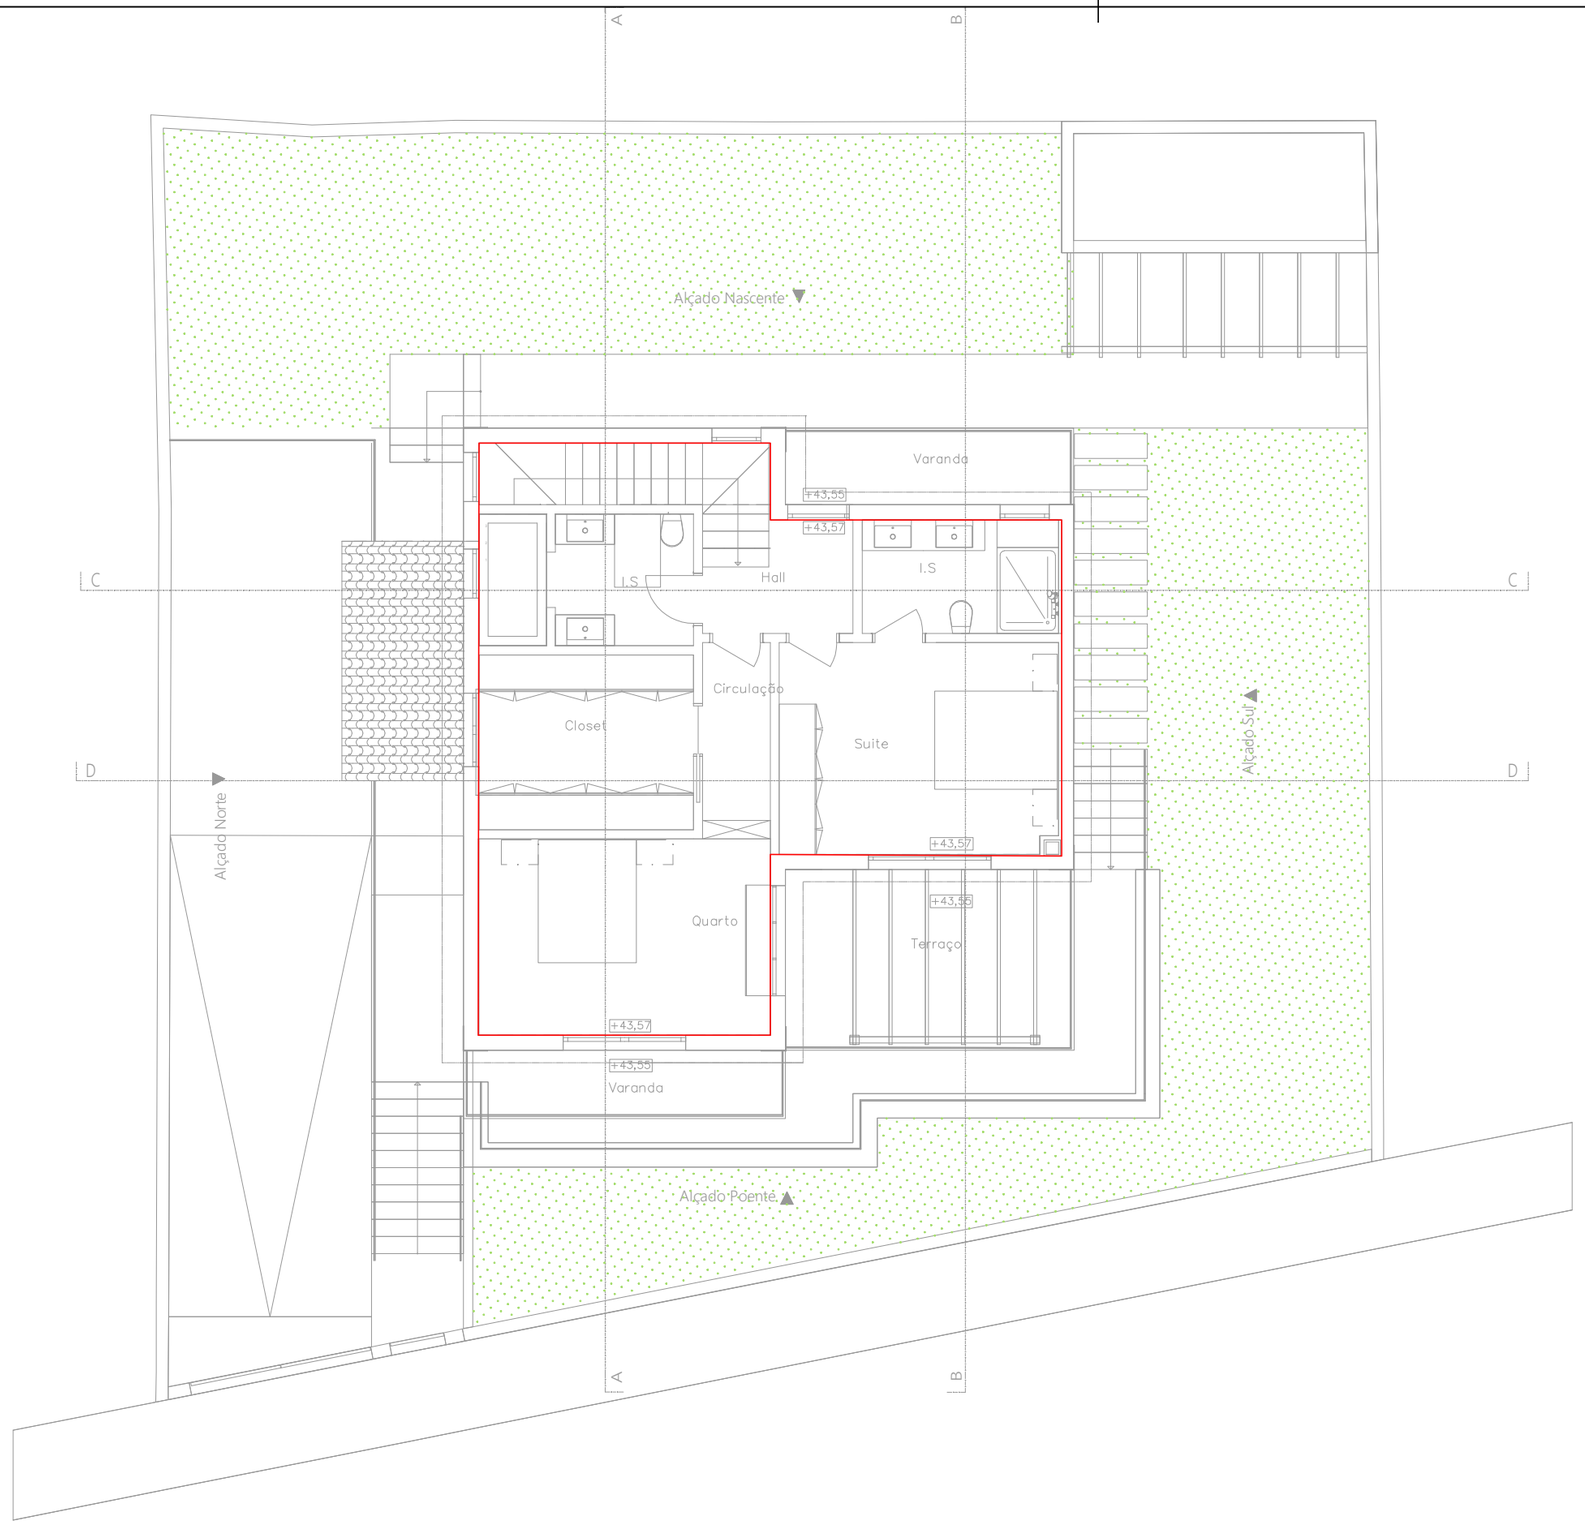

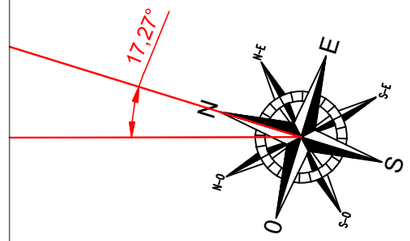

Legenda:

- Pavimento interior com requisitos de interior - PavI1
- Pavimento em contacto com o solo - PavS1
- Envolvente exterior - ParE1
- Envolvente interior com requisitos de interior - ParI1
- Envolvente em contacto com o solo - ParS1

Planta do Piso 1

A3 (297x420mm)

GAPLR ENGENHARIA LDA
Telem.: 967 068 588 | fax: 219 863 894 | GAPLRgeral@gmail.com

PROJETO
CONSTRUÇÃO DE MORADIA UNIFAMILIAR

ESPECIALIDADE
COMPORTAMENTO TÉRMICO

DESIGNAÇÃO
Plt. de envol. - Pav. do Piso 1


REQUERENTE
NATASHA LARA SANTRIC


LOCAL
PRACETA DA ABADIA LOTE 13
ERICEIRA
MAFRA

DATA	PROCESSO	ESCALA
JUL DE 2026	3775	1/100

TÉCNICO
Eng.º Luis Reis
21981 O.E.

DESENHO N.º
09

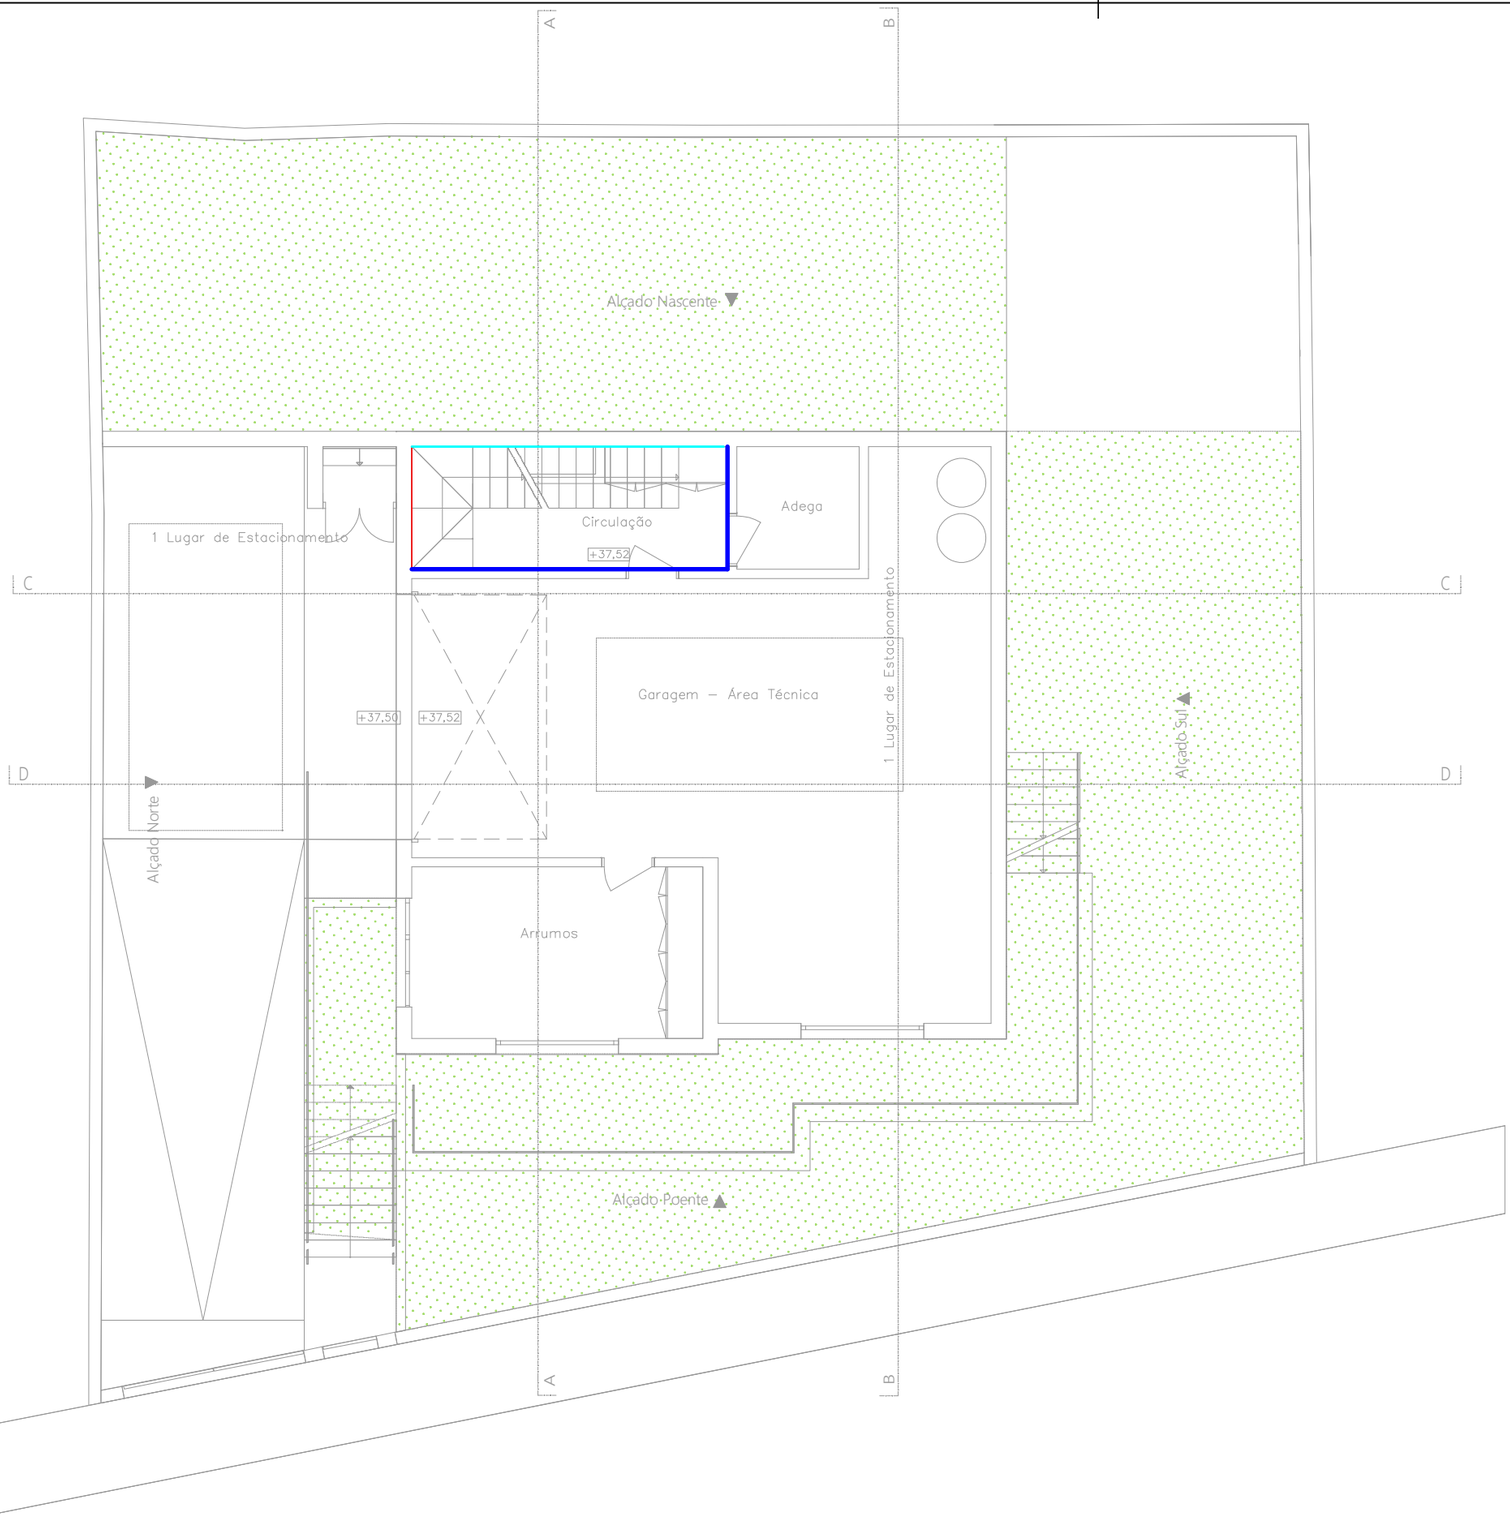

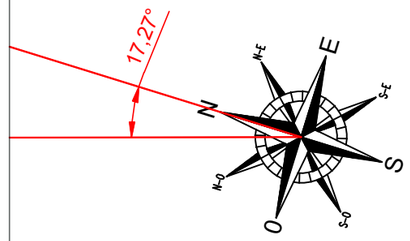

Legenda:

- Cobertura exterior - CobE1
- Cobertura exterior - CobE2
- Envolvente exterior - ParE1
- Envolvente interior com requisitos de interior - ParI1
- Envolvente em contacto com o solo - ParS1

Planta do Piso -1

A3 (297x420mm)

GAPLR ENGENHARIA LDA
Telem.: 967 068 588 | fax: 219 863 894 | GAPLRgeral@gmail.com

PROJETO
CONSTRUÇÃO DE MORADIA UNIFAMILIAR

ESPECIALIDADE
COMPORTAMENTO TÉRMICO

DESIGNAÇÃO
Plt. de envol. - Cob. do Piso -1


REQUERENTE
NATASHA LARA SANTRIC

LOCAL
PRACETA DA ABADIA LOTE 13
ERICEIRA
MAFRA


DATA	PROCESSO	ESCALA
JUL DE 2026	3775	1/100

TÉCNICO
Eng.º Luis Reis
21981 O.E.

DESENHO N.º
10

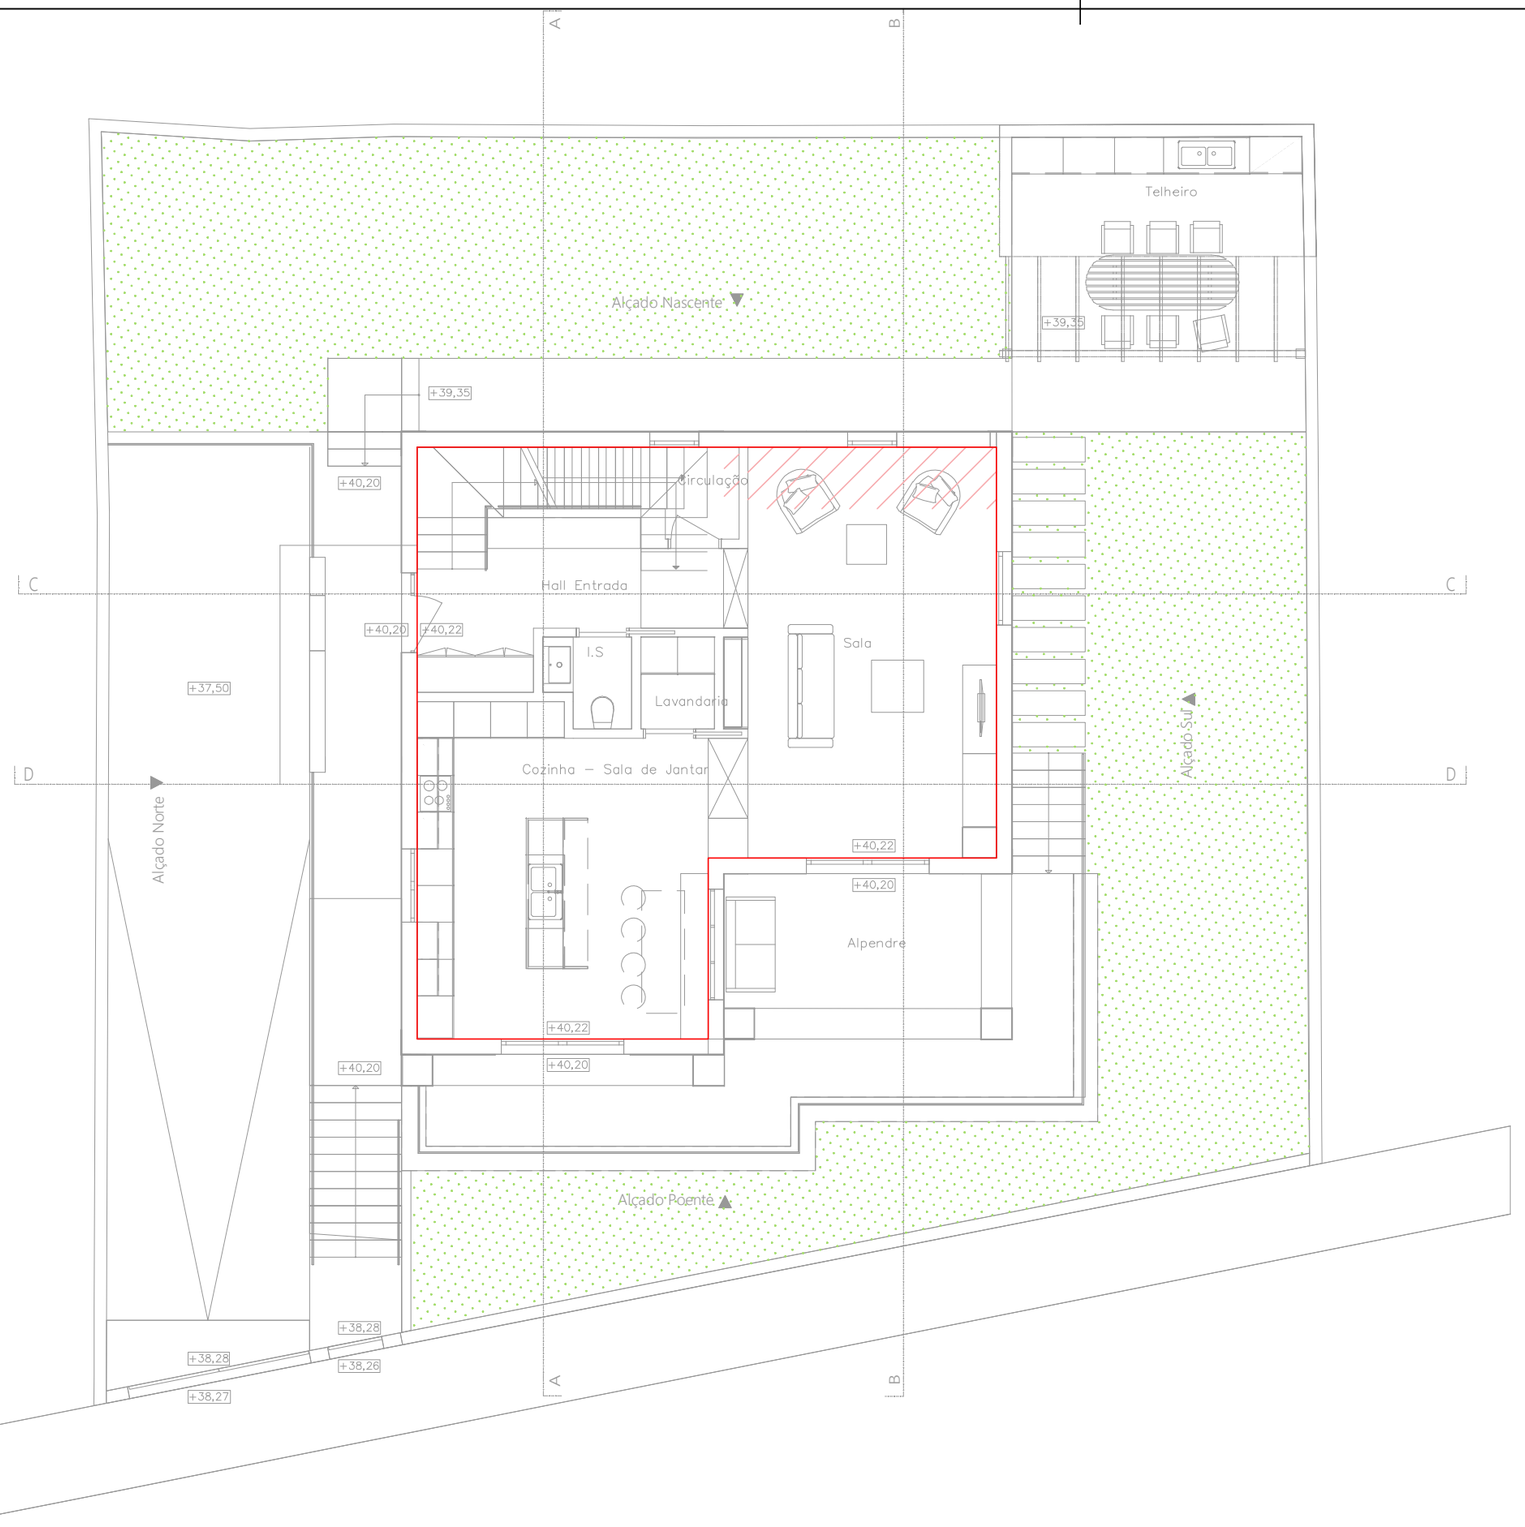

Planta do Piso 0

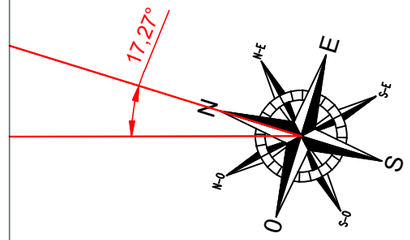

Legenda:

- Cobertura exterior - CobE1
- Cobertura exterior - CobE2
- Envolvente exterior - ParE1
- Envolvente interior com requisitos de interior - ParI1
- Envolvente em contacto com o solo - ParS1

GAPLR ENGENHARIA LDA

Telem.: 967 068 588 | fax: 219 863 894 | GAPLRgeral@gmail.com

PROJETO
CONSTRUÇÃO DE MORADIA UNIFAMILIAR

ESPECIALIDADE
COMPORTAMENTO TÉRMICO

DESIGNAÇÃO
Plt. de envol. - Cob. do Piso 0

REQUERENTE
NATASHA LARA SANTRIC


LOCAL
PRACETA DA ABADIA LOTE 13
ERICEIRA
MAFRA

DATA	PROCESSO	ESCALA
JUL DE 2026	3775	1/100


TÉCNICO
Eng.º Luis Reis
21981 O.E.

DESENHO N.º
11

A3 (297x420mm)

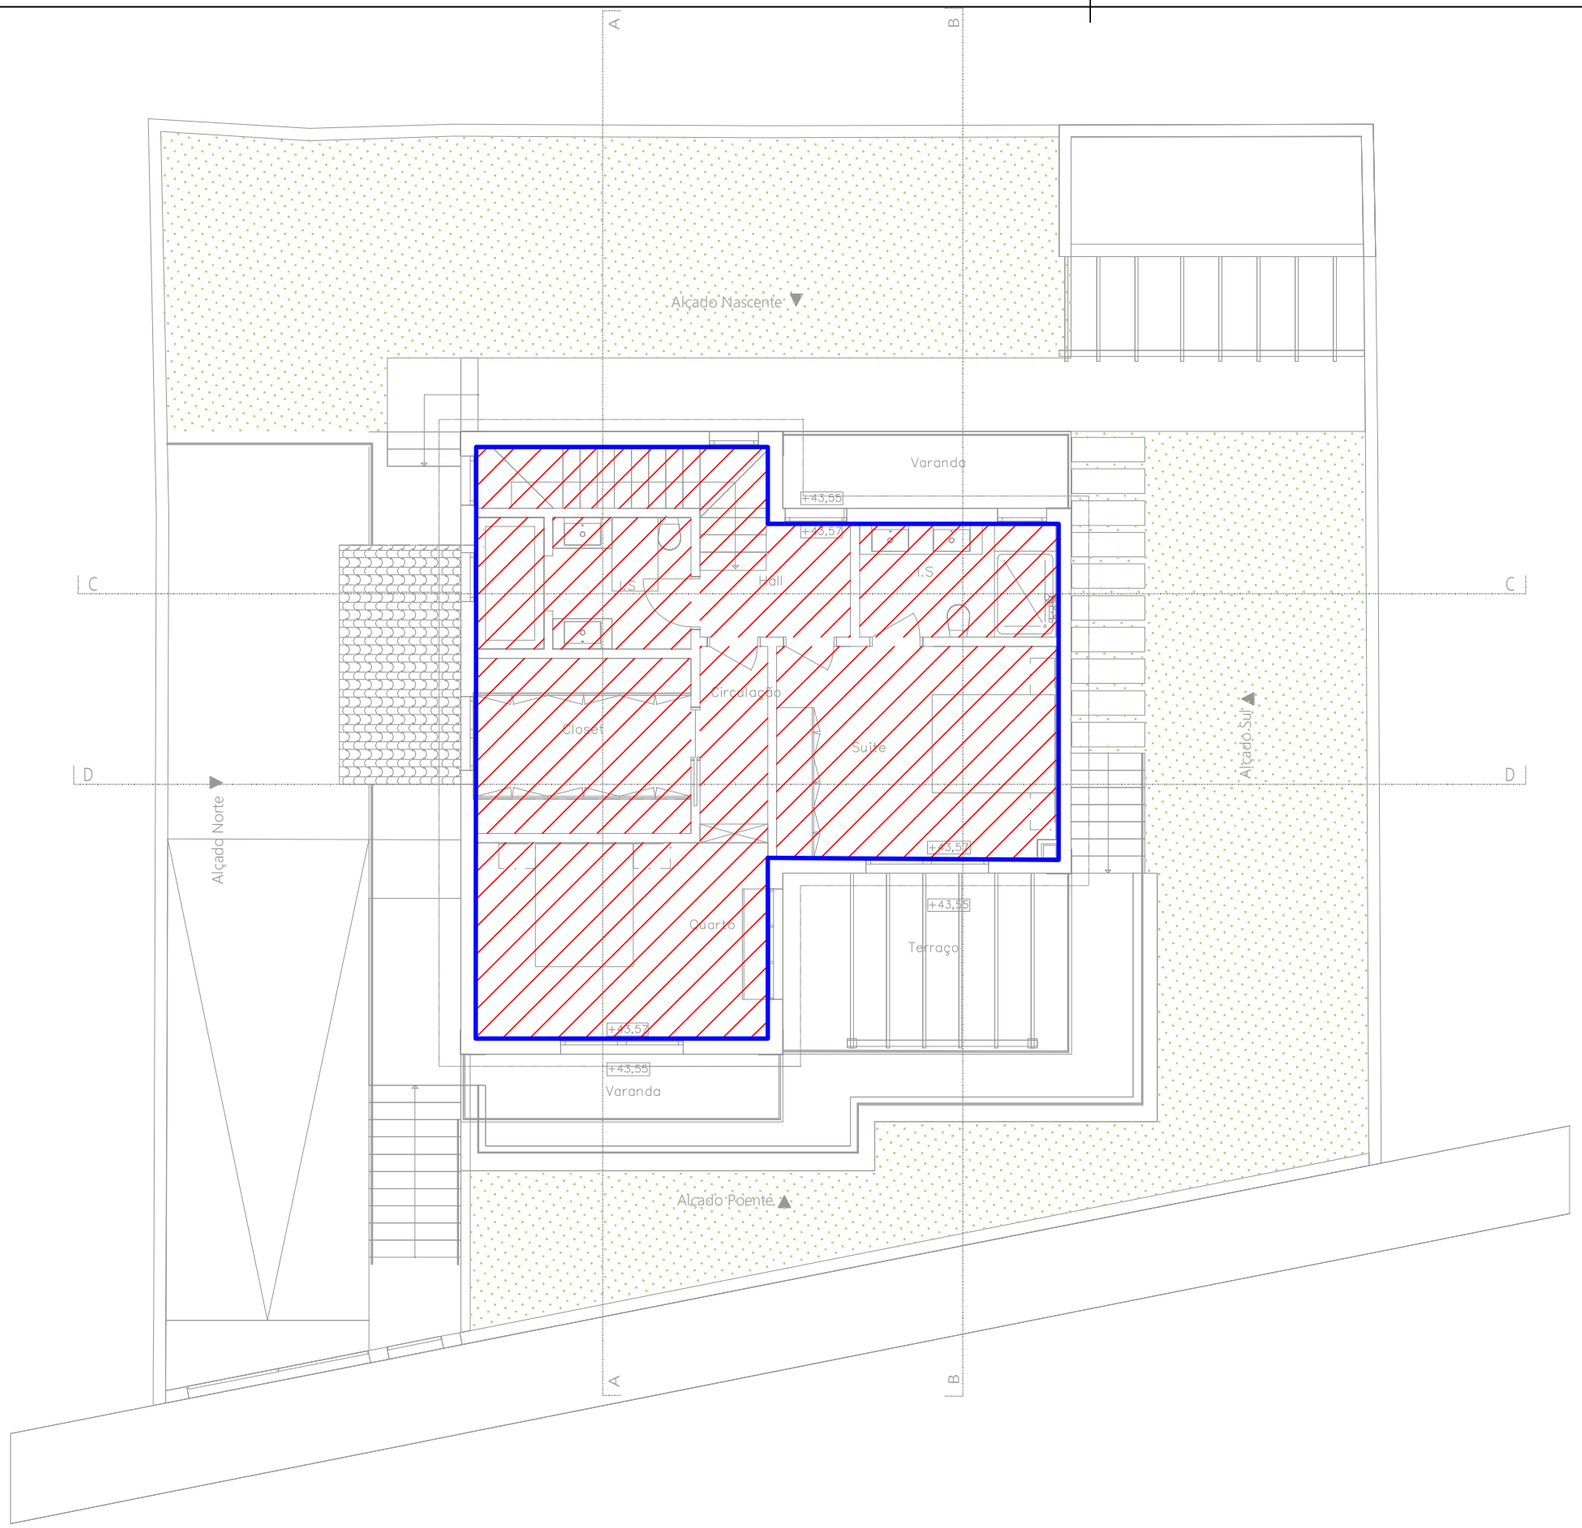

Planta do Piso 1

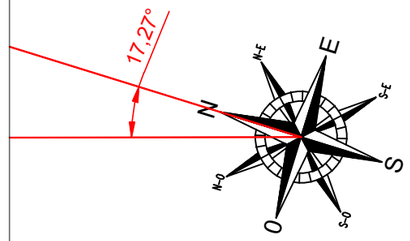

Legenda:

- Cobertura exterior - CobE1
- Cobertura exterior - CobE2
- Envolvente exterior - ParE1
- Envolvente interior com requisitos de interior - ParI1
- Envolvente em contacto com o solo - ParS1

GAPLR ENGENHARIA LDA

Telem.: 967 068 588 | fax: 219 863 894 | GAPLRgeral@gmail.com

PROJETO
CONSTRUÇÃO DE MORADIA UNIFAMILIAR

ESPECIALIDADE
COMPORTAMENTO TÉRMICO

DESIGNAÇÃO
Plt. de envol. - Cob. do Piso 1

REQUERENTE
NATASHA LARA SANTRIC

LOCAL
PRACETA DA ABADIA LOTE 13
ERICEIRA
MAFRA

DATA	PROCESSO	ESCALA
JUL DE 2026	3775	1/100

TÉCNICO
Eng.º Luis Reis
21981 O.E.

DESENHO N.º
12

A3 (297x420mm)