ÍNDICE PEÇAS DESENHADAS

DESENHO N.º	DESIGNAÇÃO	ESCALA
01	PLANTA DO PISO 0	1/100
02	PLANTA DO PISO 1	1/100

GAPLR
ENGENHARIA LDA

Telem.: 967 068 588 | fax: 219 863 894 | GAPLRgeral@gmail.com

PROJETO
CONSTRUÇÃO DE HABITAÇÃO UNIFAMILIAR

ESPECIALIDADE
COMPORTAMENTO ACÚSTICO

DESIGNAÇÃO
ÍNDICE

REQUERENTE
Natasha Lara Santric

LOCAL
Praceta da Abadia, Lote 13
Ericeira
Mafra


DATA	PROCESSO	ESCALA
julho 2026	3775	-/--

TÉCNICO
Eng.º Luis Reis
21981 O.E.

DESENHO N.º
00

SIMBOLOGIA (ELEMENTOS VERTICAIS):

- PEXT.01 - PAREDES EXTERIORES
- ENV.01 - ENVIDRAÇADOS (33 dB)
- ENV.02 - ENVIDRAÇADOS (39 dB)

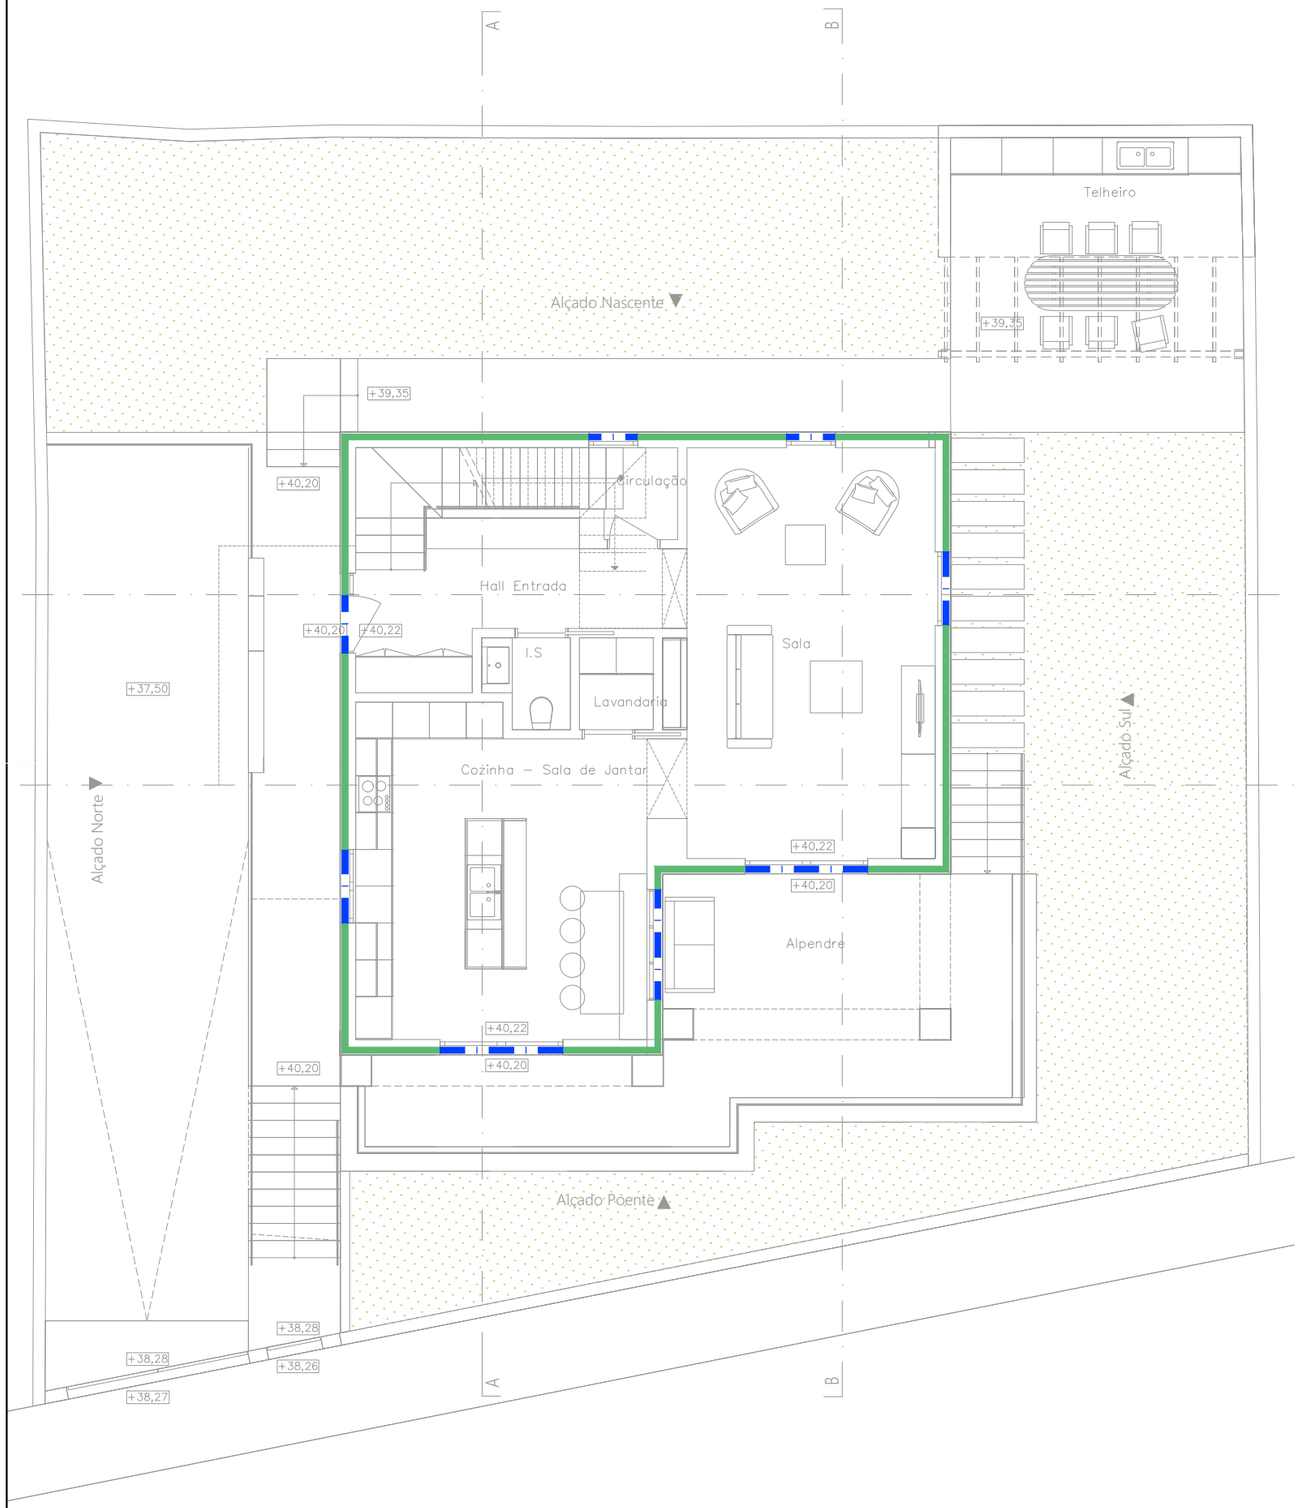

GAPLR
ENGENHARIA LDA

Telem.: 967 068 588 | fax: 219 863 894 | GAPLRgeral@gmail.com

PROJETO
CONSTRUÇÃO DE HABITAÇÃO UNIFAMILIAR

ESPECIALIDADE
COMPORTAMENTO ACÚSTICO

DESIGNAÇÃO
PLANTA DO PISO 0

REQUERENTE
Natasha Lara Santric


LOCAL
Praceta da Abadia, Lote 13
Ericeira
Mafra

DATA	PROCESSO	ESCALA
julho 2026	3775	1/100

TÉCNICO	DESENHO N.º
Eng.º Luis Reis 21981 O.E.	**01**

SIMBOLOGIA (ELEMENTOS VERTICAIS):

- PEXT.01 - PAREDES EXTERIORES
- ENV.01 - ENVIDRAÇADOS (33 dB)
- ENV.02 - ENVIDRAÇADOS (39 dB)

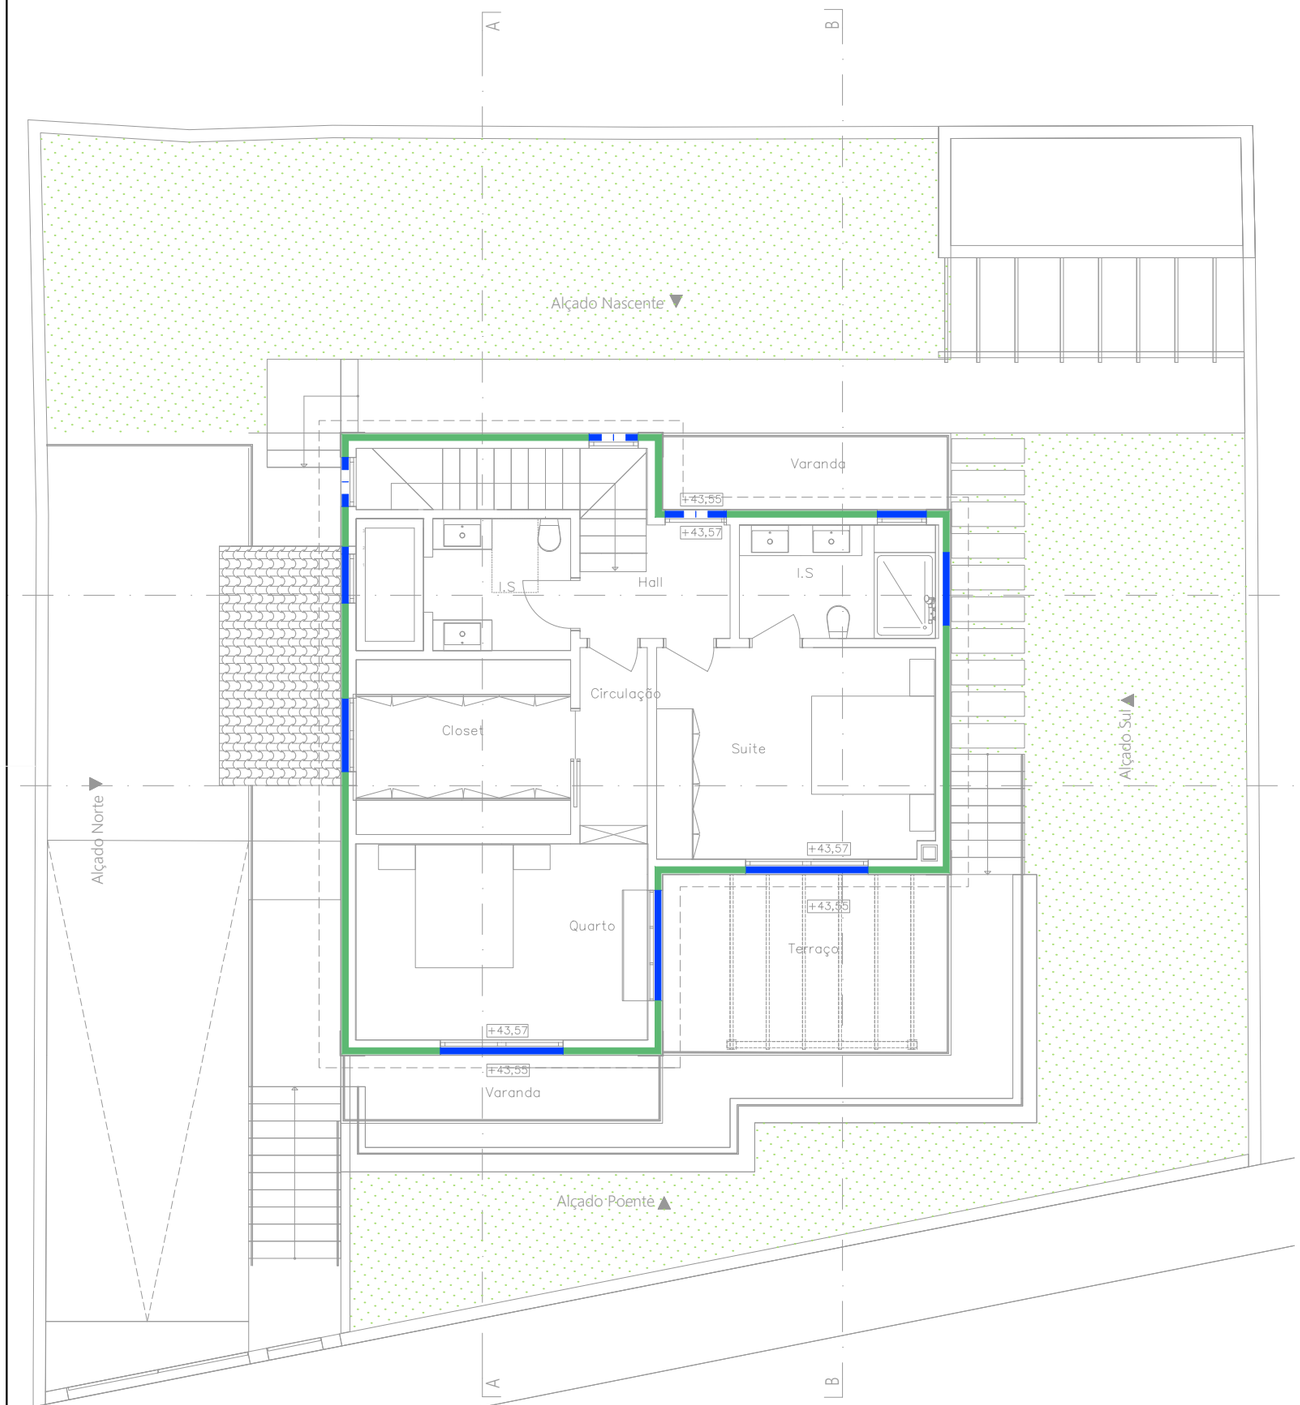

GAPLR
ENGENHARIA LDA

Telem.: 967 068 588 | fax: 219 863 894 | GAPLRgeral@gmail.com

PROJETO
CONSTRUÇÃO DE HABITAÇÃO UNIFAMILIAR

ESPECIALIDADE
COMPORTAMENTO ACÚSTICO

DESIGNAÇÃO
PLANTA DO PISO 1

REQUERENTE
Natasha Lara Santric

LOCAL
Praceta da Abadia, Lote 13
Ericeira
Mafra

DATA	PROCESSO	ESCALA
julho 2026	3775	1/100

TÉCNICO	DESENHO N.º
Eng.º Luis Reis 21981 O.E.	**02**